


AGUJAS	P.K.
2	506/084

SEÑALES	P.K.
E2	505/811
E1	507/084

AGUJAS	P.K.
1	506/813

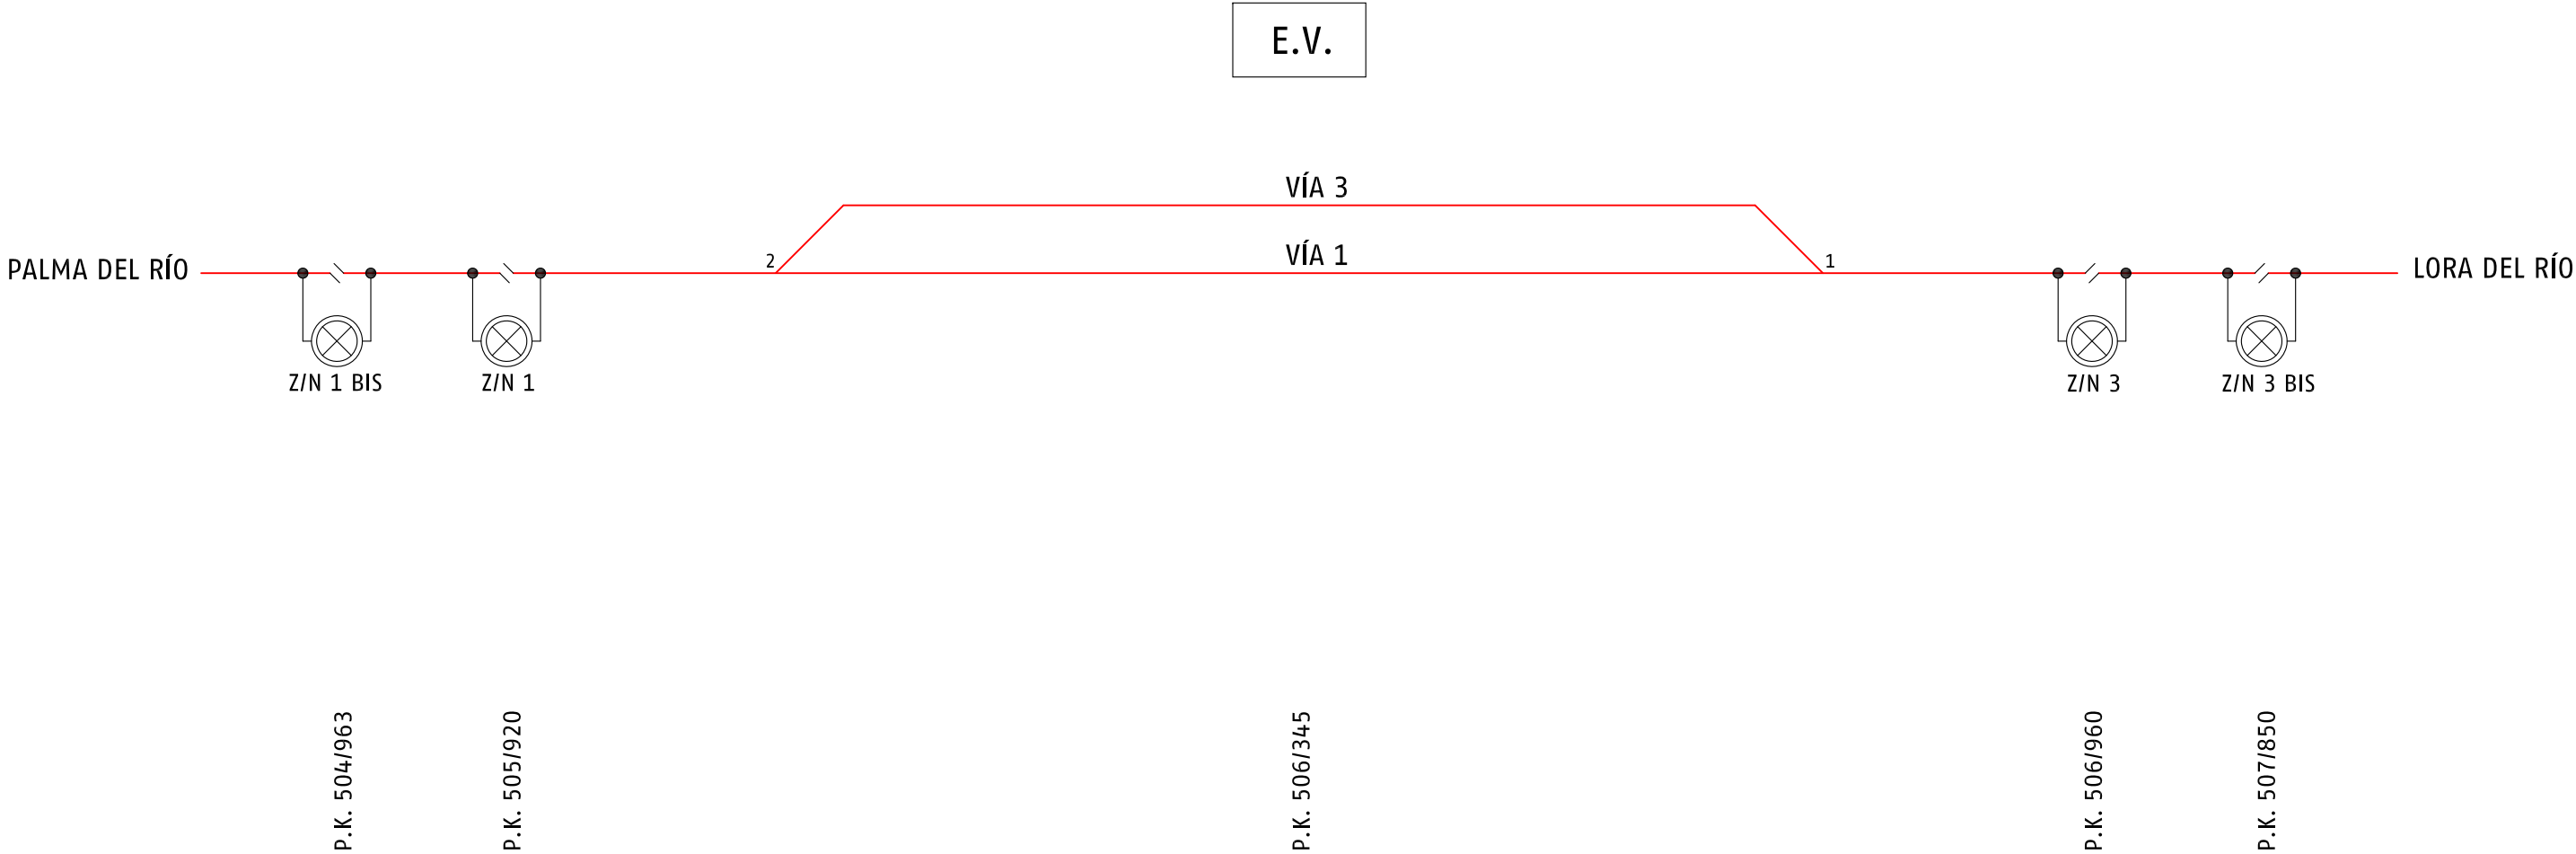

SUBDIRECCIÓN DE OPERACIONES
RED CONVENCIONAL SUR
JEFATURA DE ÁREA DE
MANTENIMIENTO DE SEVILLA

Dibujado por: J.G.J.
Aprobado por: Jose Angel Gomez Flores
Firma: Firmado digitalmente por Jose Angel Gomez Flores Fecha: 2024.07.19 11:19:16 +02'00'
Fecha: 19-JULIO-2024

ESQUEMA ELÉCTRICO L.A.C.
P.E. 17 LÍNEA DE MADRID A SEVILLA
EL PRIORATO

Plano nº 1 de 1
Sustituye a: Hoja 1 de 8 de 26/11/15
Hoja nº 1 de 11