


AGUJAS	P.K.
123	1/276
121	1/367
2	4/128
4	4/686
6	4/725-2/470

SEÑALES LÍNEA	P.K.	SEÑALES RAMAL	P.K.
E3	2/763	E1	5/033
E2A	3/832	E5	5/033
		E6	4/322
		E8	4/294
		E2C	5/754
		E4	5/754

AGUJAS	P.K.
8	6/046
10	6/119
12	6/127
14	6/199
16	6/347
18	6/442

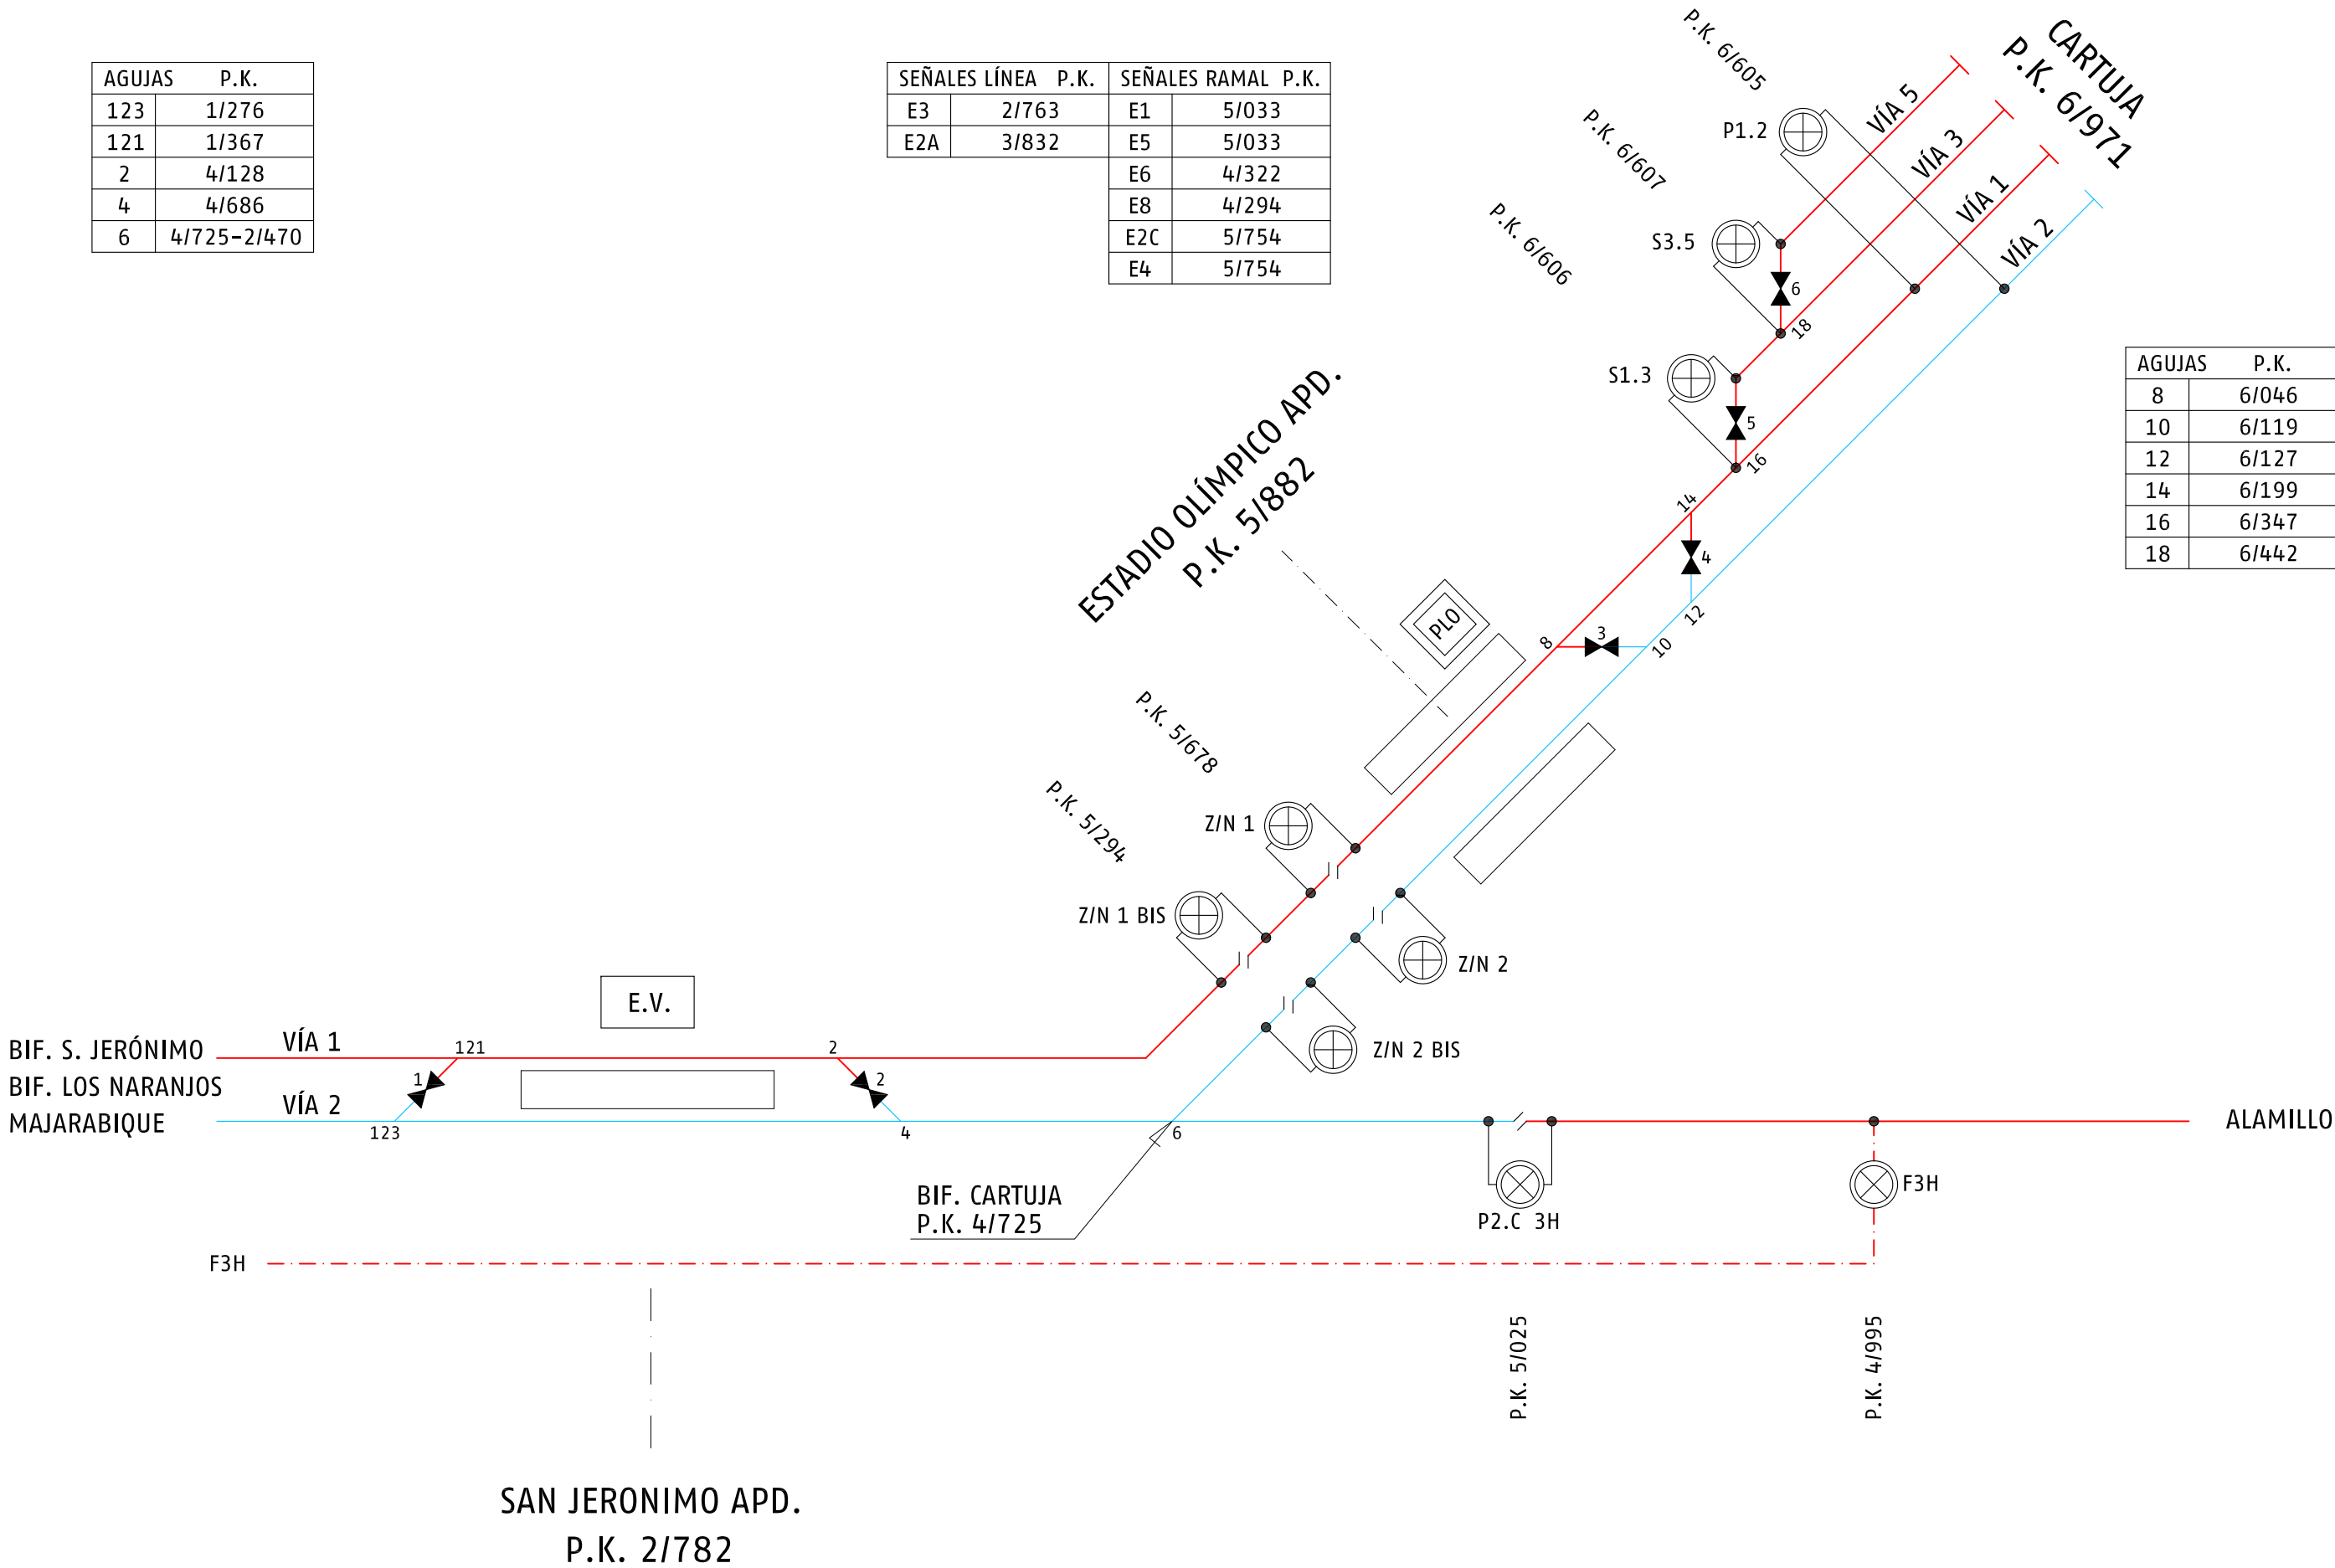

SUBDIRECCIÓN DE OPERACIONES
RED CONVENCIONAL SUR
JEFATURA DE ÁREA DE
MANTENIMIENTO DE SEVILLA

Dibujado por: J.G.J.
Aprobado por: JOSÉ ÁNGEL GÓMEZ FLORES
Firma
Fecha: 22-MARZO-2023

ESQUEMA ELÉCTRICO L.A.C.
P.E. 17 LÍNEA DE MADRID A SEVILLA
BIF. S. JERÓNIMO-BIF. CARTUJA-APD. CARTUJA

Plano nº 1 de 1
Sustituye a:
Hoja nº 10 de 10