


AGUJAS	P.K.	AGUJAS	P.K.
11CT	570/356	34	570/644
10	570/449	40	570/693
12	570/474	48	570/711
16	570/537	44	570/749
18	570/576	46	570/749
24	570/581	56	570/980

SEÑALES	P.K.
E1	1/021
E3	1/021
E2	570/202
E4	570/204
E6	570/945

AGUJAS	P.K.	AGUJAS	P.K.
19	571/631-0/452	9	571/719-0/540
17	571/637-0/458	7	571/751-0/572
15	571/647-0/468	5	571/752-0/573
13	571/674-0/495	3	571/855-0/676
11	571/683-0/504	1	571/927-0/748

PP.KK. en rojo correspondientes a Línea 400
Alcázar de San Juan a Cádiz, Tramo Sevilla a Cádiz

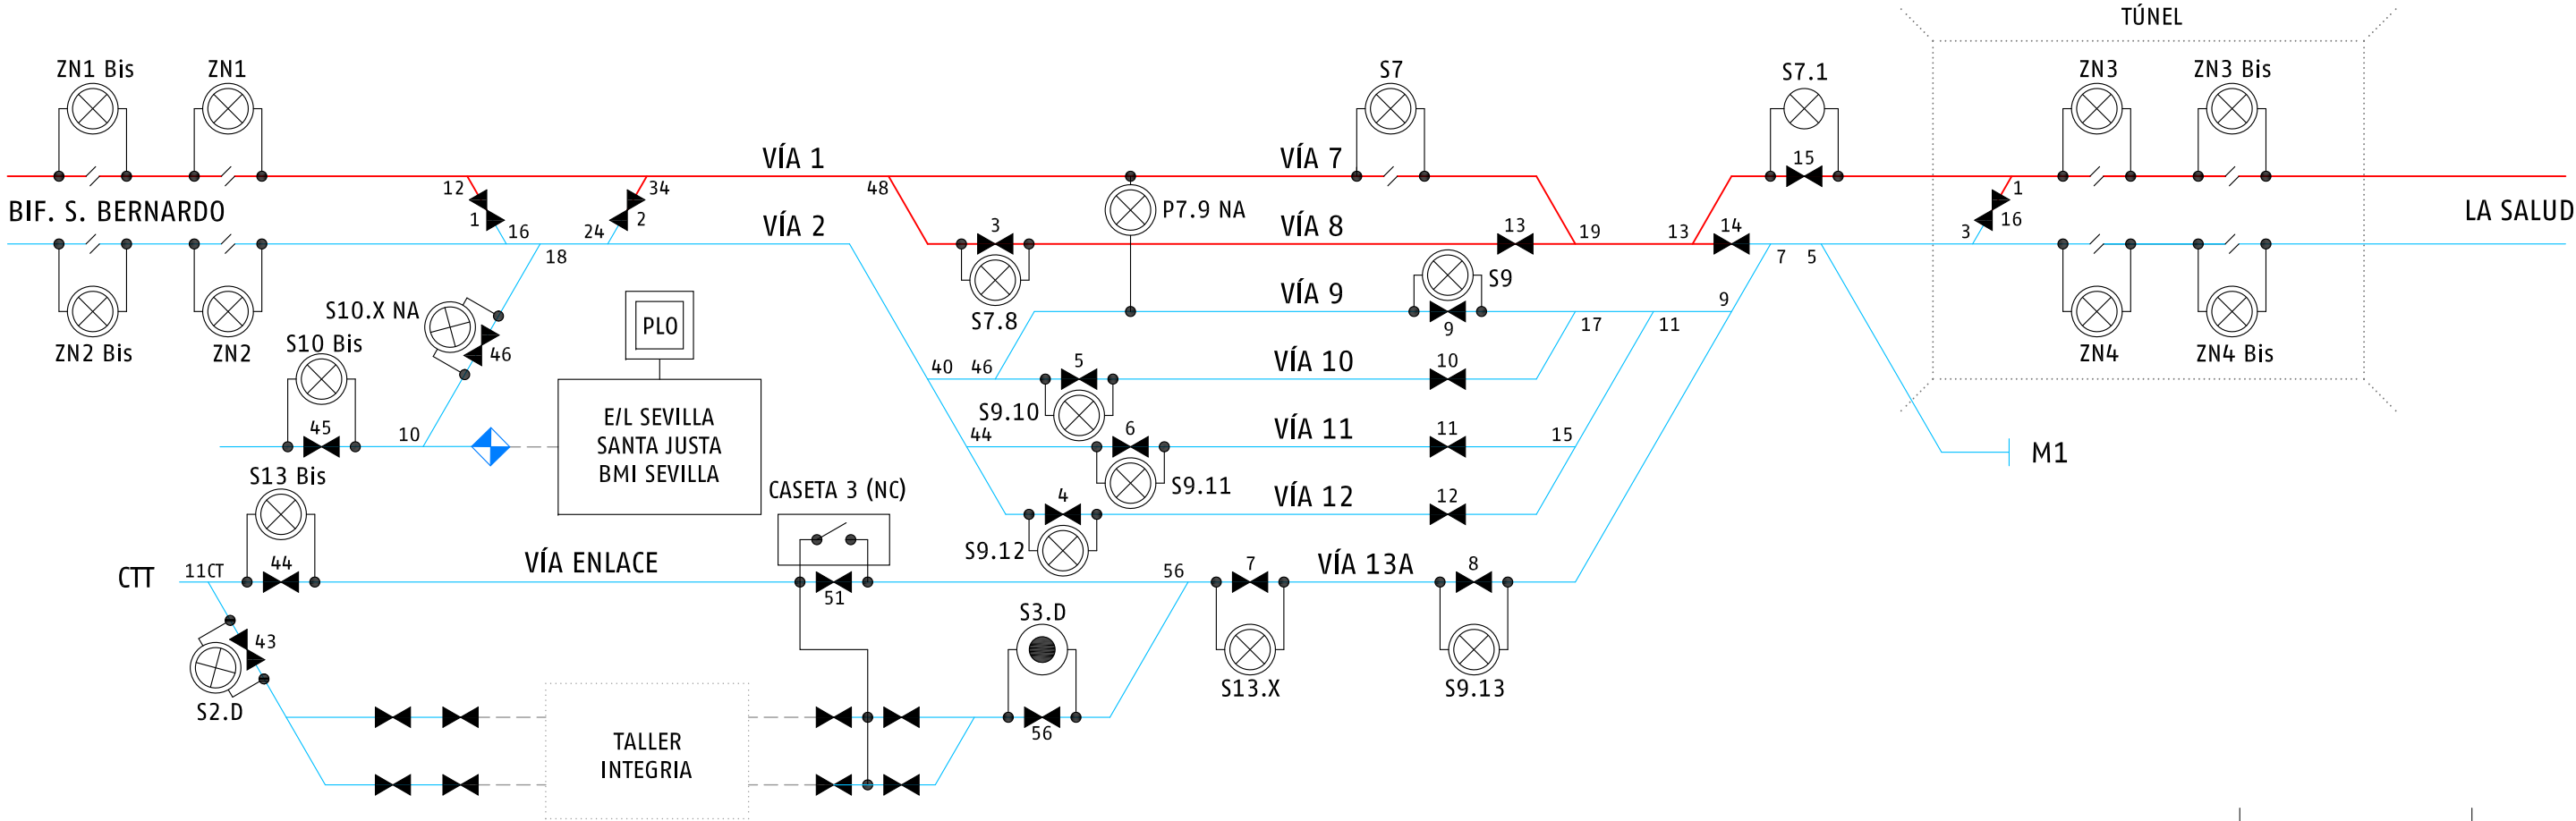

SECCIONADORES P.K.	SECCIONADORES P.K.	SECCIONADORES P.K.	SECCIONADORES P.K.	SECCIONADORES P.K.	SECCIONADORES P.K.
Z1N Bis	569/600	S2.D	570/400	S3.D	570/920
Z2N Bis	569/600	S10 Bis	570/440	S7.8	570/548
Z1N	570/275	S13 Bis	570/400	S9.10	570/844
Z2N	570/275	S10.X	570/530	S9.12	570/820
				S13.X	570/990
				S9.11	570/844
				S7	0/291
				S9.13	0/426
				S9	0/449
				S7.1	0/583
				ZN3	0/850
				ZN4	0/749
				ZN3 Bis	0/980
				ZN4 Bis	0/980

P.K. 0/680

P.K. 2/874

APDO. VIRGEN
SAN BERNARDO DEL ROCIO
P.K. 1+956 P.K. 3+600

NOTA: Esquema que no cumple con la NAE 112