


AGUJAS	P.K.	AGUJAS	P.K.
11CT	570/356	34	570/644
10	570/449	40	570/693
12	570/474	48	570/711
16	570/537	44	570/749
18	570/576	46	570/749
24	570/581	56	570/980

SEÑALES	P.K.
E1	1/021
E3	1/021
E2	570/202
E4	570/204
E6	570/945

AGUJAS	P.K.	AGUJAS	P.K.
19	571/631-0/452	9	571/719-0/540
17	571/637-0/458	7	571/751-0/572
15	571/647-0/468	5	571/752-0/573
13	571/674-0/495	3	571/855-0/676
11	571/683-0/504	1	571/927-0/748

PP.KK. en rojo correspondientes a Línea 400
Alcázar de San Juan a Cádiz, Tramo Sevilla a Cádiz

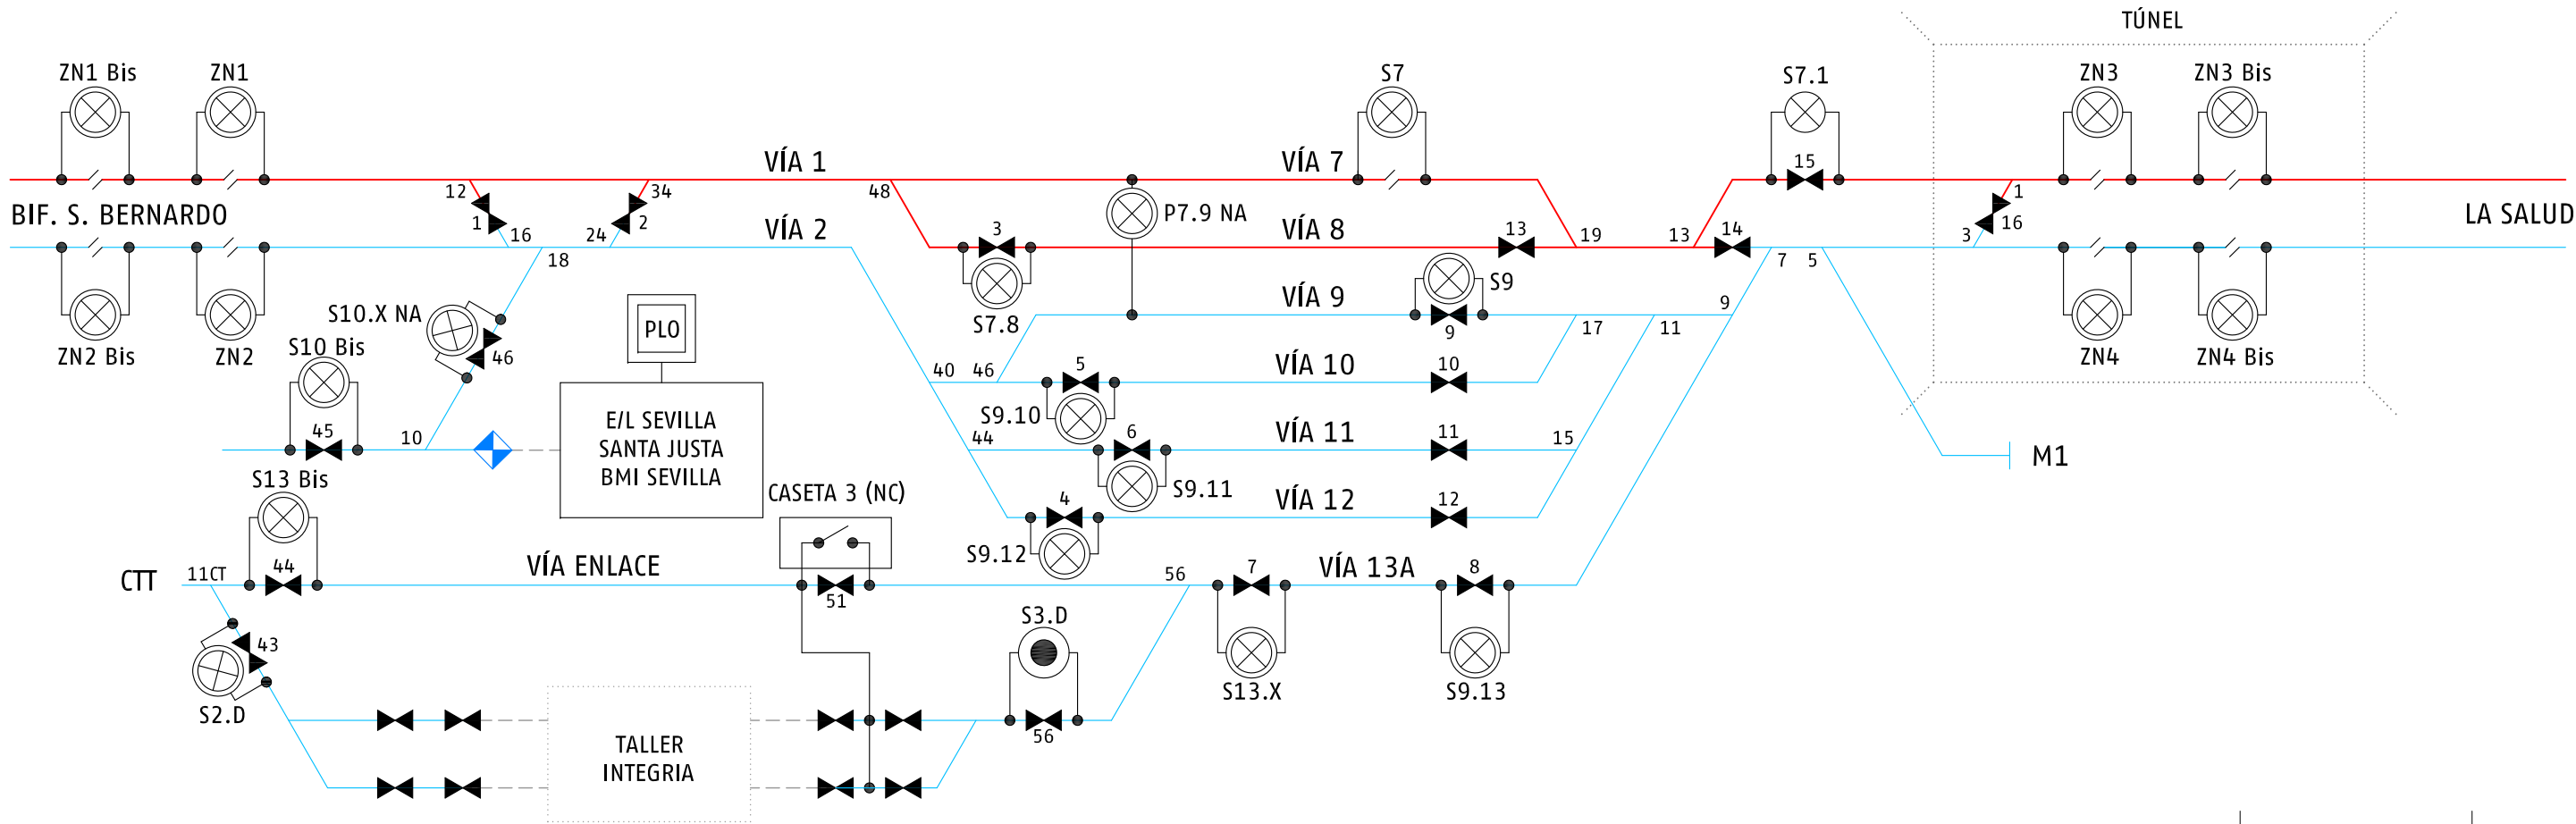

SECCIONADORES P.K.	SECCIONADORES P.K.	SECCIONADORES P.K.	SECCIONADORES P.K.	SECCIONADORES P.K.	SECCIONADORES P.K.
Z1N Bis	569/600	S2.D	570/400	S3.D	570/920
Z2N Bis	569/600	S10 Bis	570/440	S7.8	570/548
Z1N	570/275	S13 Bis	570/400	S9.10	570/844
Z2N	570/275	S10.X	570/530	S9.12	570/820
				S13.X	570/990
				S9.11	570/844

P.K. 0/680

P.K. 2/874

APDO. VIRGEN
SAN BERNARDO DEL ROCIO
P.K. 1+956 P.K. 3+600

NOTA: Esquema que no cumple con la NAE 112

ESQUEMA ELÉCTRICO L.A.C.
P.E. 24 LÍNEA DE SEVILLA A CÁDIZ
SEVILLA SANTA JUSTA

Plano nº	1 de 1
Sustituye a:	Hoja 1 de 21 de 12/05/2021
Hoja nº	01 de 21



SUBDIRECCIÓN DE OPERACIONES
RED CONVENCIONAL SUR
JEFATURA DE ÁREA DE
MANTENIMIENTO DE SEVILLA

Dibujado por:	J.G.J.
Aprobado por:	Jose Angel Gomez Flores
Firma	
Fecha:	19 FEBRERO 2025