


NOTA: Los pp.kk. con * pertenecen a la línea 456

AGUJAS	P.K.	AGUJAS	P.K.	AGUJAS	P.K.
2B	6/057	4	7/176-11/174	18	7/400-11/336
4B	6/177	6	7/215-11/206	20	7/412
6B	6/188-0/000*	8	7/264-11/255	22	7/503
2T	10/080	10	7/272	24	7/504
4T	10/153	12	7/316-11/307	26	7/577
6T	10/161-0/840*	14	7/345		
2	7/095-11/086	16	7/353		

SEÑALES	P.K.	SEÑALES	P.K.
E16	9/702	E6	10/818
E14	5/781	E4	6/831
E12	5/780	E2	7/015
E10	10/818	E1	8/439
E8	6/981	E3	8/440

AGUJAS	P.K.
17	7/962
15	7/812
13	7/903
11	7/927
9	7/934
7	7/962
5	8/007
3	8/048
1	8/139

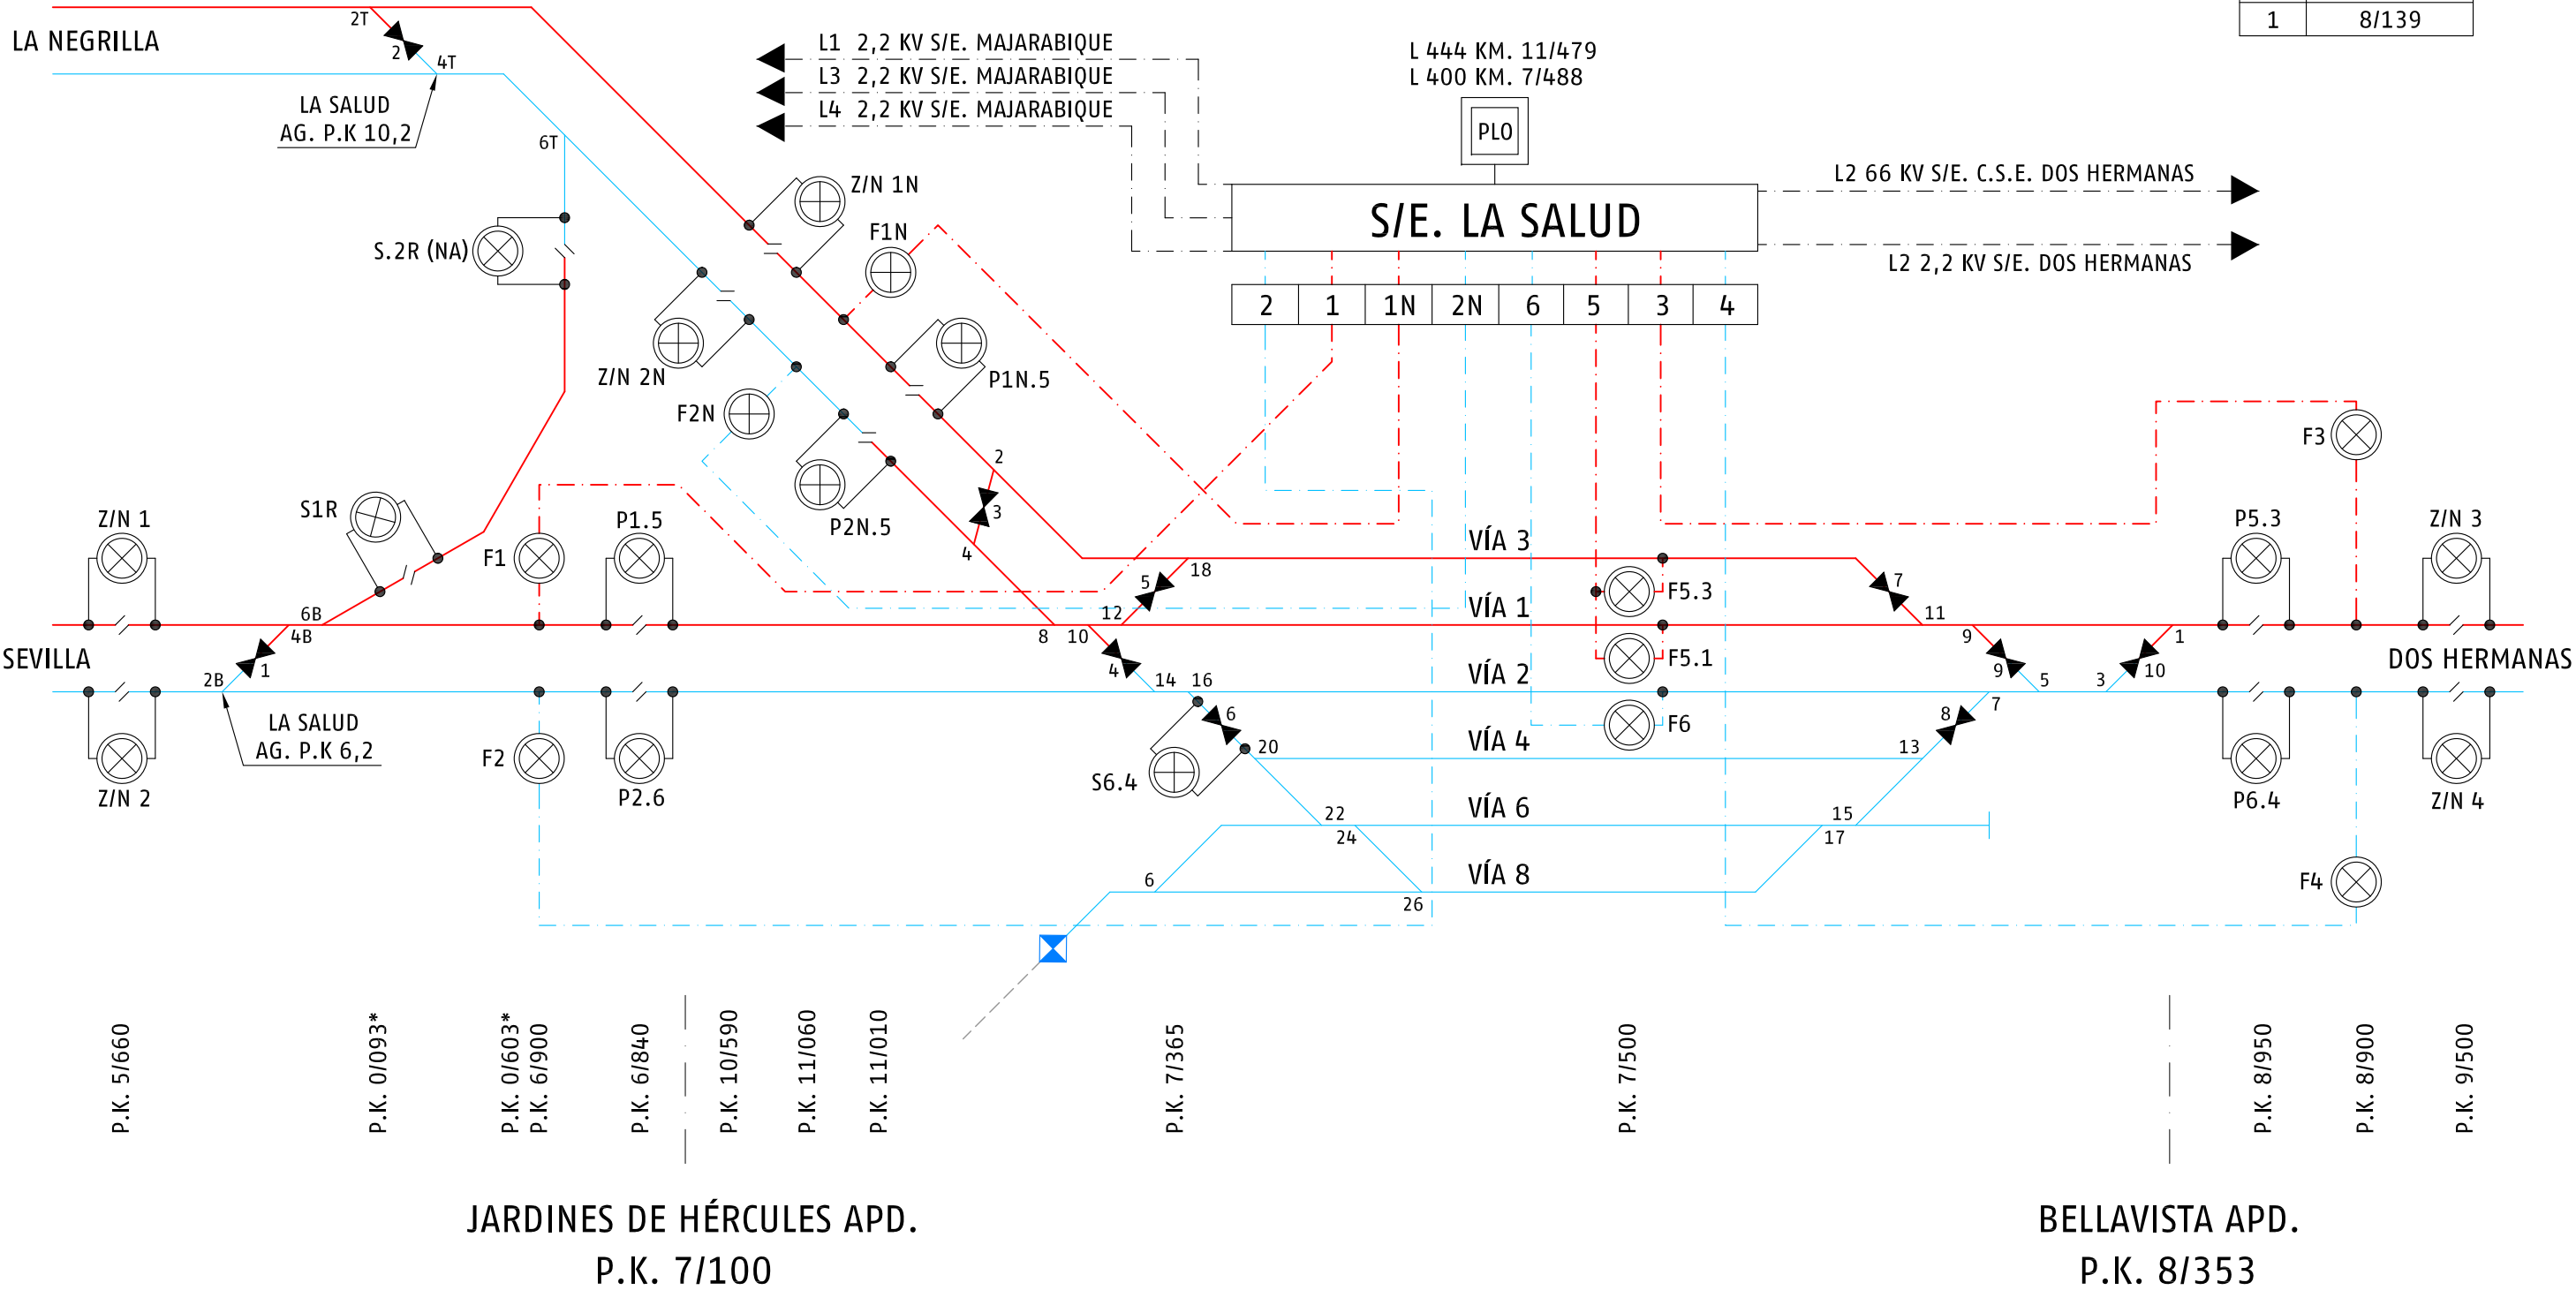

NOTA: Esquema que no cumple con la NAE 112



SUBDIRECCIÓN DE OPERACIONES
RED CONVENCIONAL SUR
JEFATURA DE ÁREA DE
MANTENIMIENTO DE SEVILLA

Dibujado por: J.G.J.
Aprobado por: Jose Angel Gomez Flores
Firma
Fecha: 19 FEBRERO 2025

ESQUEMA ELÉCTRICO L.A.C.
P.E. 24 LÍNEA DE SEVILLA A CÁDIZ
LA SALUD

Plano nº 1 de 1
Sustituye a: Hoja 2 de 21 de 19/11/2015
Hoja nº 02 de 21