


AGUJAS	P.K.	AGUJAS	P.K.
B1	27/341	8	30/733
B2	27/503	10	30/801
B3	27/729	12	30/801
2	30/483	16	30/894
4	30/578	18	31/478
6	30/640	20	31/572

SEÑALES	P.K.
E6	27/080
E8	27/089
E5	28/027
E7	28/027
E2	30/213
E4	30/214
E1	33/075
E3	33/075

AGUJAS	P.K.
11	31/902
9	31/925
7	31/996
5	32/027
3	32/580
1	32/744

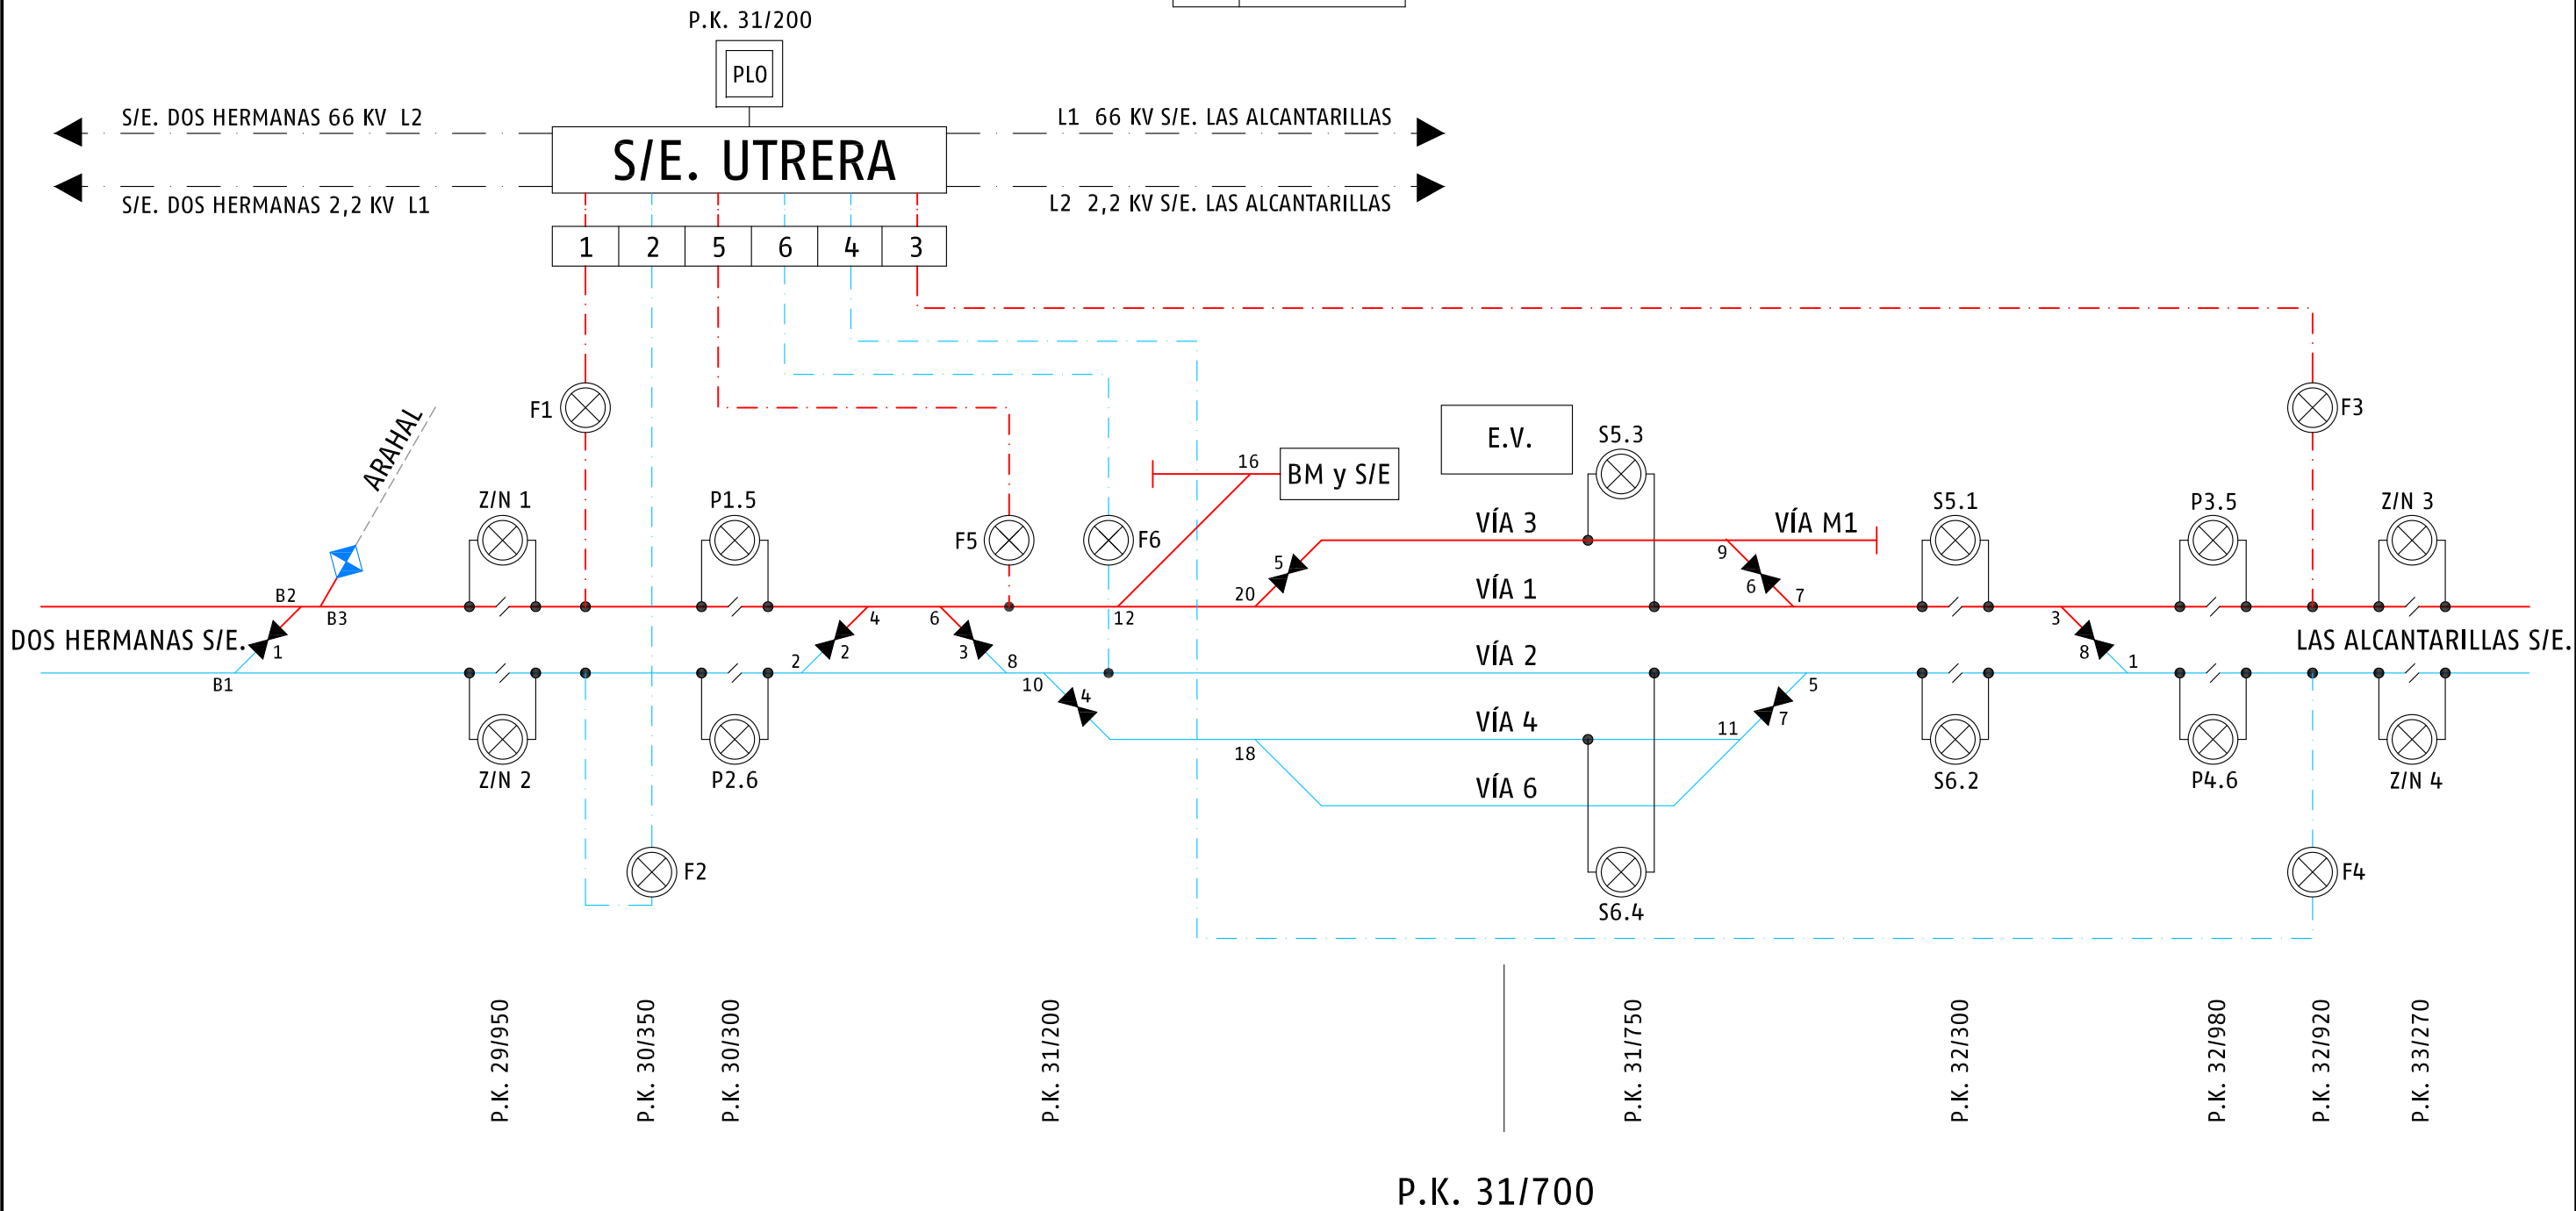

SUBDIRECCIÓN DE OPERACIONES
RED CONVENCIONAL SUR
JEFATURA DE ÁREA DE
MANTENIMIENTO DE SEVILLA

Dibujado por: J.G.J.
Aprobado por: Jose Angel Gomez Flores
Firma: [Firma]
Fecha: 19 FEBRERO 2025

ESQUEMA ELÉCTRICO L.A.C.
P.E. 24 LÍNEA DE SEVILLA A CÁDIZ
UTRERA

Plano nº 1 de 1
Sustituye a: Hoja 5 de 21 de 08/04/21
Hoja nº 05 de 21