


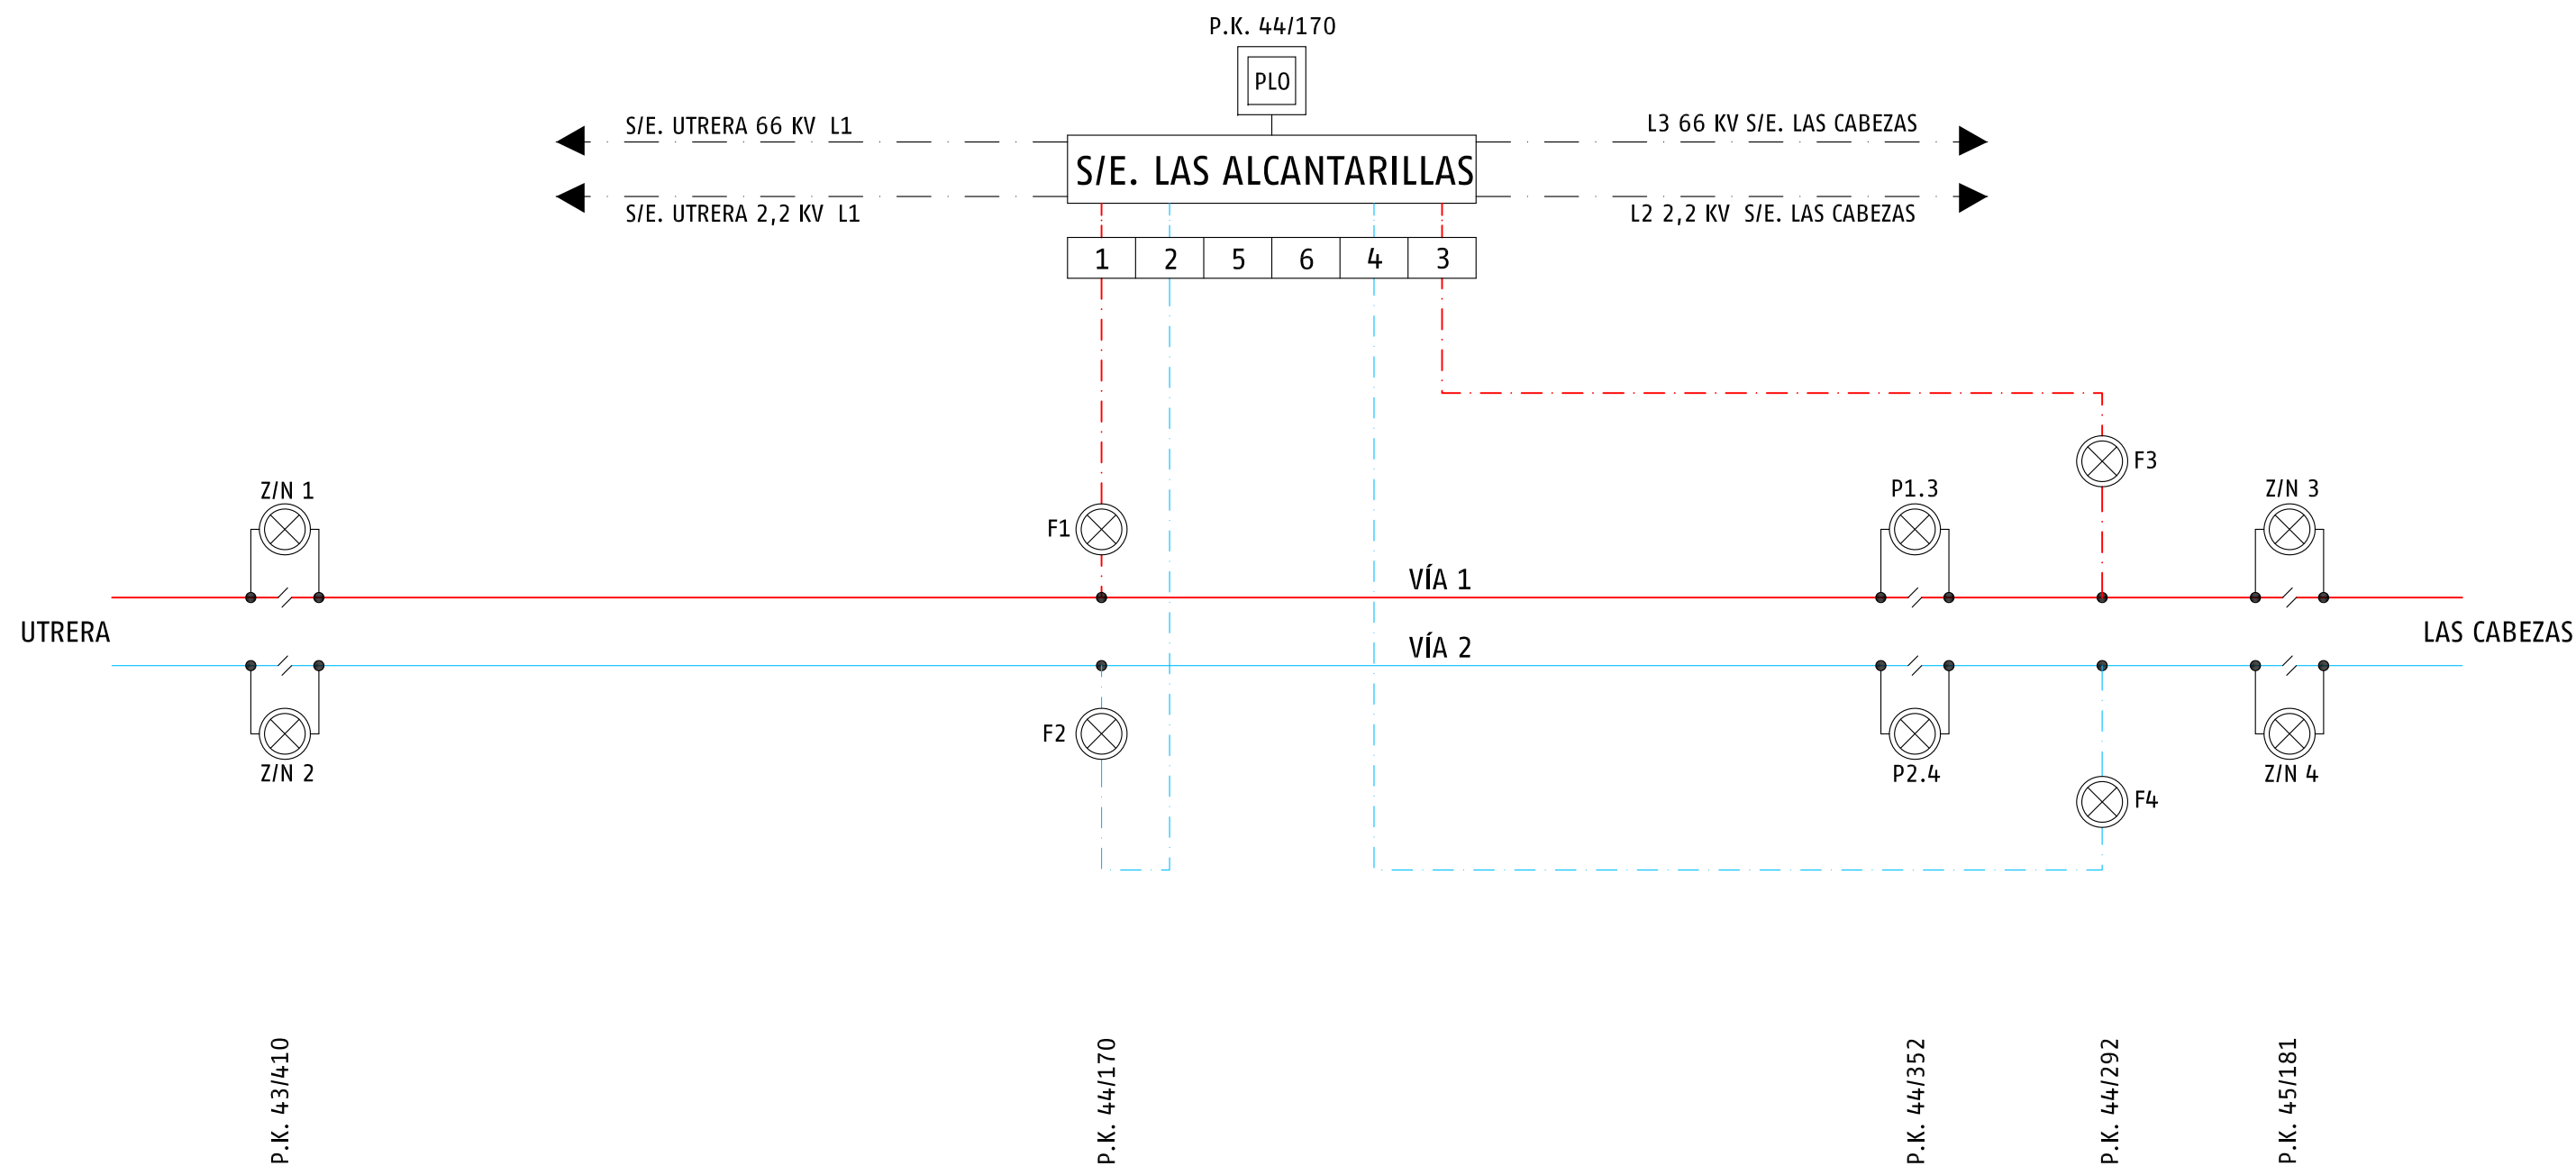

SUBDIRECCIÓN DE OPERACIONES  
RED CONVENCIONAL SUR  
JEFATURA DE ÁREA DE  
MANTENIMIENTO DE SEVILLA

Dibujado por: J.G.J.

Aprobado por: Jose Angel Gomez Flores  
Firma

Fecha: 19 FEBRERO 2025

ESQUEMA ELÉCTRICO L.A.C.  
P.E. 24 LÍNEA DE SEVILLA A CÁDIZ  
**LAS ALCANTARILLAS S/E.**

Plano nº 1 de 1

Sustituye a: Hoja 6 de 21 de 08/04/21

Hoja nº 06 de 21