


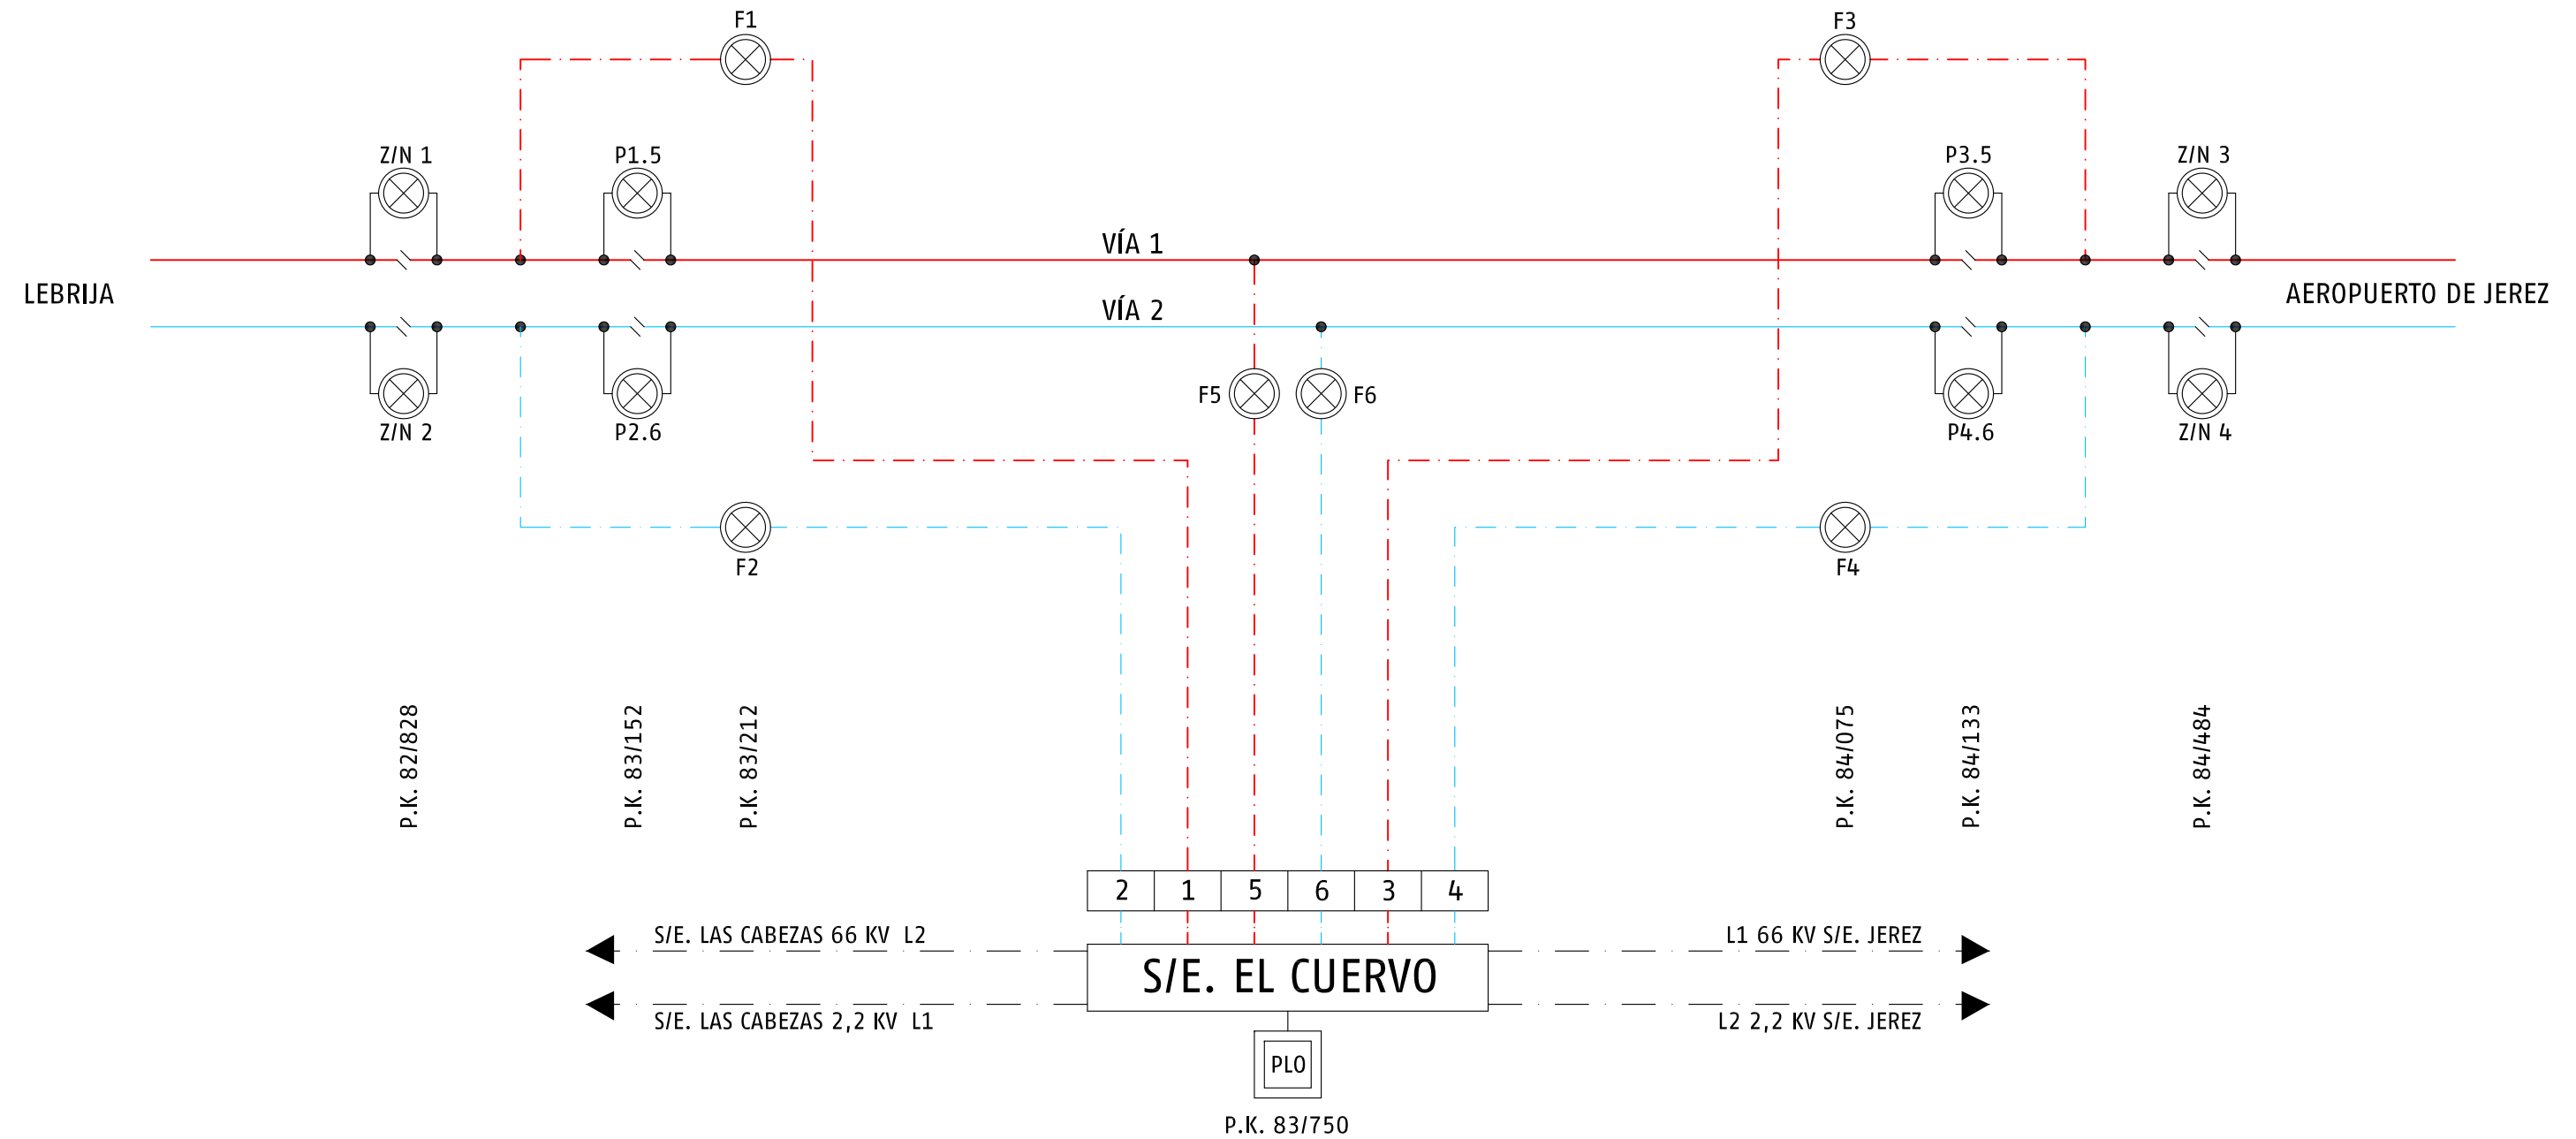

SUBDIRECCIÓN DE OPERACIONES
RED CONVENCIONAL SUR

JEFATURA DE ÁREA DE
MANTENIMIENTO DE SEVILLA

Dibujado por: J.G.J.

Aprobado por: Jose Angel Gomez Flores

Firma

Fecha: 19 FEBRERO 2025

ESQUEMA ELÉCTRICO L.A.C.
P.E. 24 LÍNEA DE SEVILLA A CÁDIZ

EL CUERVO S/E.

Plano nº 1 de 1

Sustituye a: Hoja 10 de 21 de 08/04/21

Hoja nº 10 de 21