


AGUJAS	P.K.
2	93/641
4	93/804
6	93/814
8	93/816
10	93/908

SEÑALES	P.K.
E2	93/350
E4	93/350
E1	94/919
E3	94/919

AGUJAS	P.K.
7	94/466
5	94/466
3	94/476
1	94/639

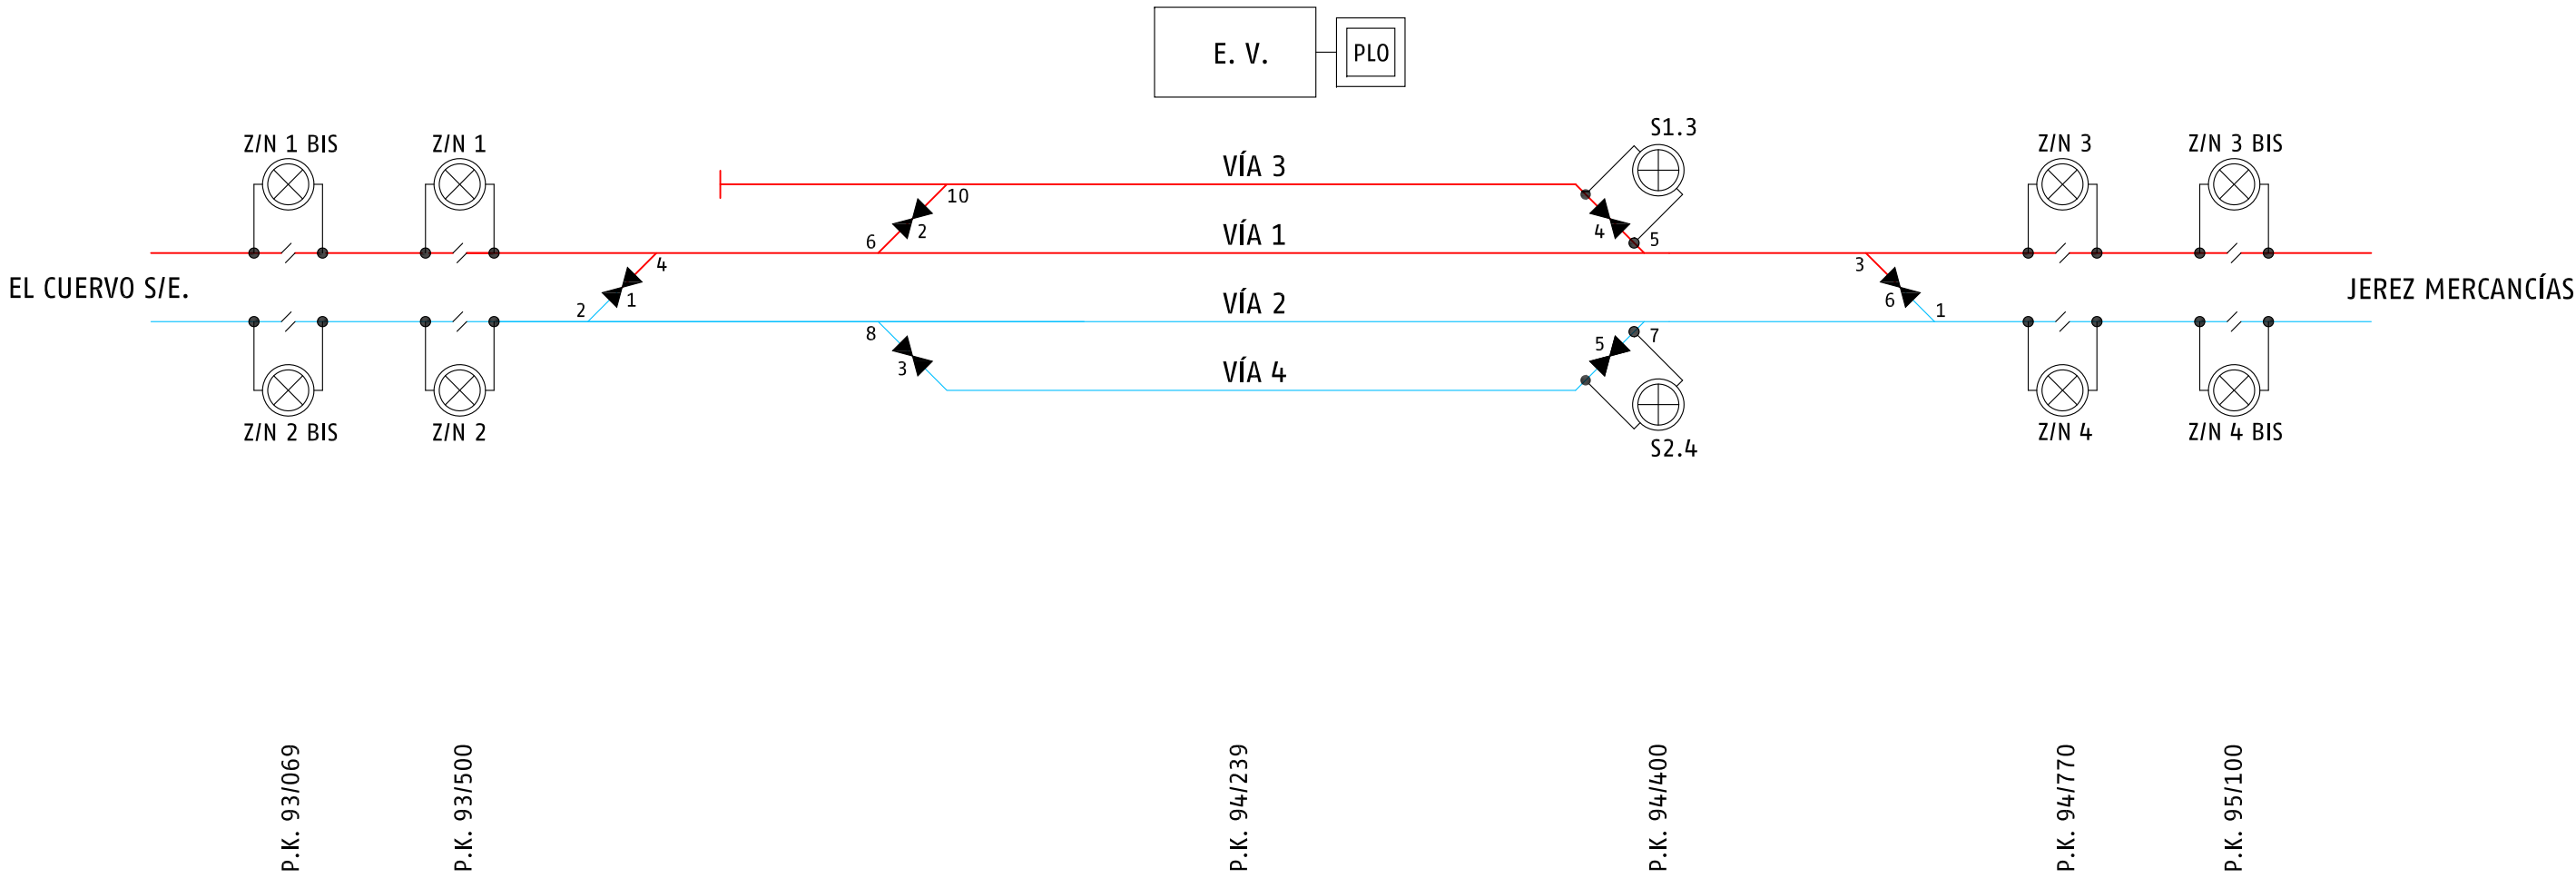

SUBDIRECCIÓN DE OPERACIONES
RED CONVENCIONAL SUR
JEFATURA DE ÁREA DE
MANTENIMIENTO DE SEVILLA

Dibujado por:	J.G.J.
Aprobado por:	Jose Angel Gomez Flores
Firma	
Fecha:	19 FEBRERO 2025

ESQUEMA ELÉCTRICO L.A.C.
P.E. 24 LÍNEA DE SEVILLA A CÁDIZ
AEROPUERTO DE JEREZ

Plano nº	1 de 1
Sustituye a:	Hoja 11 de 21 de 09/04/21
Hoja nº	11 de 21