


AGUJAS	P.K.
2	97/402
4	97/496
6	97/617
8	97/620
10	97/711
12	97/725
14	97/792
16	97/835
18	97/855

SEÑALES	P.K.
E4	96/967
E2	97/115
E3	99/493
E1	99/494

AGUJAS	P.K.
9	98/583
7	98/755
5	98/849
3	99/129
1	99/223

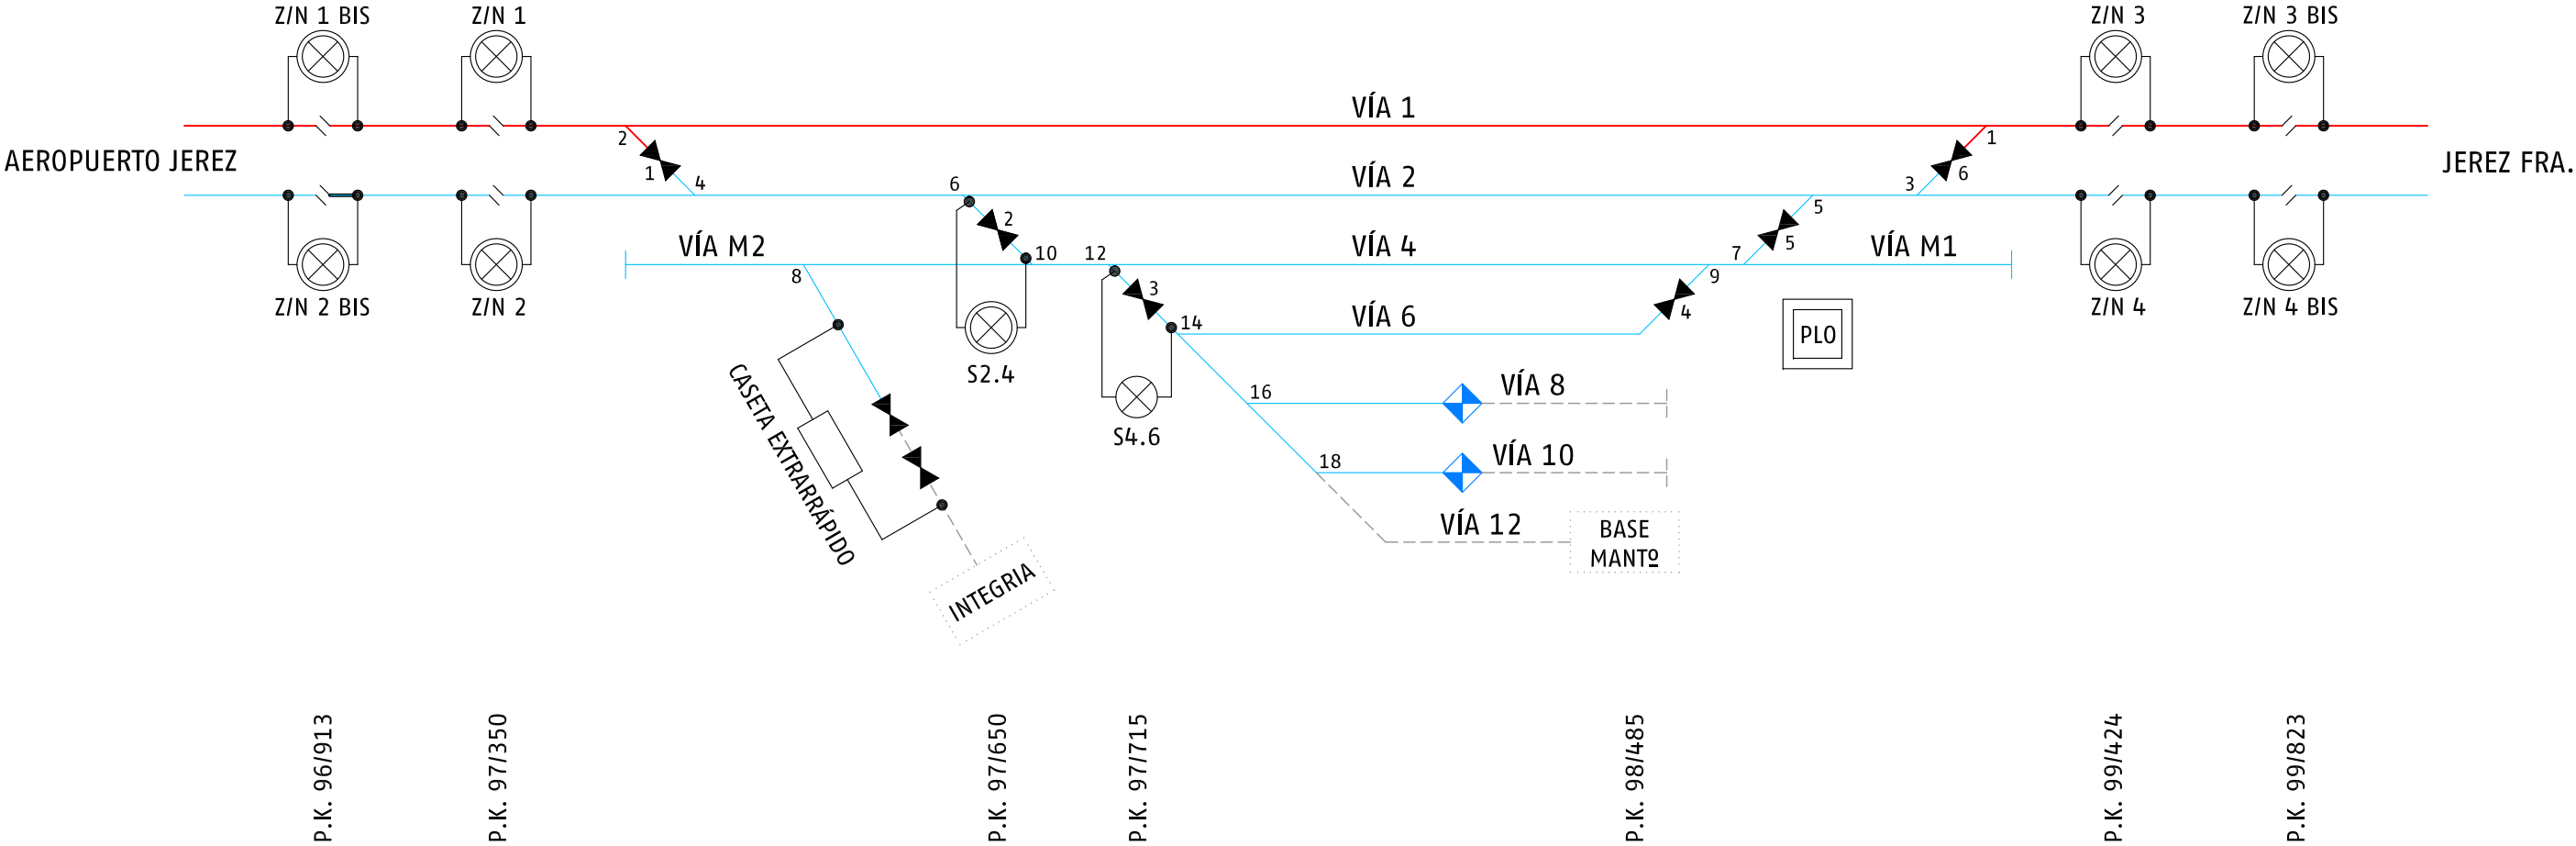

NOTA: Esquema que no cumple con la NAE 112