


AGUJAS	P.K.
2	123/221
4	123/383
6	123/405
8	123/568
10	123/674
12	123/674
14	124/201

SEÑALES	P.K.
E2	122/919
E4	122/919
E1	124/907
E3	124/907

AGUJAS	P.K.
1	124/500
3	124/500
5	124/399

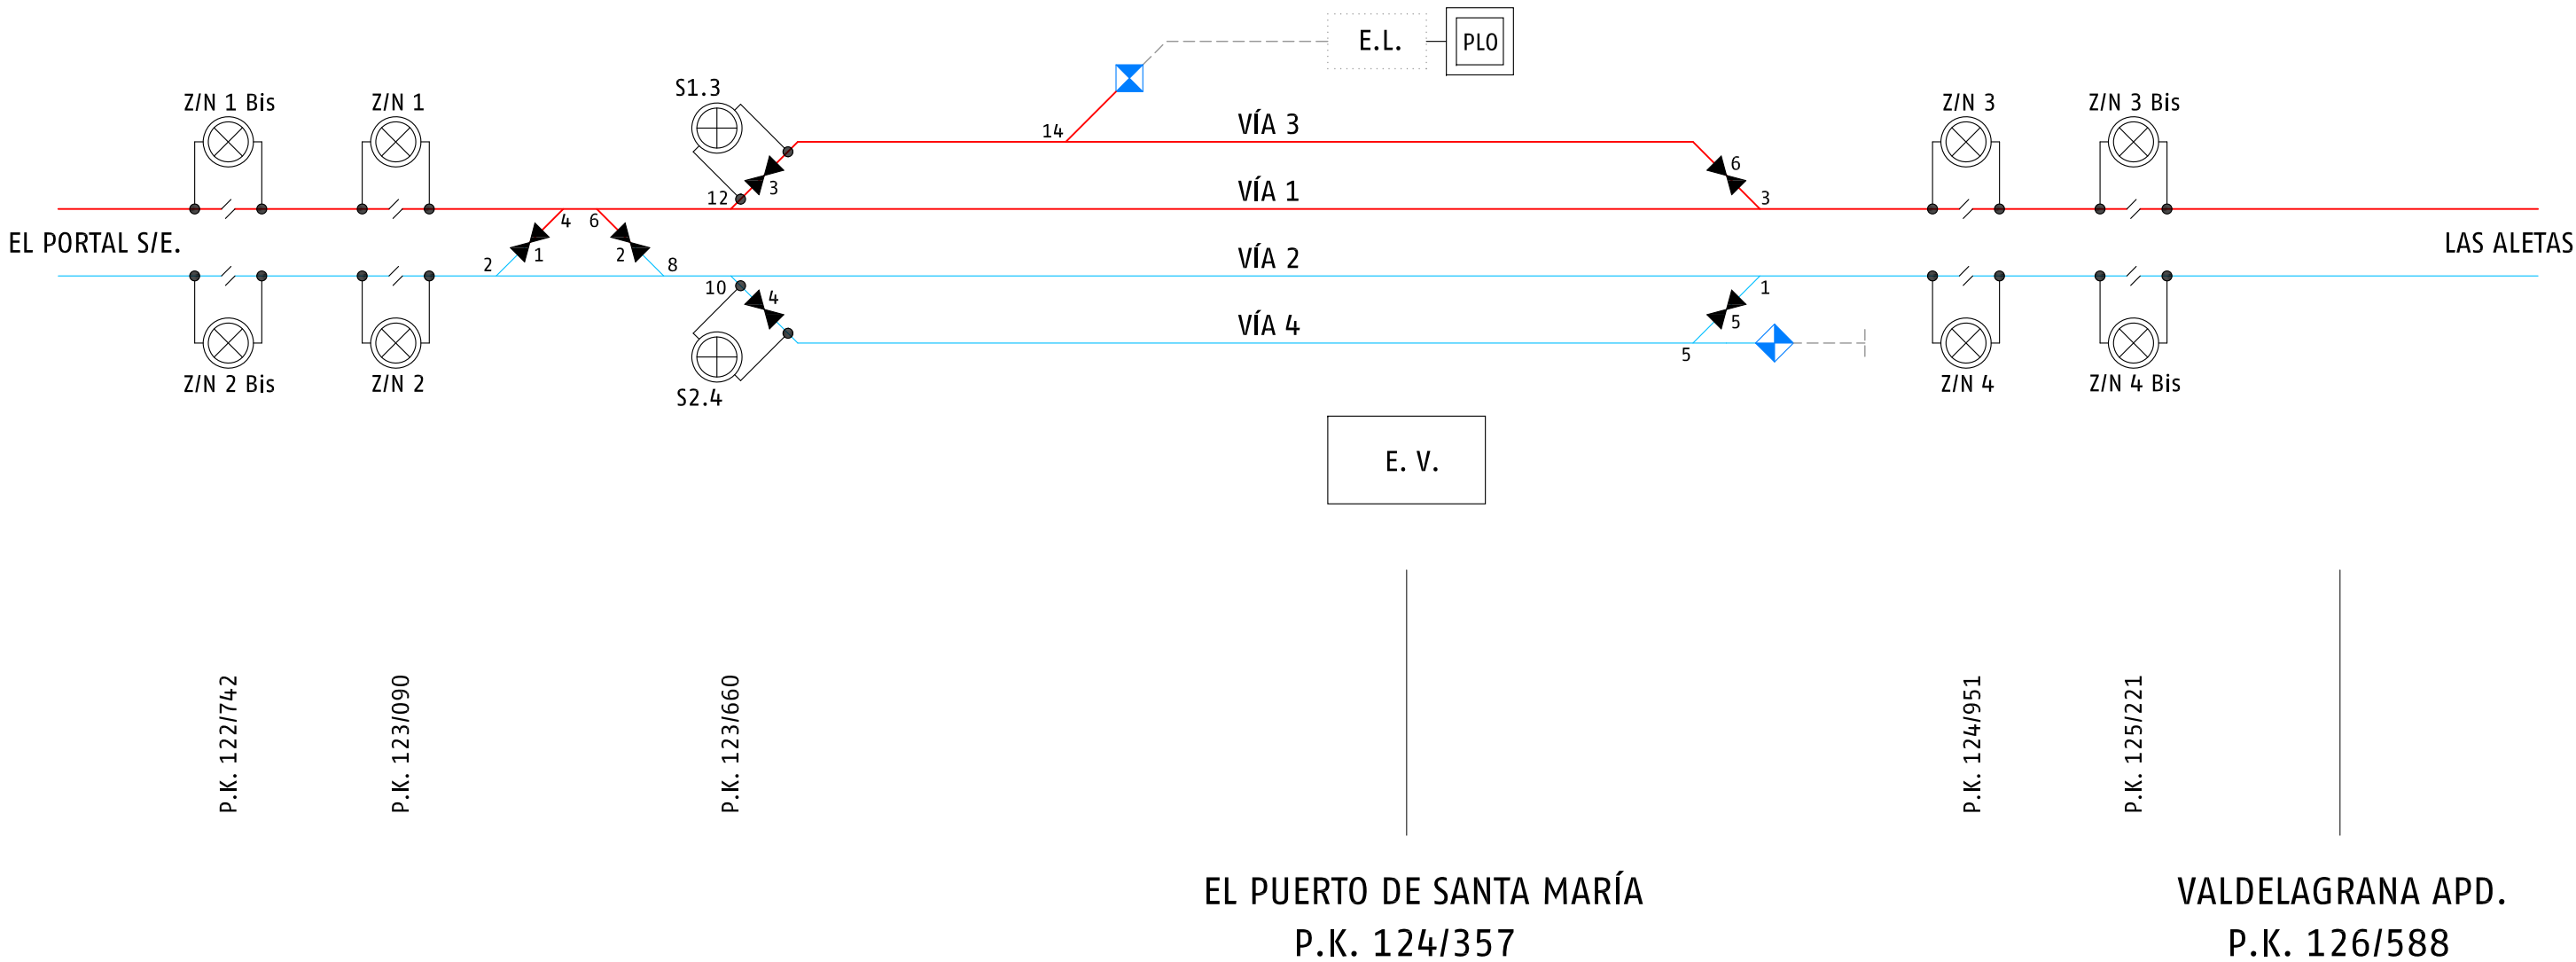

SUBDIRECCIÓN DE OPERACIONES
RED CONVENCIONAL SUR

JEFATURA DE ÁREA DE
MANTENIMIENTO DE SEVILLA

Dibujado por: J.G.J.
Aprobado por: Jose Angel Gomez Flores
Firma: [Firma]
Fecha: 19 FEBRERO 2025

ESQUEMA ELÉCTRICO L.A.C.
P.E. 24 LÍNEA DE SEVILLA A CÁDIZ
EL PUERTO DE SANTA MARÍA

Plano nº 1 de 1
Sustituye a: Hoja 15 de 21 de 12/04/21
Hoja nº 15 de 21