


AGUJAS	P.K.
2	131/456
4	131/528
6	131/540
8	131/626
10	131/696

SEÑALES	P.K.
E2	131/192
E4	131/192
E1	132/556
E3	132/556
E9	1/095
E5	2/239
E7	2/267

AGUJAS	P.K.
11	131/965
9	132/036
7	132/093
5	132/187
3	132/210
1	132/282

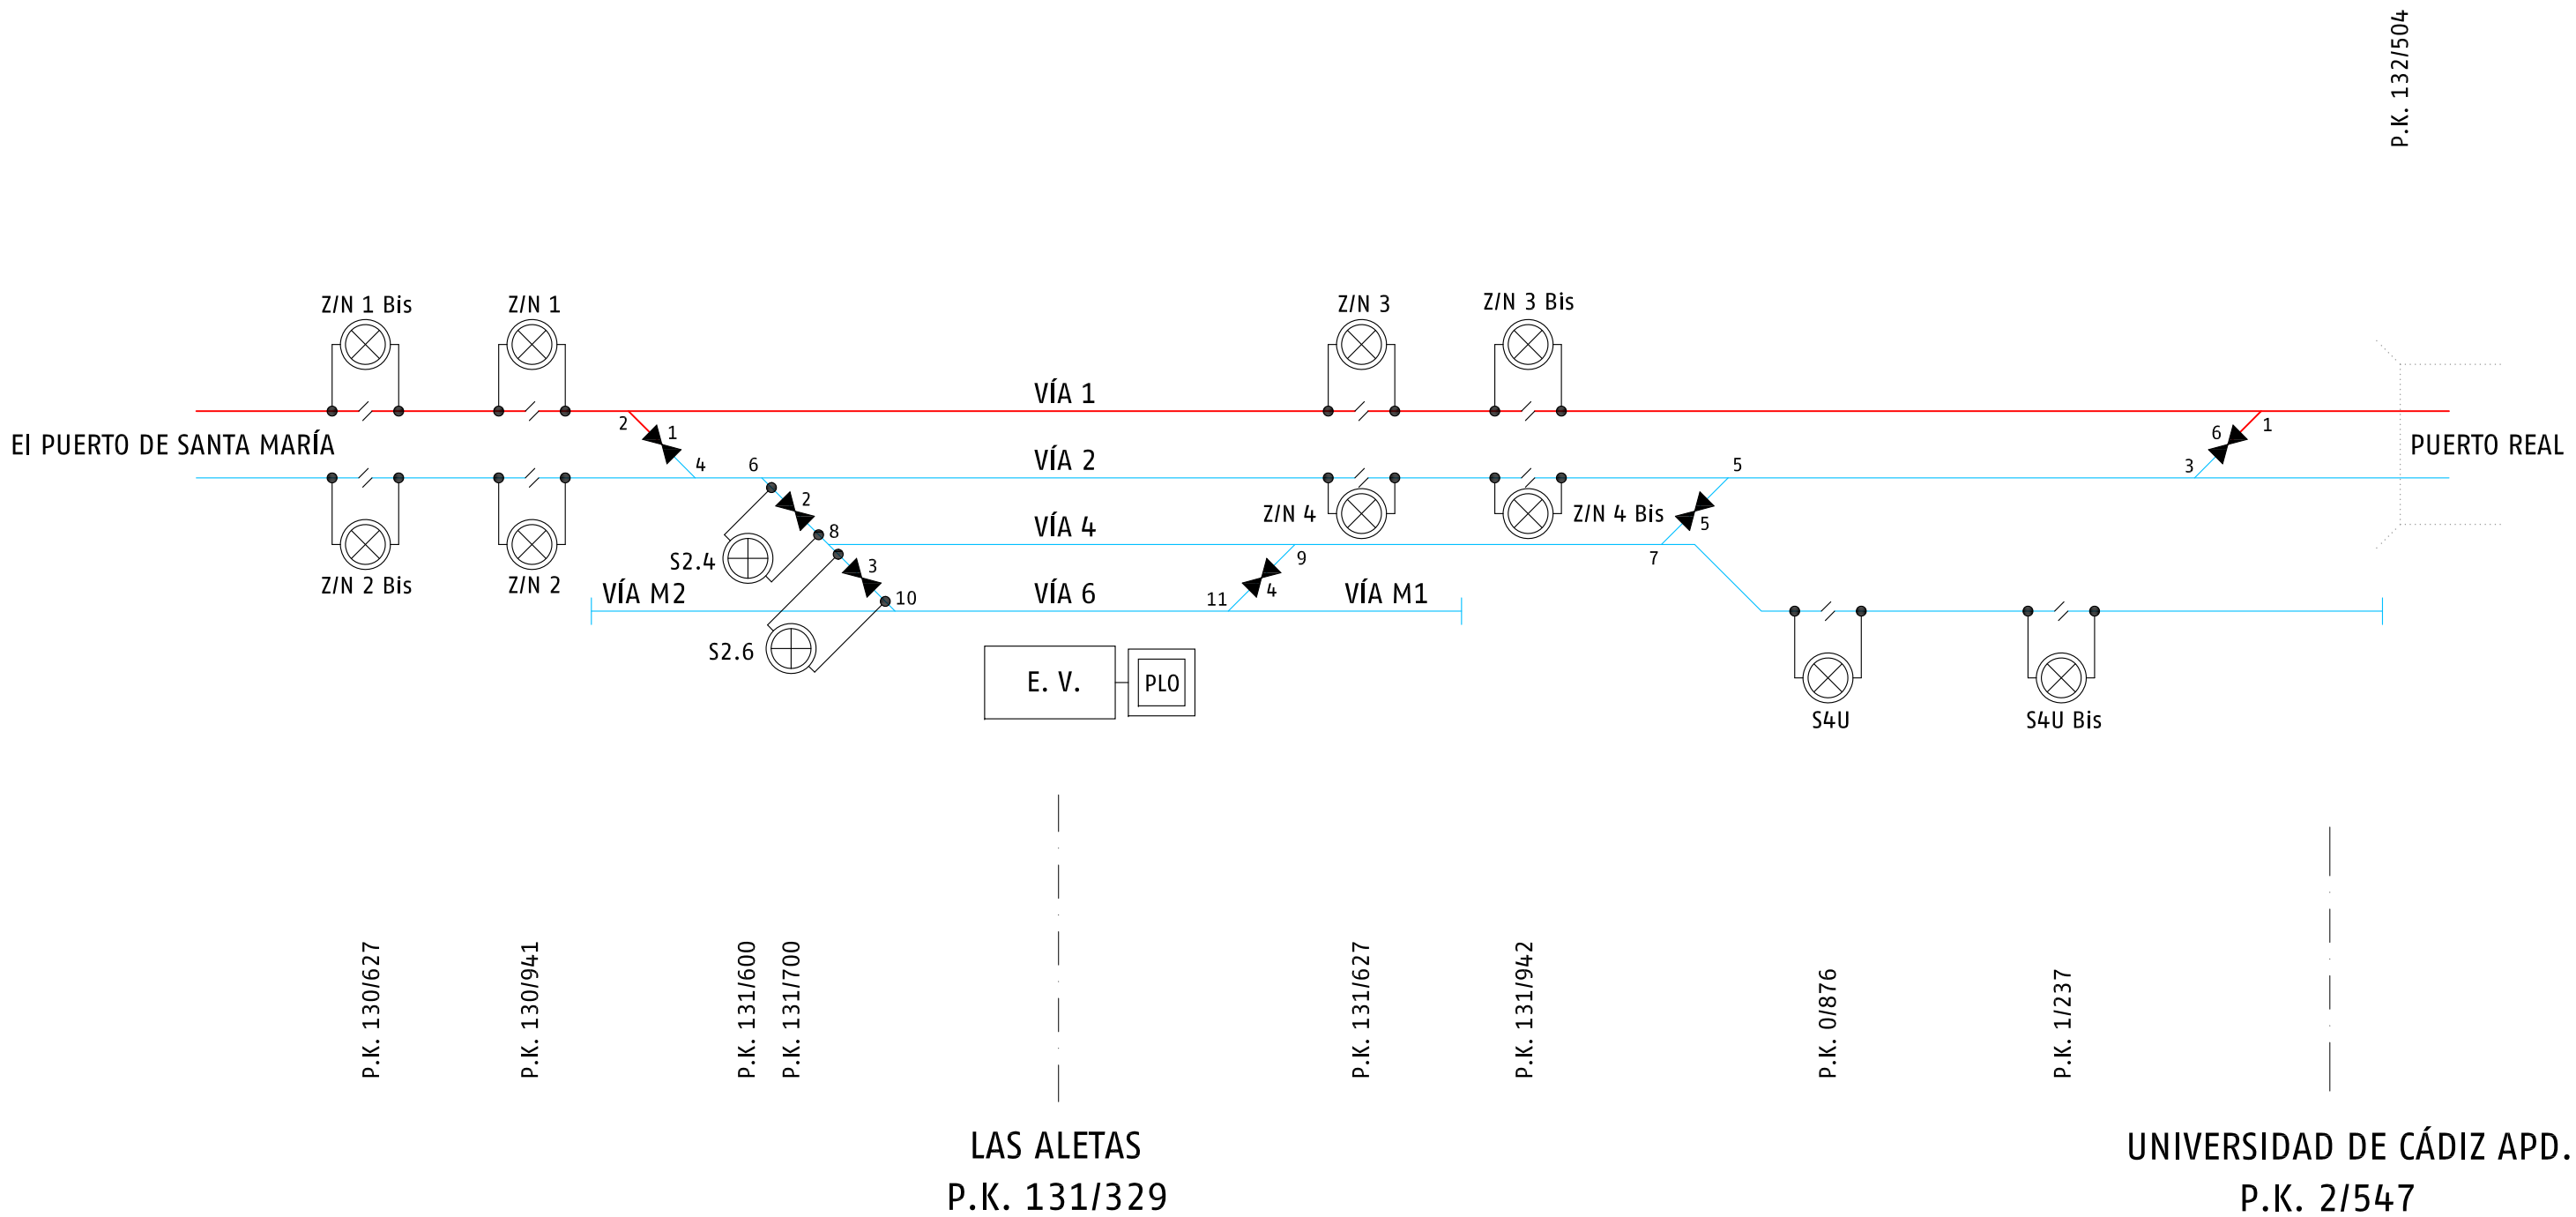

NOTA: Esquema que no cumple con la NAE 112