


AGUJAS	P.K.
2	153/577

SEÑALES	P.K.
E2	153/302
E4	153/302
E1	154/401
E3	154/401

AGUJAS	P.K.
3	154/061
1	154/133

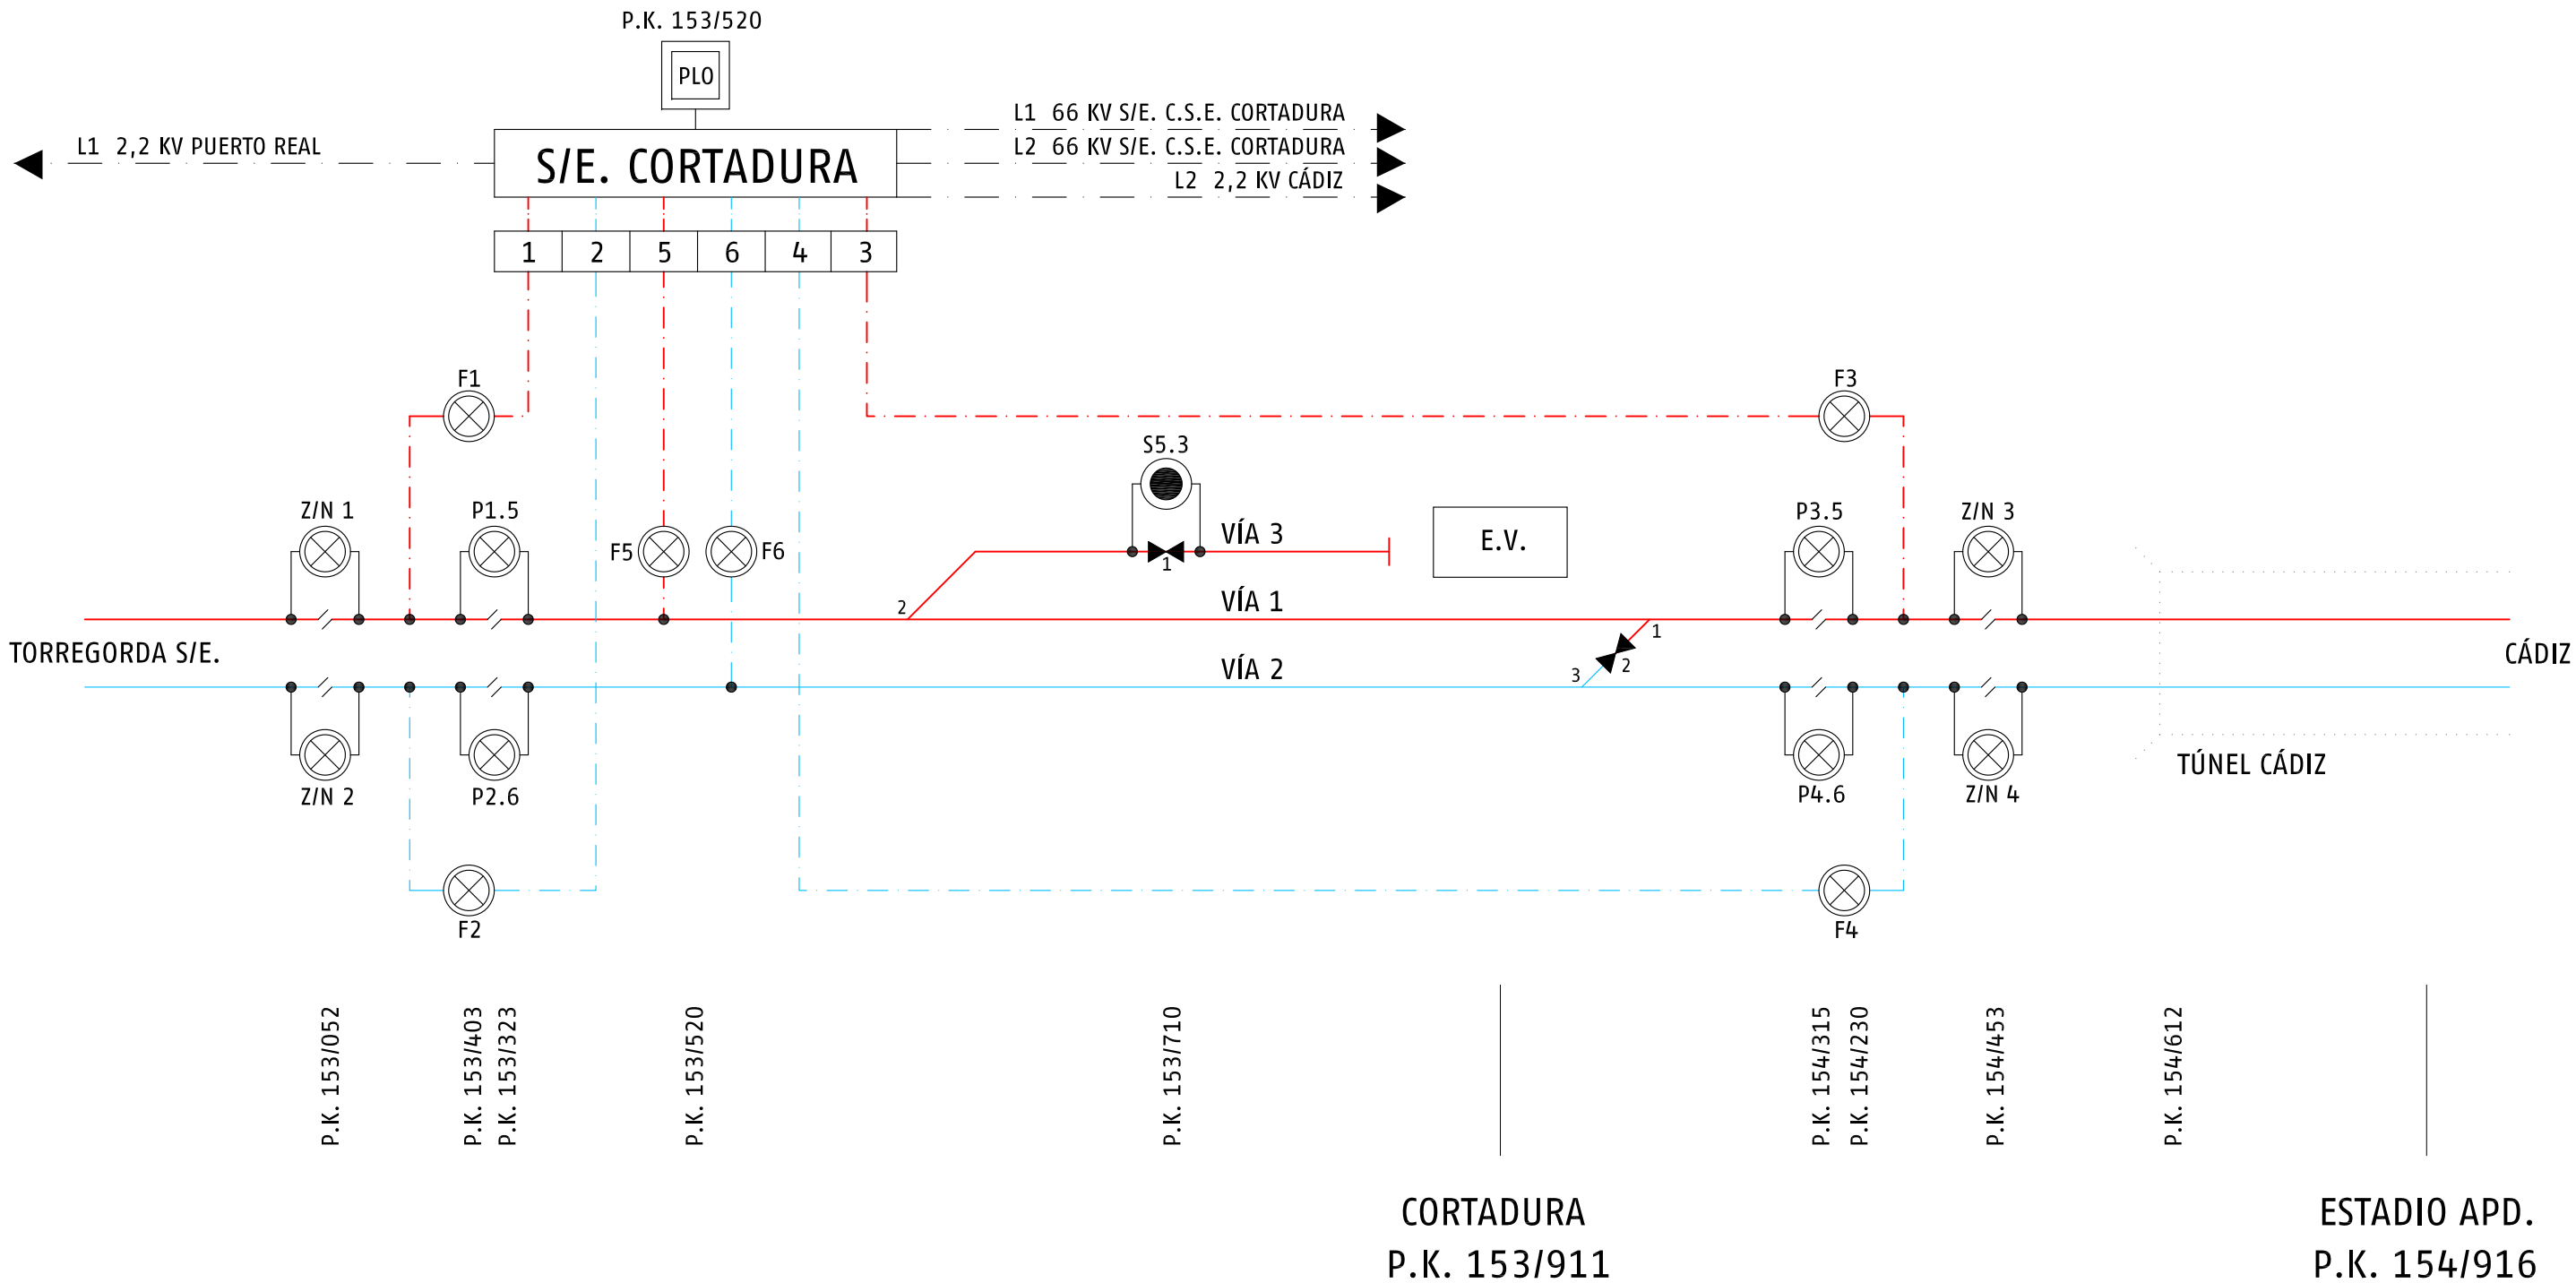

NOTA: Esquema que no cumple con la NAE 112



SUBDIRECCIÓN DE OPERACIONES
RED CONVENCIONAL SUR
JEFATURA DE ÁREA DE
MANTENIMIENTO DE SEVILLA

Dibujado por:	J.G.J.
Aprobado por:	Jose Angel Gomez Flores
Firma	
Fecha:	19 FEBRERO 2025

ESQUEMA ELÉCTRICO L.A.C.
P.E. 24 LÍNEA DE SEVILLA A CÁDIZ
CORTADURA

Plano nº	1 de 1
Sustituye a:	Hoja 20 de 21 de 20/04/21
Hoja nº	20 de 21