AGUJAS	P.K.
2	157/322
4	157/556
6	157/566
8	157/611
10	157/653
12	157/697
14	157/746
16	157/823
18	158/082

SEÑALES	P.K.
E2	156/961
E4	156/962

AGUJAS	P.K.
1	157/232
3	157/485
5	157/530
7	157/602
9	157/607
11	157/655
13	157/739
15	157/817
17	157/794

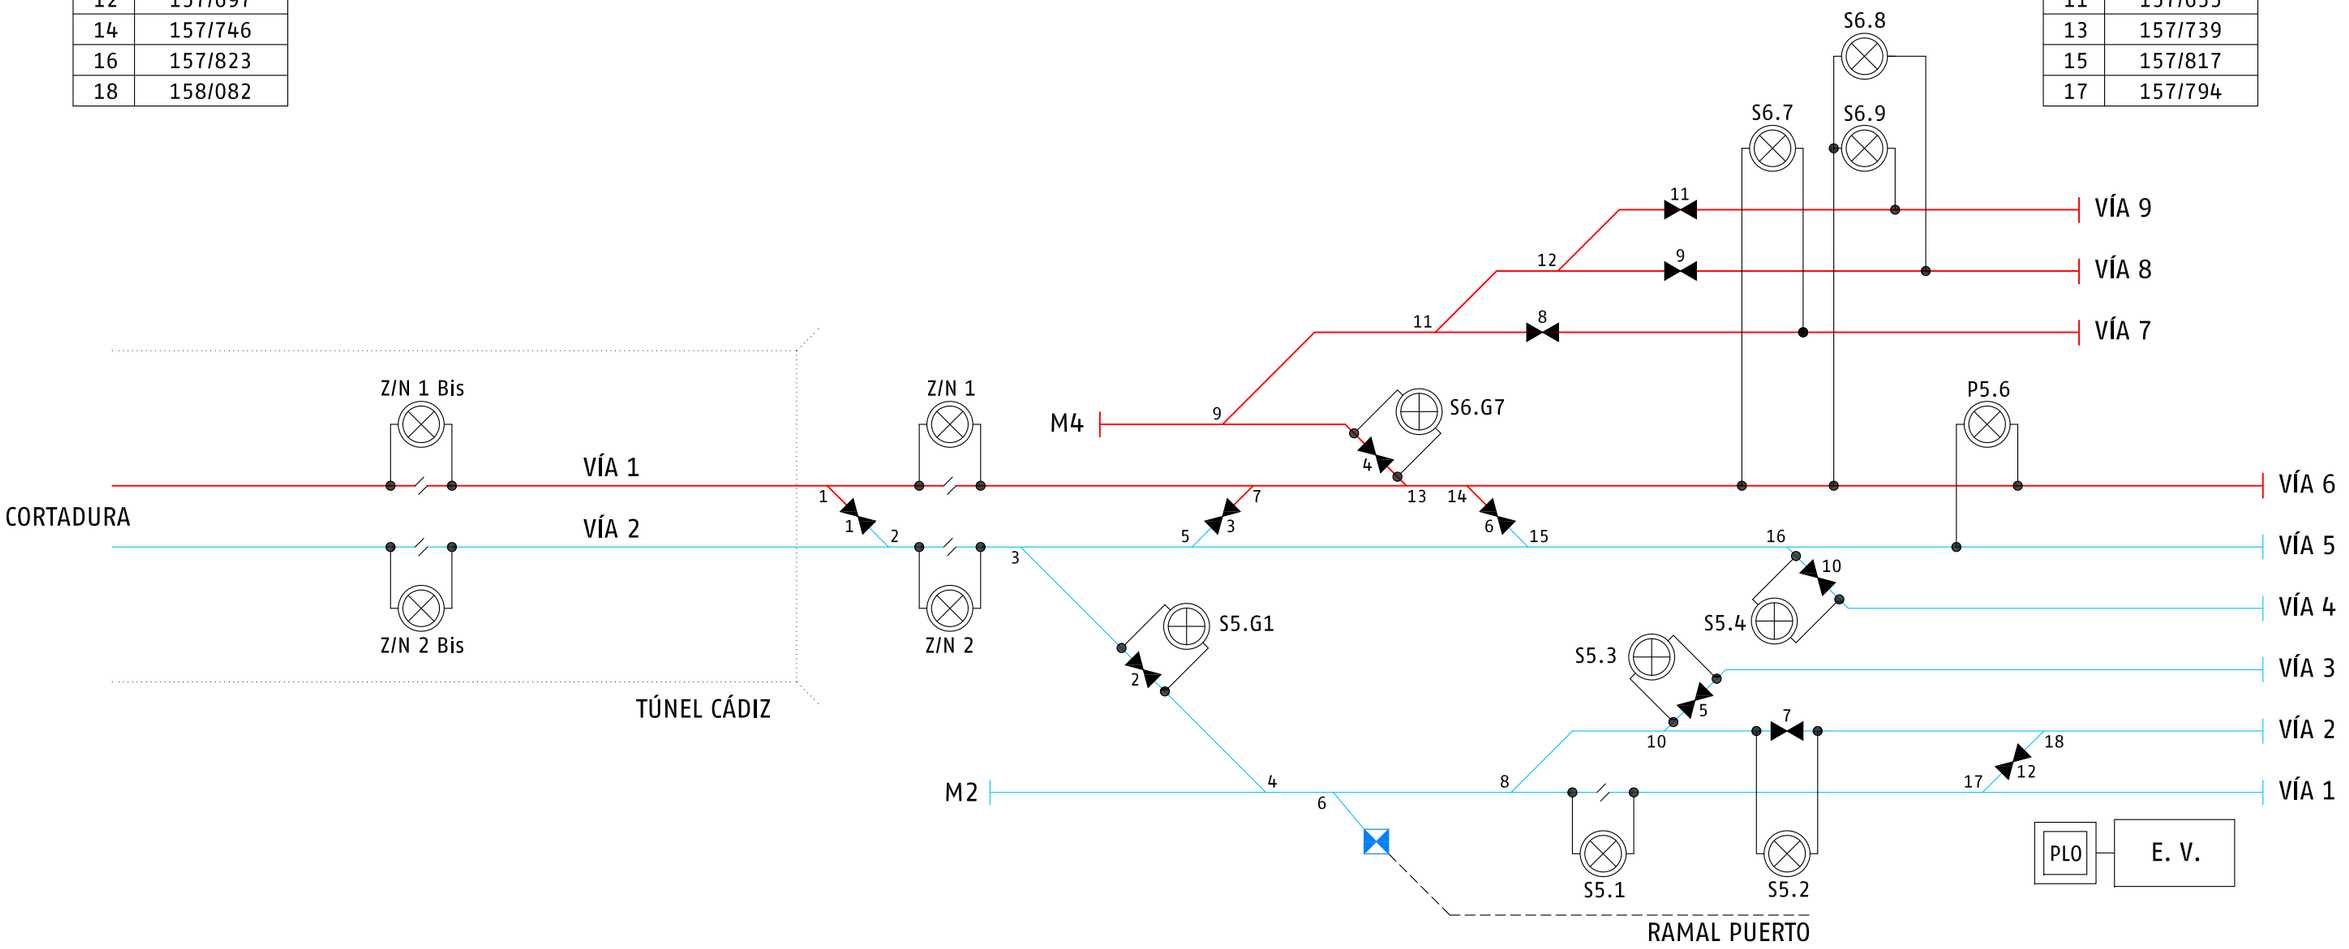

adif	SUBDIRECCIÓN DE OPERACIONES RED CONVENCIONAL SUR JEFATURA DE ÁREA DE MANTENIMIENTO DE SEVILLA	Dibujado por: J.G.J. Aprobado por: Jose Angel Gomez Flores Firma Fecha: 19 FEBRERO 2025	ESQUEMA ELÉCTRICO L.A.C. P.E. 24 LÍNEA DE SEVILLA A CÁDIZ CÁDIZ	Plano nº 1 de 1 Sustituye a: Hoja 21 de 21 de 20/04/21 Hoja nº 21 de 21