


AGUJAS	P.K.
2	12/475

SEÑALES	P.K.
E1	13/371
E2	12/450

AGUJAS	P.K.
1	13/101

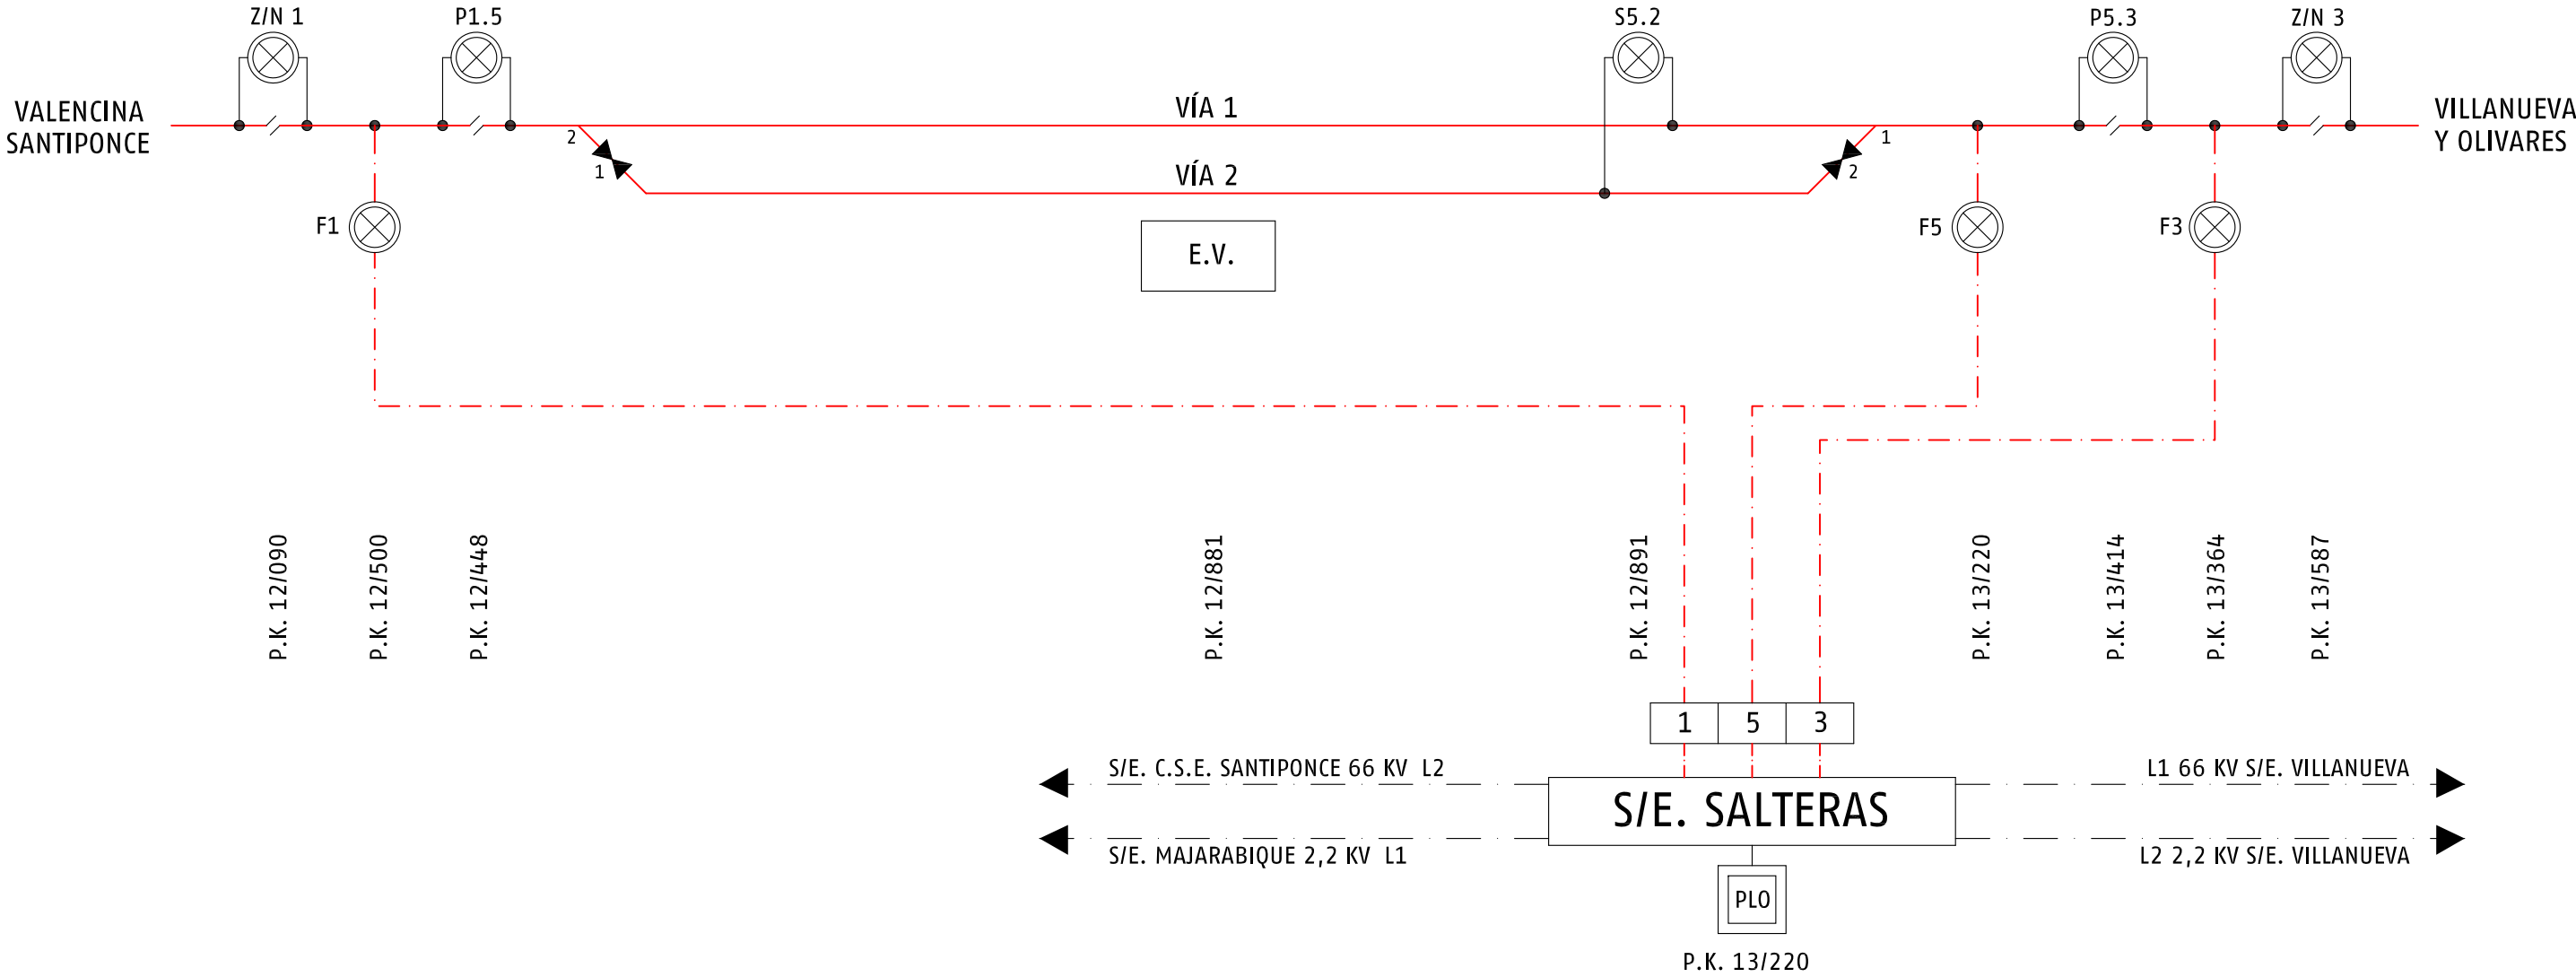

NOTA: Esquema que no cumple con la NAE 112



SUBDIRECCIÓN DE OPERACIONES
RED CONVENCIONAL SUR
JEFATURA DE ÁREA DE
MANTENIMIENTO DE SEVILLA

Dibujado por: J.G.J.
Aprobado por: Jose Angel Gomez Flores
Firma: Firmado digitalmente por Jose Angel Gomez Flores
Fecha: 2024.07.19 11:19:16 +02'00'
Fecha: 19-JULIO-2024

ESQUEMA ELÉCTRICO L.A.C.
P.E. 26 LÍNEA DE BIF. LOS NARANJOS A HUELVA
SALTERAS

Plano nº 1 de 1
Sustituye a: Hoja 5 de 17 de 13/05/15
Hoja nº 5 de 17