


AGUJAS	P.K.
2	35/323
4	35/377
6	35/424

SEÑALES	P.K.
E1	36/328
E2	35/040

AGUJAS	P.K.
1	36/052
3	35/906
5	35/858

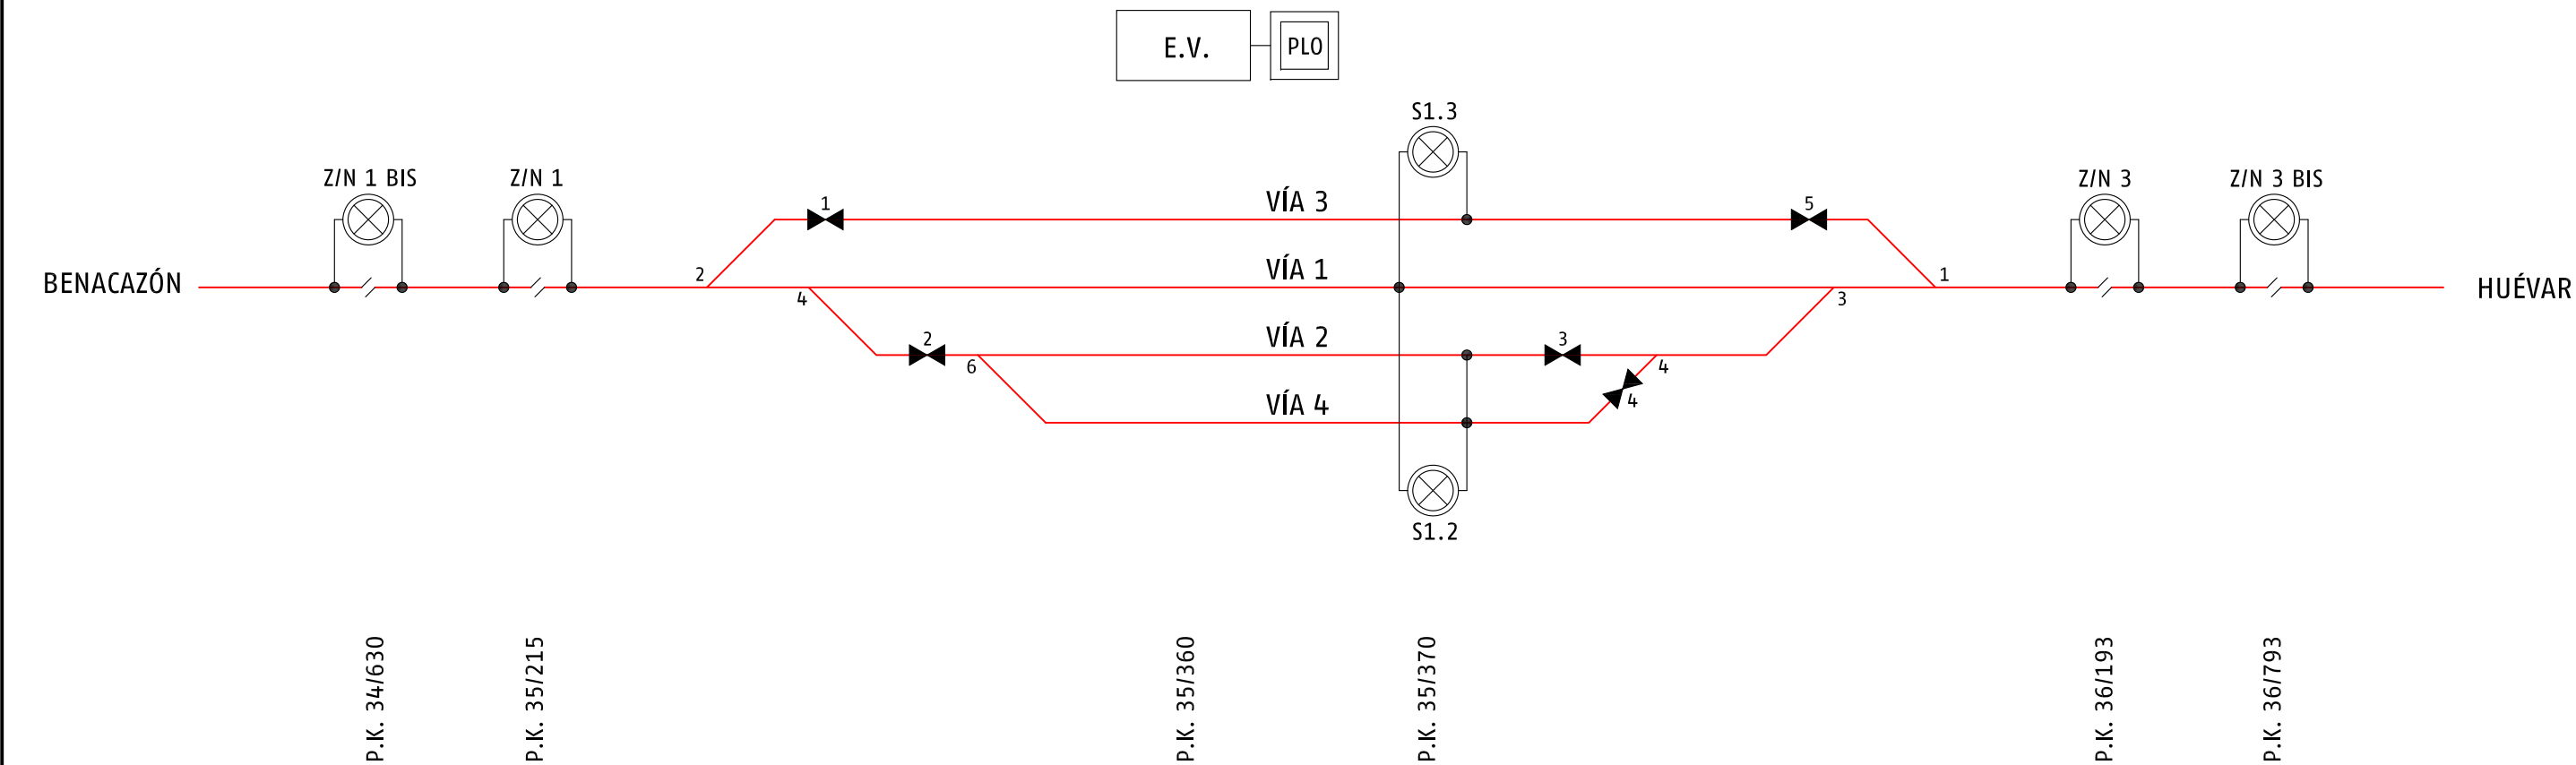

SUBDIRECCIÓN DE OPERACIONES
RED CONVENCIONAL SUR
JEFATURA DE ÁREA DE
MANTENIMIENTO DE SEVILLA

Dibujado por: J.G.J.
Aprobado por: Jose Angel Gomez Flores
Firma: Firmado digitalmente por Jose Angel Gomez Flores
Fecha: 2024.07.19 11:19:16 +02'00'
Fecha: 19-JULIO-2024

ESQUEMA ELÉCTRICO L.A.C.
P.E. 26 LÍNEA DE BIF. LOS NARANJOS A HUELVA
AZNALCÁZAR-PILAS

Plano nº 1 de 1
Sustituye a: Hoja 8 de 17 de 13/05/15
Hoja nº 8 de 17