


AGUJAS	P.K.
2	45/550
4	46/630

SEÑALES	P.K.
E1	46/275
E2	45/338

AGUJAS	P.K.
1	46/220

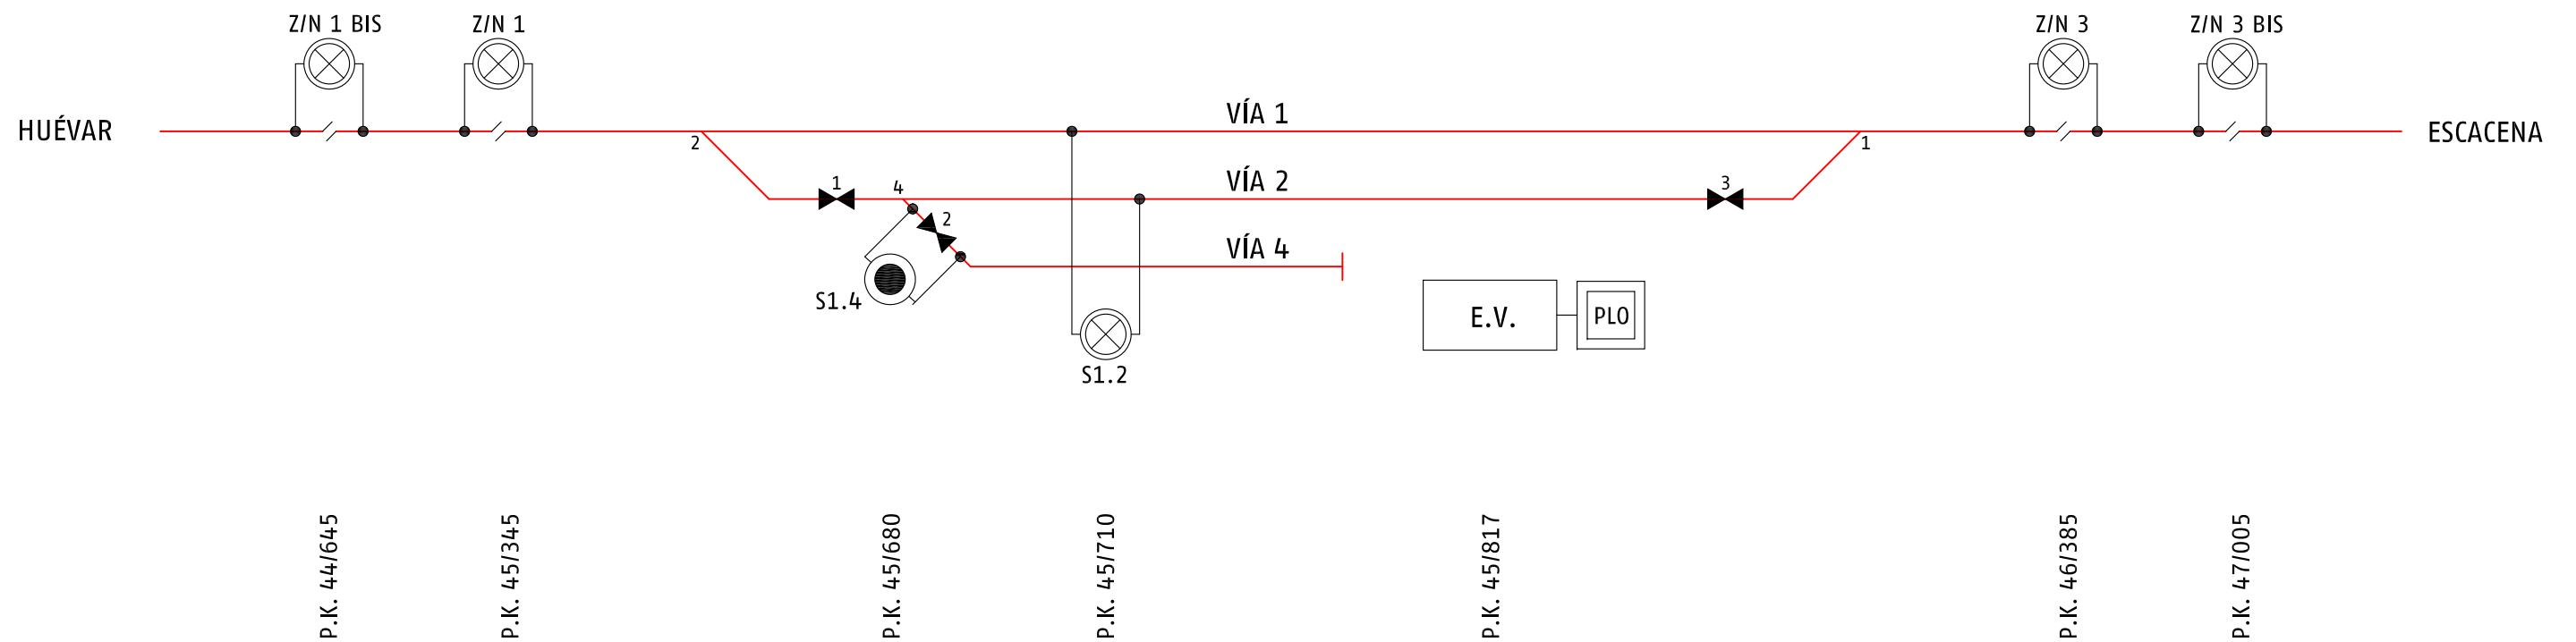

SUBDIRECCIÓN DE OPERACIONES
RED CONVENCIONAL SUR
JEFATURA DE ÁREA DE
MANTENIMIENTO DE SEVILLA

Dibujado por: J.G.J.
Aprobado por: Jose Angel Gomez Flores
Firma: Firmado digitalmente por Jose Angel Gomez Flores
Fecha: 2024.07.19 11:19:16 +02'00'
Fecha: 19-JULIO-2024

ESQUEMA ELÉCTRICO L.A.C.
P.E. 26 LÍNEA DE BIF. LOS NARANJOS A HUELVA
CARRIÓN DE LOS CÉSPEDES

Plano nº 1 de 1
Sustituye a: Hoja 10 de 17 de 13/05/15
Hoja nº 10 de 17