


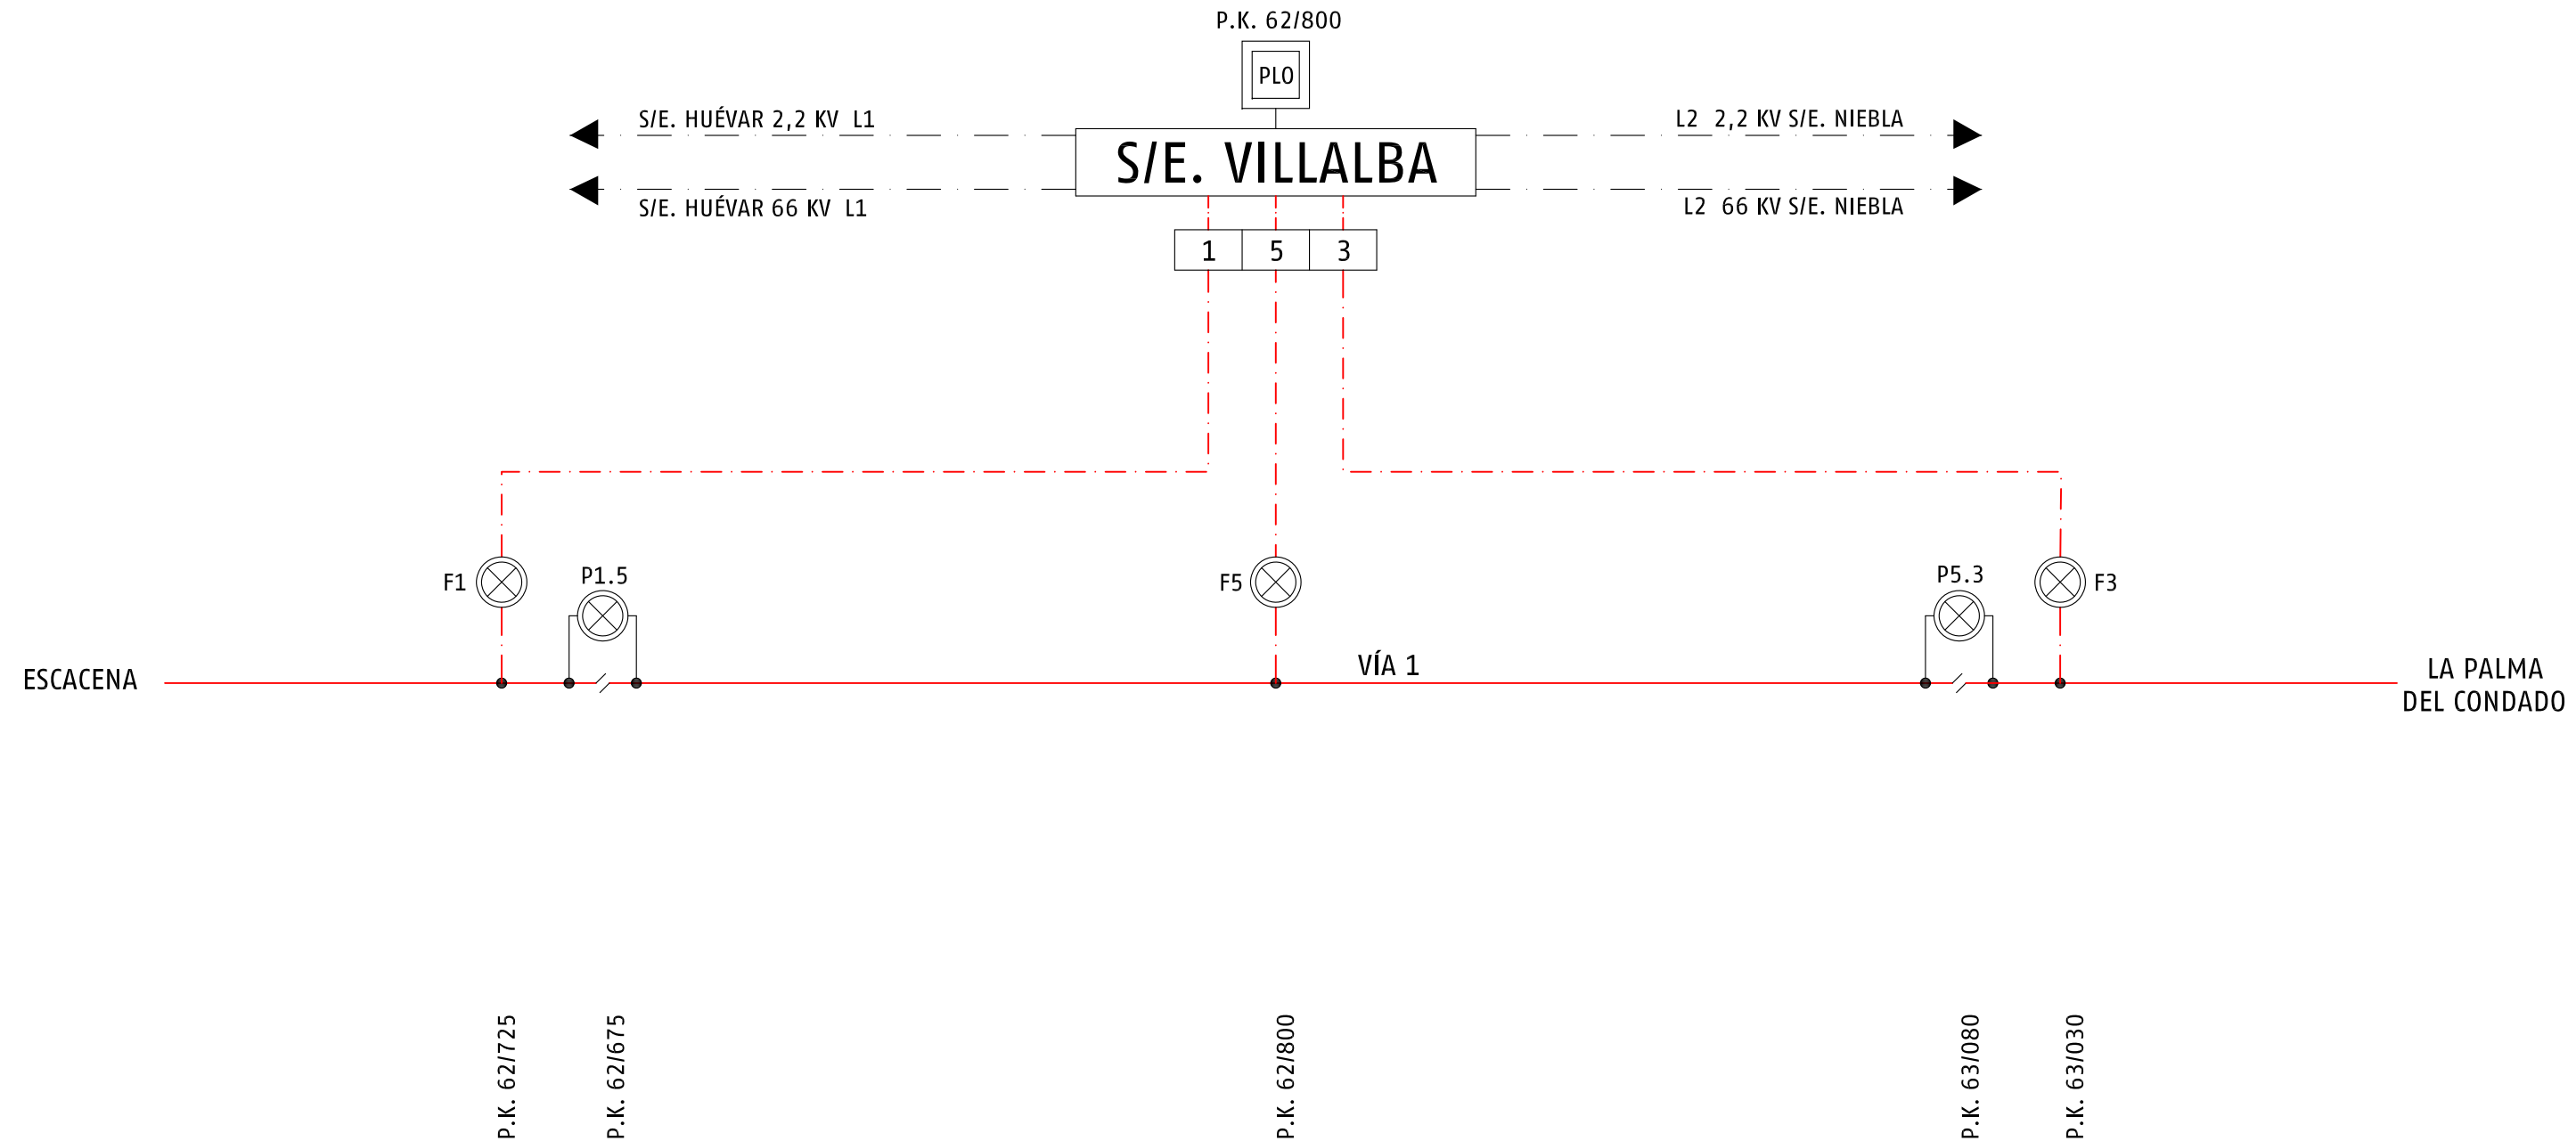

NOTA: Esquema que no cumple con la NAE 112

	SUBDIRECCIÓN DE OPERACIONES RED CONVENCIONAL SUR JEFATURA DE ÁREA DE MANTENIMIENTO DE SEVILLA	Dibujado por: J.G.J.	ESQUEMA ELÉCTRICO L.A.C. P.E. 26 LÍNEA DE BIF. LOS NARANJOS A HUELVA VILLALBA	Plano nº 1 de 1
		Aprobado por: Jose Angel Gomez Flores Firma		Sustituye a: Hoja 12 de 17 de 13/05/15
		Fecha: 19-JULIO-2024		Hoja nº 12 de 17