


AGUJAS	P.K.
2	68/216
4	68/355
6	68/369
8	68/445

SEÑALES	P.K.
E1	69/098
E2	68/155

AGUJAS	P.K.
1	68/933
3	68/897
5	68/883

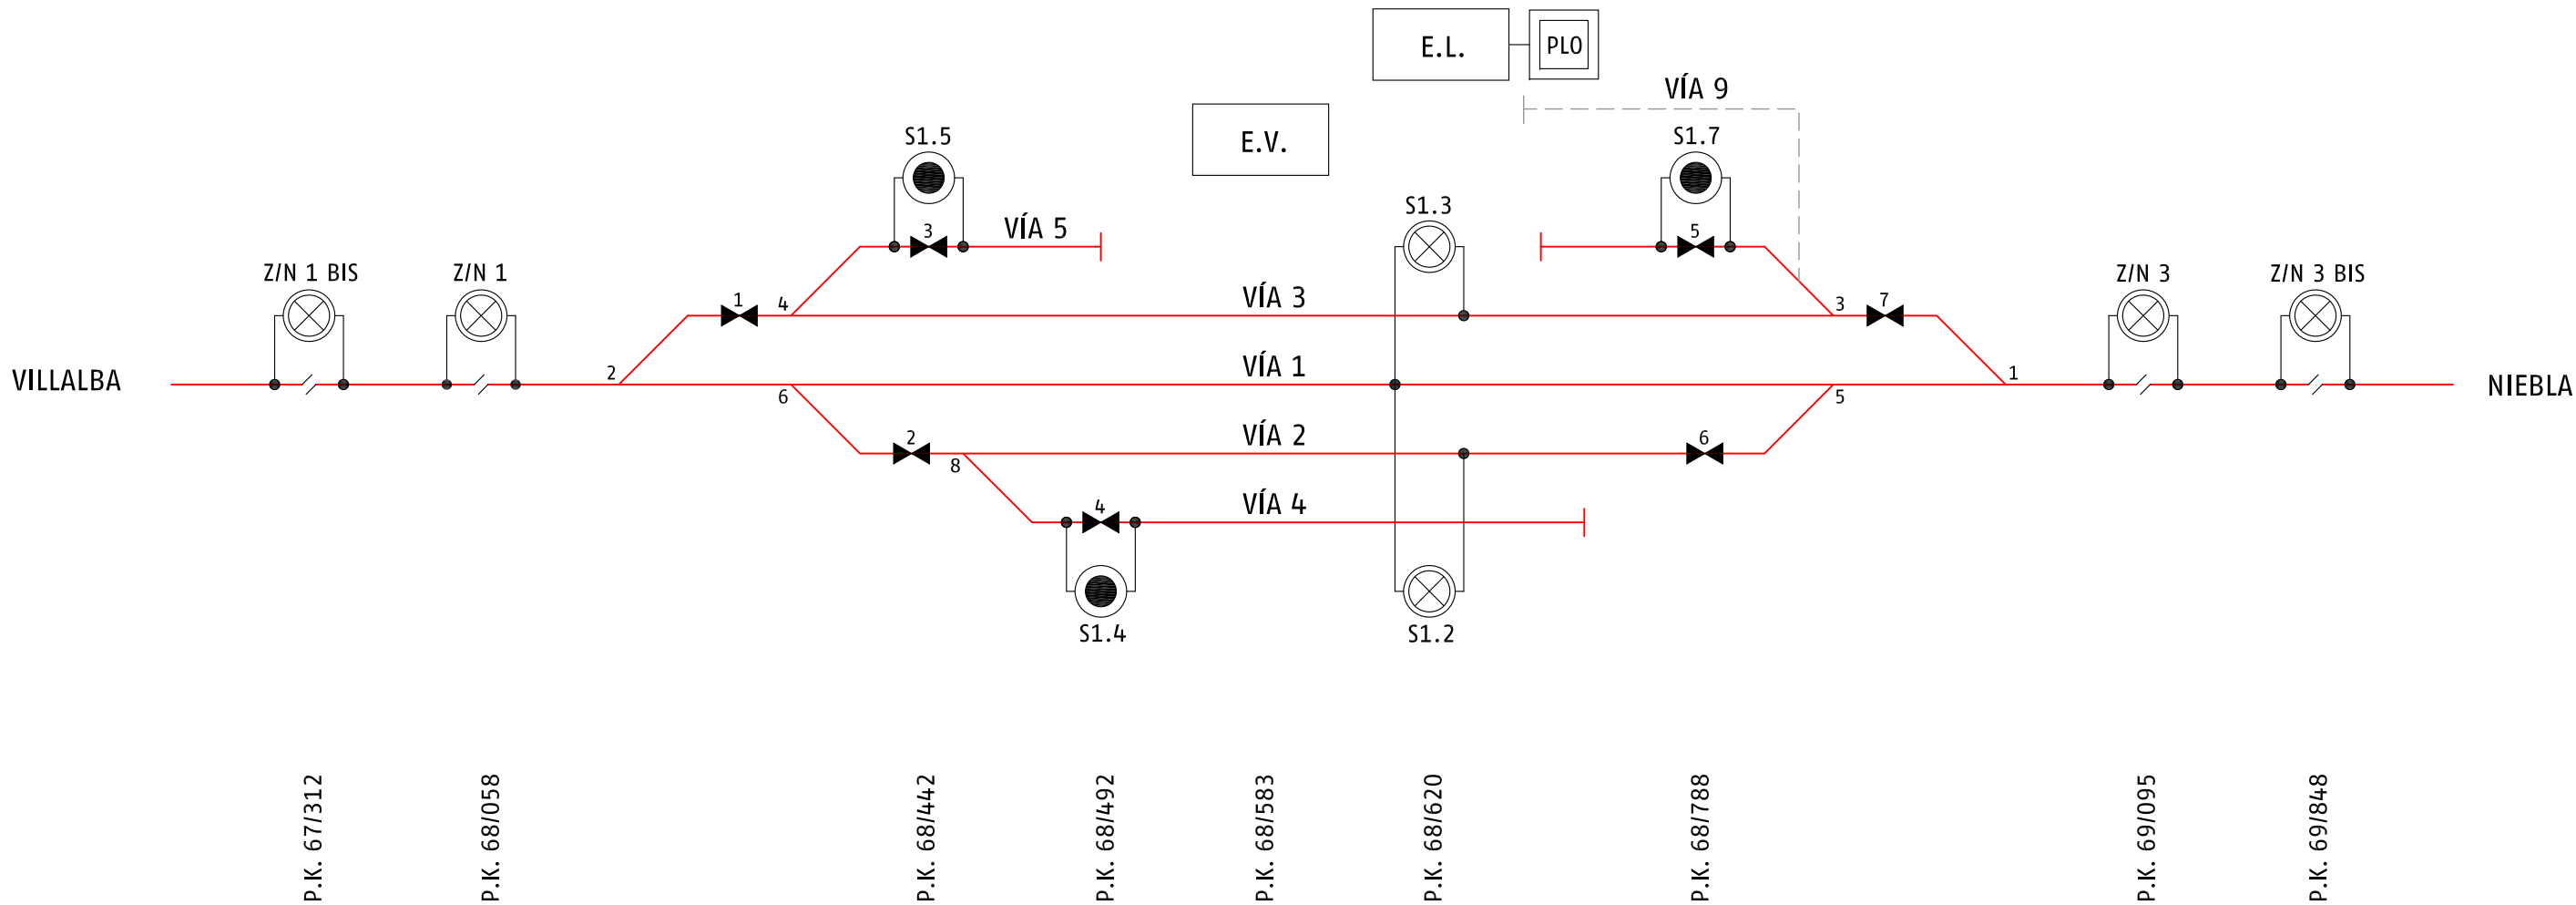

SUBDIRECCIÓN DE OPERACIONES
RED CONVENCIONAL SUR

JEFATURA DE ÁREA DE
MANTENIMIENTO DE SEVILLA

Dibujado por: J.G.J.
Aprobado por: Jose Angel Gomez Flores
Firma: Firmado digitalmente por Jose Angel Gomez Flores
Fecha: 2024.07.19 11:19:16 +02'00'
Fecha: 19-JULIO-2024

ESQUEMA ELÉCTRICO L.A.C.
P.E. 26 LÍNEA DE BIF. LOS NARANJOS A HUELVA
LA PALMA DEL CONDADO

Plano nº 1 de 1
Sustituye a: Hoja 13 de 17 de 13/05/15
Hoja nº 13 de 17