


AGUJAS	P.K.
2	96/310
4	96/358

SEÑALES	P.K.
E1	97/435
E2	96/255

AGUJAS	P.K.
1	97/375
3	97/230
5	96/949

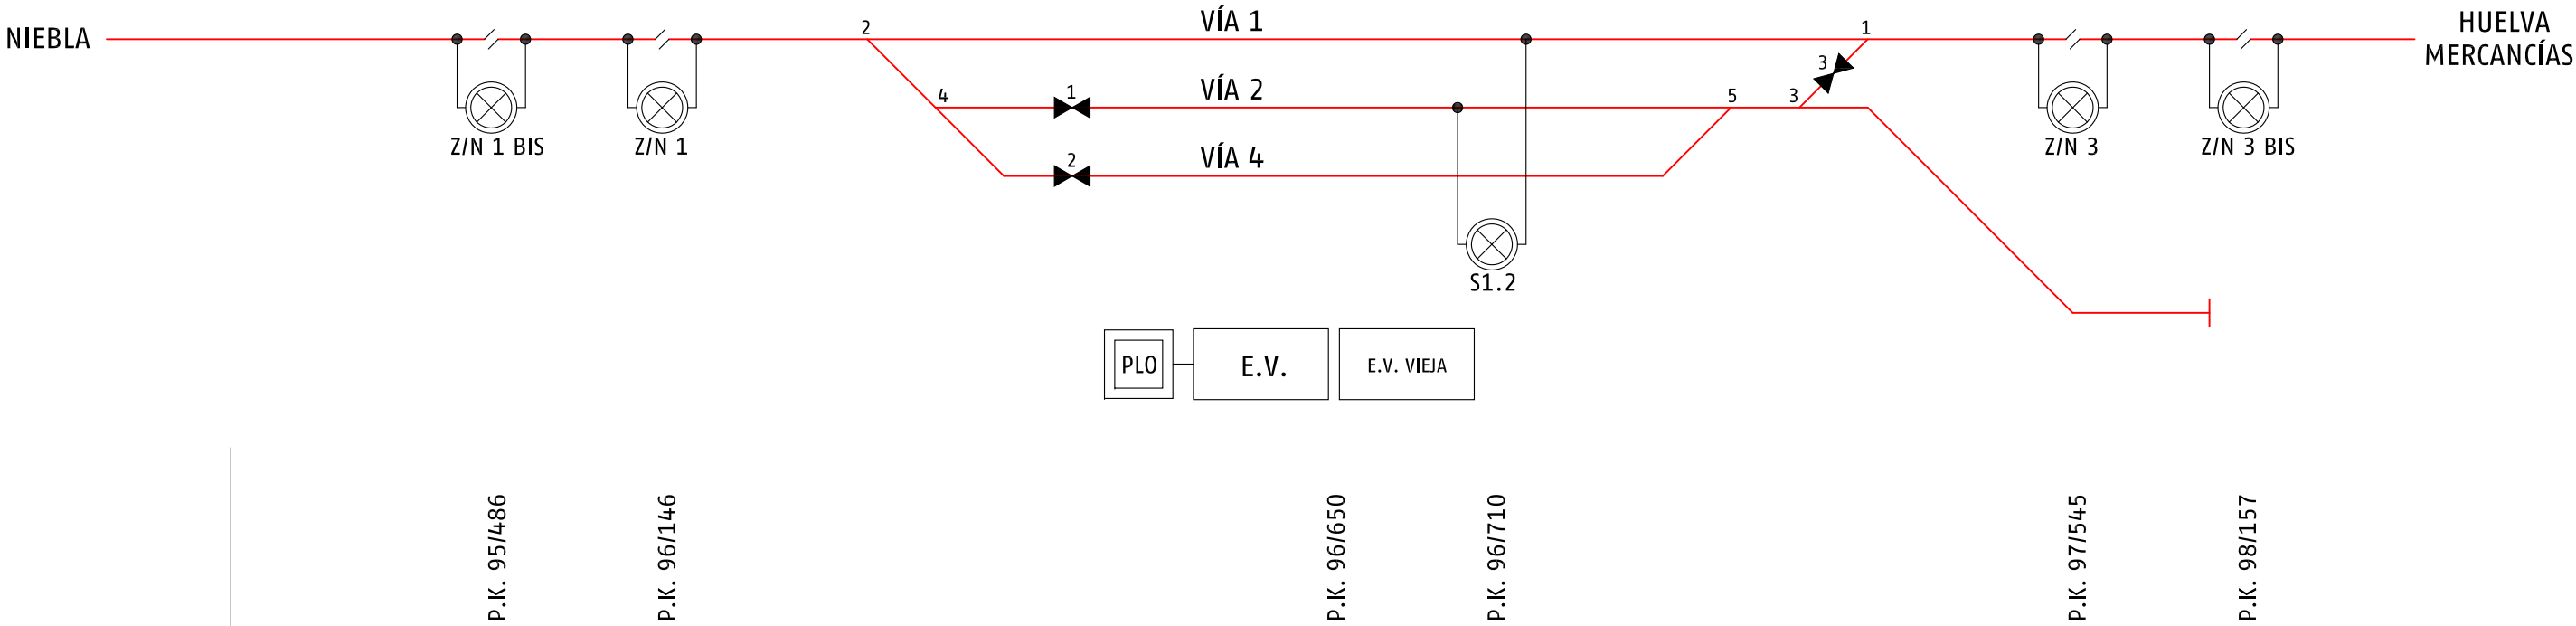

SAN JUAN DEL PUERTO APD.
P.K. 96/100



SUBDIRECCIÓN DE OPERACIONES
RED CONVENCIONAL SUR
JEFATURA DE ÁREA DE
MANTENIMIENTO DE SEVILLA

Dibujado por: J.G.J.
Aprobado por: Jose Angel Gomez Flores
Firma: Firmado digitalmente por Jose Angel Gomez Flores
Fecha: 2024.07.19 11:19:16 +02'00'
Fecha: 19-JULIO-2024

ESQUEMA ELÉCTRICO L.A.C.
P.E. 26 LÍNEA DE BIF. LOS NARANJOS A HUELVA
SAN JUAN DEL PUERTO

Plano nº 1 de 1
Sustituye a: Hoja 15 de 17 de 13/05/15
Hoja nº 15 de 17