
AGUJAS	P.K.
2	78/479
4	78/833

SEÑALES	P.K.
E1	79/282
E2	78/424

AGUJAS	P.K.
1	79/213
3	79/168

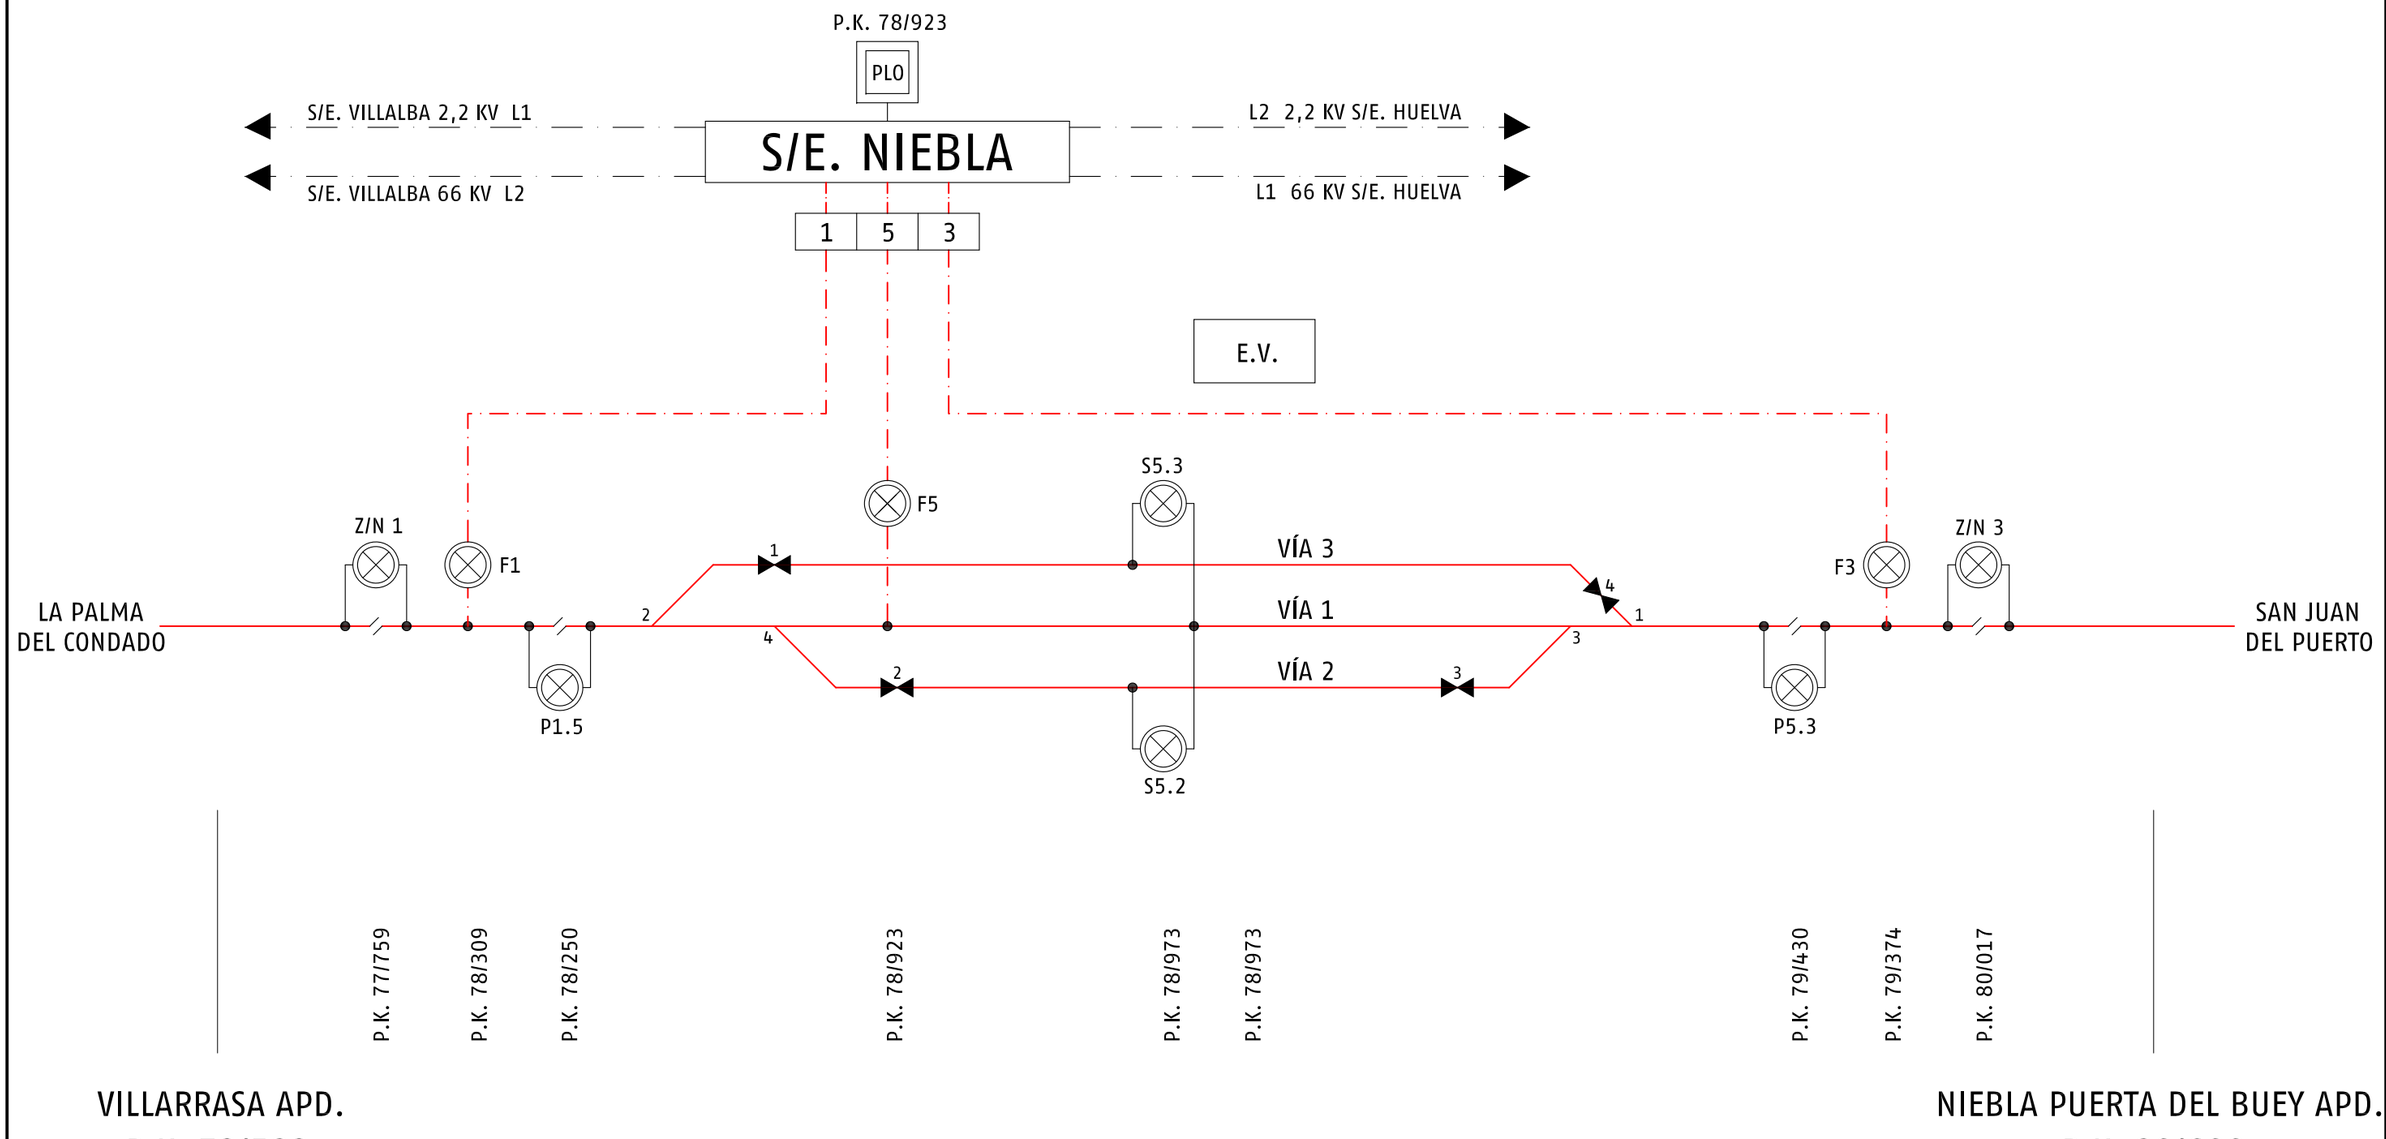

NOTA: Esquema que no cumple con la NAE 112

adif	SUBDIRECCIÓN DE OPERACIONES RED CONVENCIONAL SUR JEFATURA DE ÁREA DE MANTENIMIENTO DE SEVILLA	Dibujado por: J.G.J. Aprobado por: Jose Angel Gomez Flores (Firmado digitalmente por Jose Angel Gomez Flores Fecha: 2024.07.19 11:19:16 +02'00') Firma Fecha: 19-JULIO-2024	ESQUEMA ELÉCTRICO L.A.C. P.E. 26 LÍNEA DE BIF. LOS NARANJOS A HUELVA NIEBLA	Plano nº 1 de 1 Sustituye a: Hoja 14 de 17 de 20/06/16 Hoja nº 14 de 17