


CARTUJA

Km. 6.971

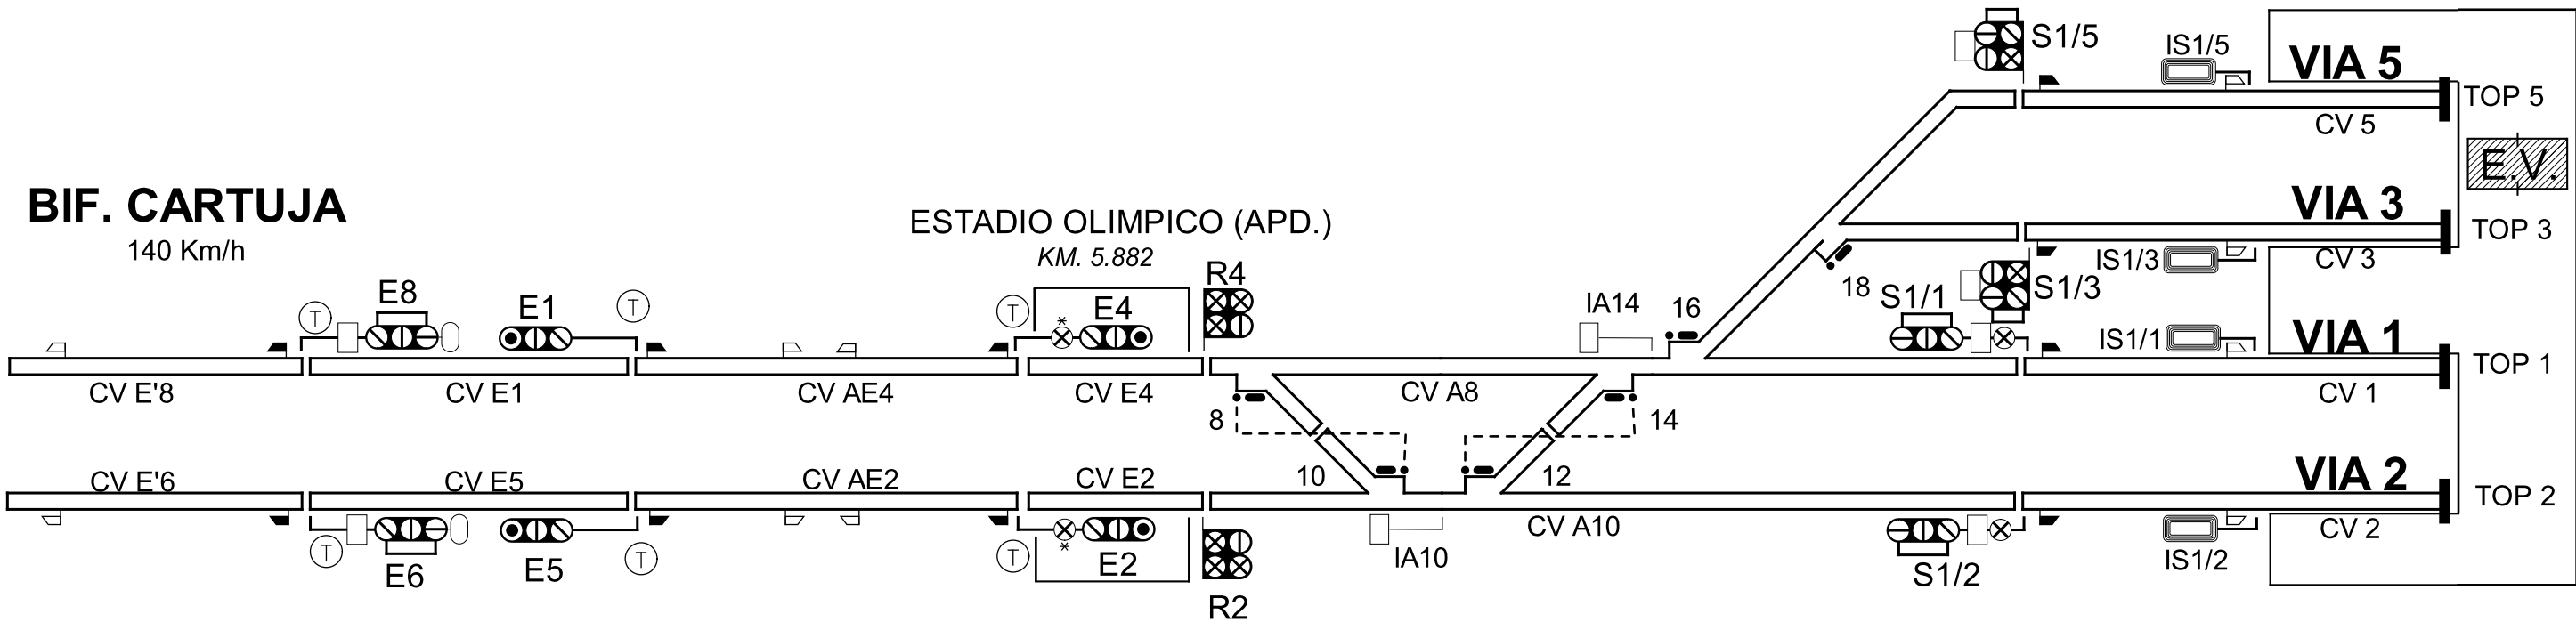

NOTA:

- EL CV E1 CORRESPONDE A LOS C.V. DE ENTRADA Y AGUJAS CV E8, CV A2 Y CV E1 DE BIF. CARTUJA.
- EL CV E5 CORRESPONDE A LOS C.V. DE ENTRADA Y AGUJAS CV E6, CV A4 Y CV E5 DE BIF. CARTUJA.
- LAS M.C. DE SALIDA SON INCOMPATIBLES CON BLOQUEO RECEPTOR Y VICEVERSA.

APARATOS							
Nº	Modelo	P.K. 1	VEL.	Nº	Modelo	P.K. 1	VEL.
8		6,046	50.0	TOP 5		6,972	
10		6,119	50.0	TOP 3		6,972	
12		6,127	50.0	TOP 1		6,972	
14		6,199	50.0	TOP 2		6,972	
16		6,347	50.0				
18		6,442	50.0				

SENALES			
Nombre	P.K.	Nombre	P.K.
E8	4,294	R2	6,026
E6	4,322	R4	6,026
E5	5,033	S1/2	6,213
E1	5,033	S1/1	6,418
E2	5,754	S1/5	6,516
E4	5,754	S1/3	6,516

ANDENES		
Nombre	P.K. INICIAL	P.K. FINAL
ANDEN	5,782	5,982
ANDEN	5,782	5,982
ANDEN	6,760	6,960
ANDEN	6,760	6,960
ANDEN	6,760	6,960

INDICADORAS DE SALIDA

IS1/1 6.740
IS1/2 6.740
IS1/3 6.740
IS1/5 6.740

INDICADORAS DE AGUJAS

IA10 6.126
IA14 6.335

ACTUALIZACIONES			NOMBRE	
VERSION	MOTIVO	FECHA	REVISADO	PEREZ
1	CONSIGNA	02/11/2011	ELABORADO	DAPI
			APROBADO	RINCON
			Nº: C-400-21-51050	
			HOJA: 1 de 1	
			NOMBRE DE FICHERO	
			CARTUJA 20111102	



DIRECCION ADJUNTA DE
PROG. DE INSTALACIONES

CARTUJA

Doble vía Cartuja