


SEÑALES - LORA DEL RIO			
Nombre	P.K.	Nombre	P.K.
5134	513,395	IA3	516,305
5133	513,415	R1	516,399
E2	515,472	E1	516,444
S1/4A	515,587	E5	516,675
S1/2	515,719	5178	518,003
S1/3-11	515,773	E'1	518,003
S1/1	515,777	S2	518,191
S1/4	515,890	M2	518,279
S1/6	515,890	M1	518,350
S2/6	516,162	E3	518,531
S2/4	516,162	E'3	521,025
S2/2	516,216		
S2/1	516,259		

APARATOS - LORA DEL RIO			
Nº	Modelo	P.K. 1	VEL.
2		515,510	50.0
4		515,620	50.0
6		515,713	30.0
10		515,820	30.0
7		516,249	30.0
5		516,299	30.0
3		516,319	30.0
1		516,393	30.0
A		518,244	30.0
B		518,330	30.0

LORA DEL RIO

LORA DEL RIO - L400_ALCAZAR S.J.-CADIZ - Km 516,073

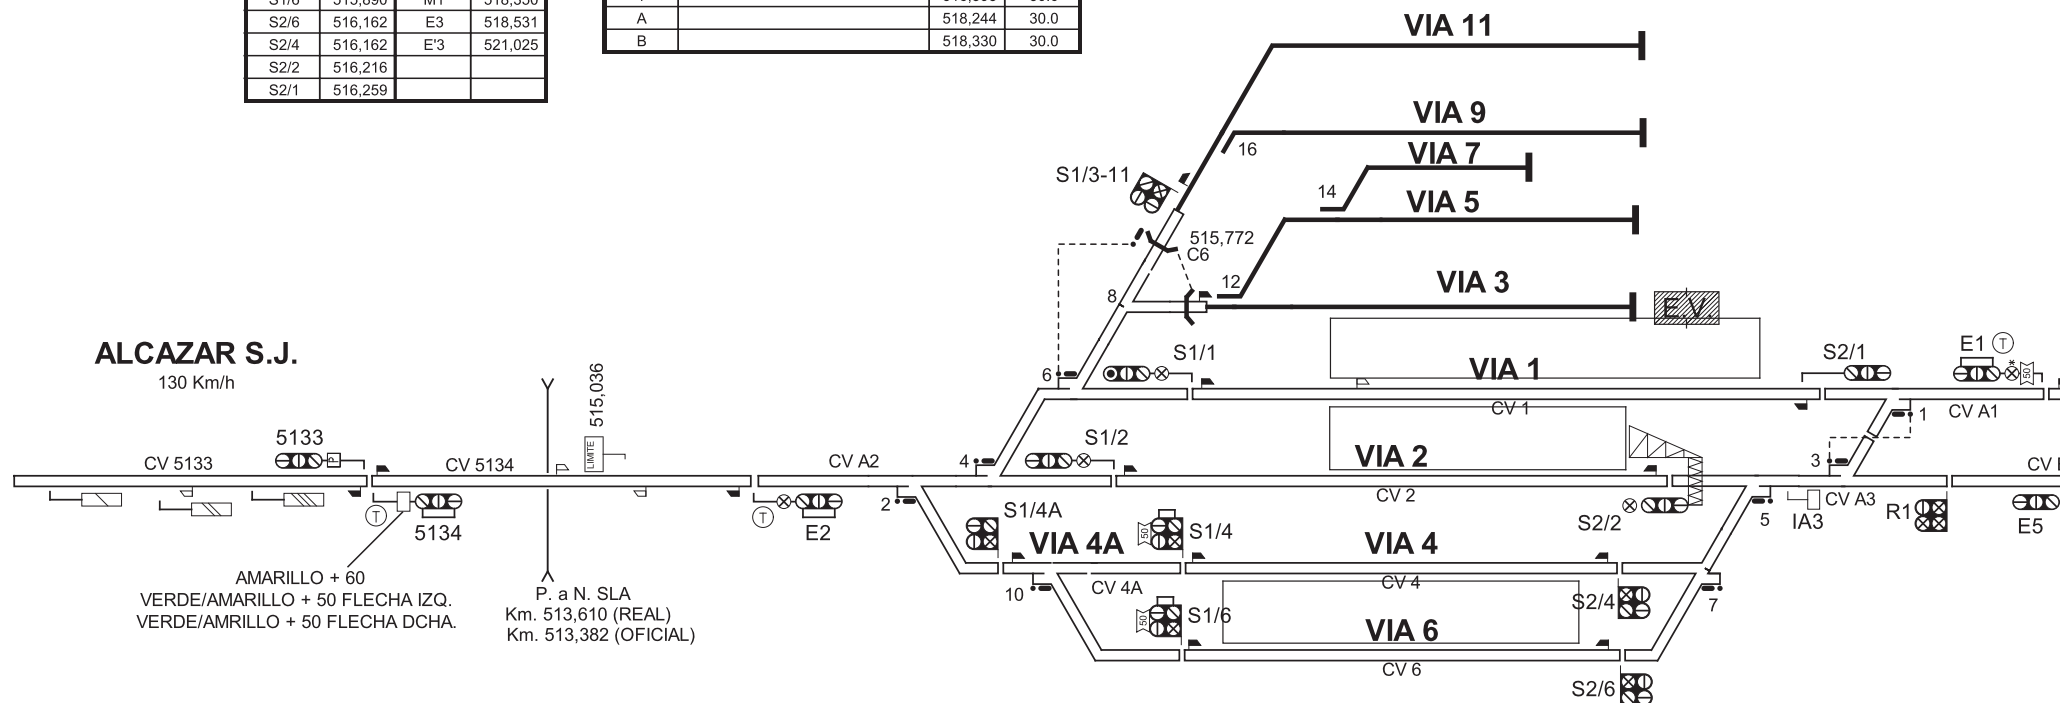

NOTAS.- LAS SEÑALES EXTERIORES LADO ALCAZAR
NO EFECTUARAN APERTURA MIENTRAS
QUE LA SEÑAL 5133 PRESENTE PARADA

LAS MANIOBRAS CENTRALIZADAS DE SALIDA , LADO ALCÁZAR DE S.J.
SON INCOMPATIBLES CON BLOQUEO RECEPTOR.

ACTUALIZACIONES			NOMBRE	
VERSION	MOTIVO	FECHA	REVISADO	MATA
1	CONSIGNA	08/04/2016	ELABORADO	MANZANO
2	CONSIGNA	12/05/2016	APROBADO	RINCON
3	CONSIGNA	20/05/2016	Nº: C-400-07-50600	
4	CONSIGNA	01/06/2016		
5	CONSIGNA	29/06/2016	HOJA: 1 de 2	
6	CONSIGNA	21/07/2016	NOMBRE DE FICHERO	
			C-400-07 LORA DEL RIO V.06	



SUBDIRECCION DE
PROG. DE INSTALACIONES

LORA DEL RIO