


EL PRIORATO

EL PRIORATO - L400_ALCAZAR S.J.-CADIZ - Km 506,119

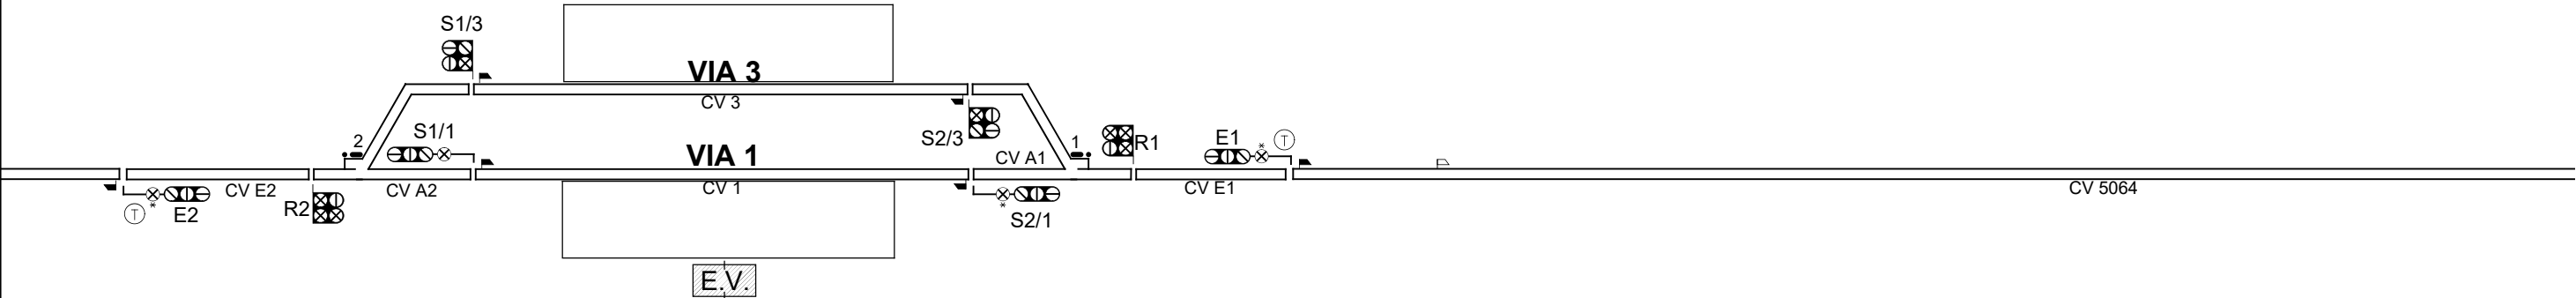

APARATOS - EL PRIORATO			
Nº	Modelo	P.K. 1	VEL.
2		506,084	30.0
1		506,813	30.0

SEÑALES - EL PRIORATO			
Nombre	P.K.	Nombre	P.K.
5040	504,073	S2/3	506,732
E2	505,811	S2/1	506,732
R2	506,084	R1	506,831
S1/3	506,168	E1	507,084
S1/1	506,168	5089	509,001

ACTUALIZACIONES				NOMBRE	
VERSION	MOTIVO	FECHA	ELABORADO	REVISADO	HERRERO
1	CONSIGNA	27/05/2016	MELLENDEZ	ELABORADO	MELLENDEZ
2	CONSIGNA	20/06/2016	MELLENDEZ	APROBADO	J. A. DELGADO
3	CONSIGNA	06/06/2017	MANZANO	C-400-06	
4	CONSIGNA	10/01/2020	OLEA		
				HOJA: 22 de 25	
				NOMBRE DE FICHERO	
				C-400-06 EL HIGUERON-LORA DEL RIO	



GERENCIA DE AREA DE
PROG. DE INSTALACIONES

EL HIGUERON - LORA DEL RIO