


PUERTO REAL (APD.)

Km. 133,397

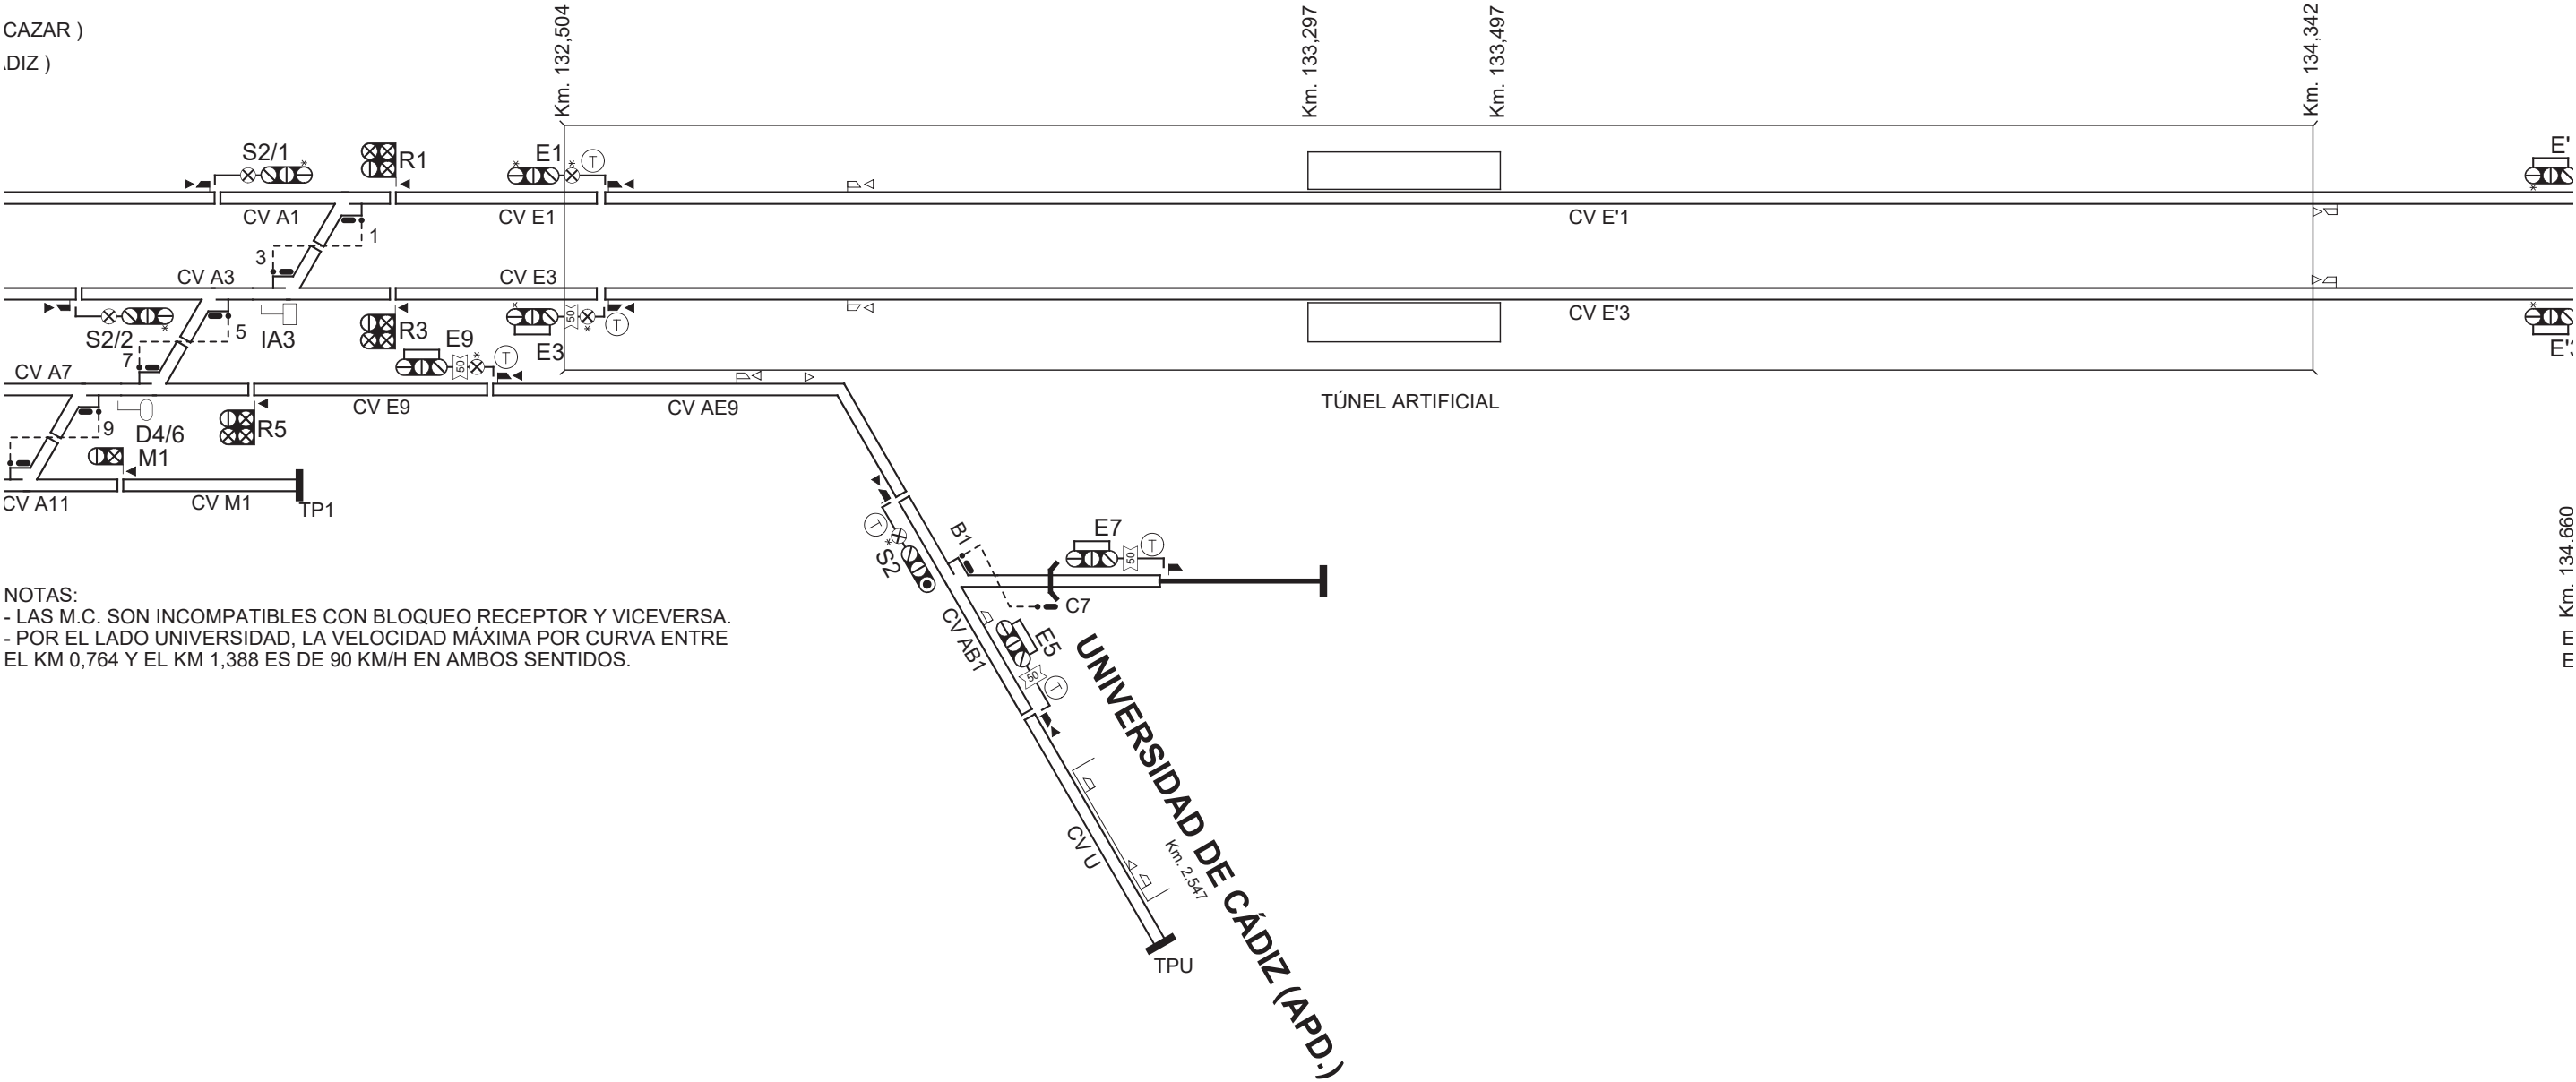

NOTAS:
- LAS M.C. SON INCOMPATIBLES CON BLOQUEO RECEPTOR Y VICEVERSA.
- POR EL LADO UNIVERSIDAD, LA VELOCIDAD MÁXIMA POR CURVA ENTRE EL KM 0,764 Y EL KM 1,388 ES DE 90 KM/H EN AMBOS SENTIDOS.

ACTUALIZACIONES				NOMBRE	
VERSION	MOTIVO	FECHA	ELABORADO	REVISADO	A.ALONSO
9	CONSIGNA	29/10/2019	MANZANO	ELABORADO	MANZANO
10	CONSIGNA	11/03/2020	I. PEÑA	APROBADO	J. A. DELGADO
11	CONSIGNA	17/03/2022	A. VAZQUEZ	T-40011-C1	
12	CONSIGNA	31/03/2022	A.VAZQUEZ		
13	CONSIGNA	15/06/2022	I. PEÑA	HOJA:	10 de 22
14	CONSIGNA	13/12/2022	A. OLEA	NOMBRE DE FICHERO	
15	CONSIGNA	22/12/2022	A.VAZQUEZ	T-40011-C1 JEREZ DE LA F.-CADIZ_V.15	



GERENCIA DE AREA DE
PROG. DE INSTALACIONES

JEREZ DE LA FRONTERA-CADIZ