


SAN FERNANDO-BAHIA SUR

SAN FERNANDO-BAHIA SUR - (C1) - L400_ALCAZAR S.J.-CADIZ - Km 143,845

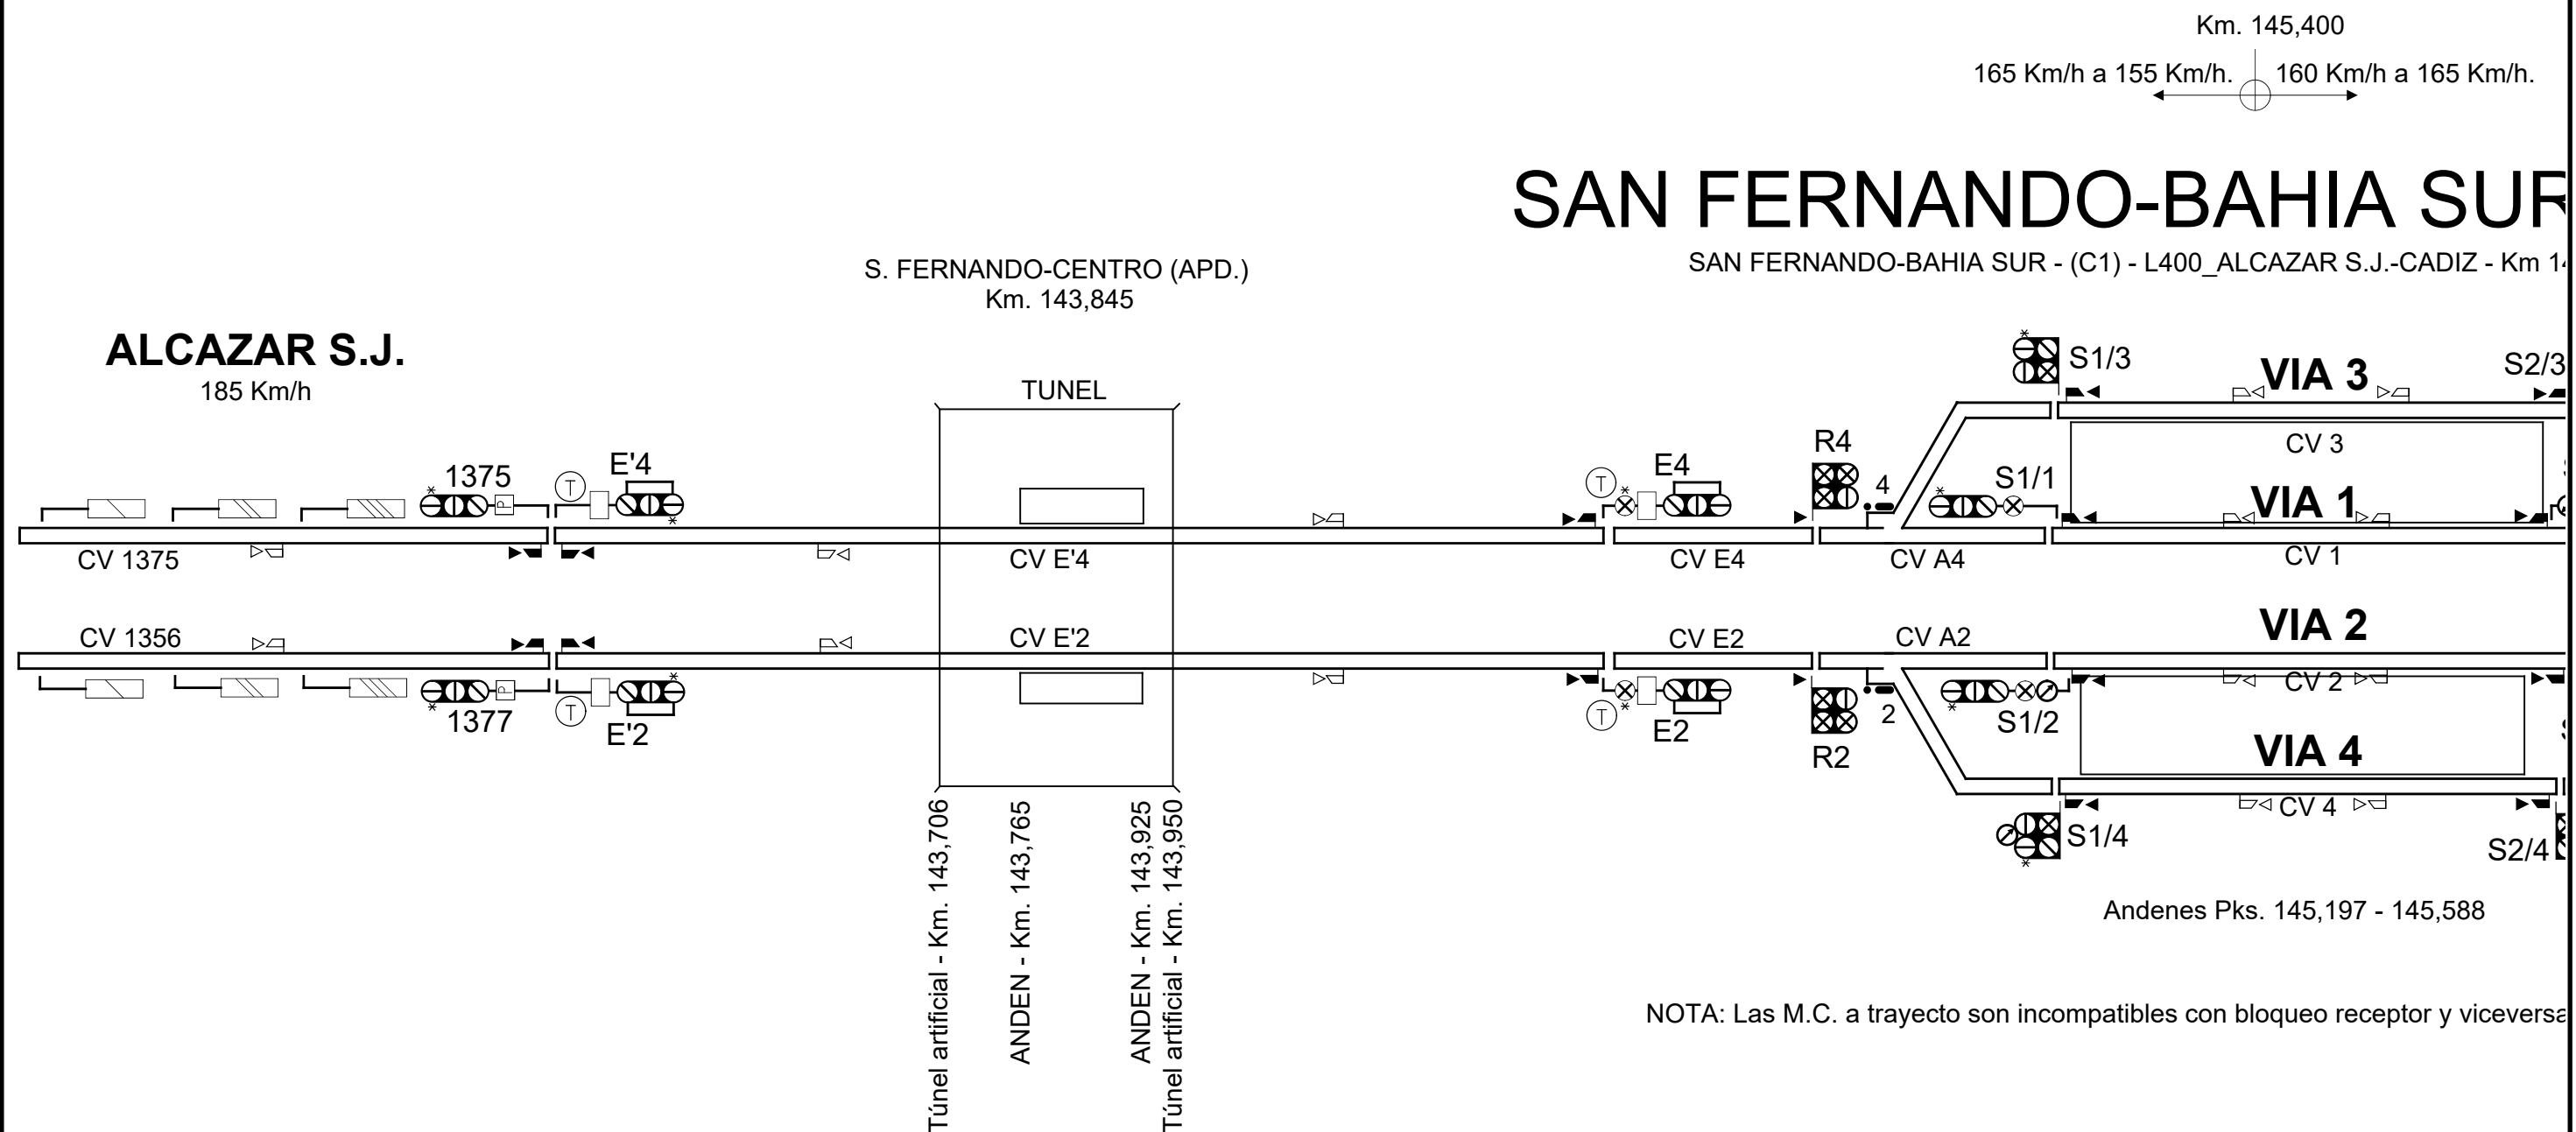

SEÑALES - SAN FERNANDO-BAHIA SUR - (C1)			
Nombre	P.K.	Nombre	P.K.
E'4	142,734	S2/1	145,604
E'2	142,734	S2/2	145,604
1375	142,754	S2/3	145,604
1377	142,754	IA15	145,671
E2	144,708	IA11	145,757
E4	144,709	R7	145,860
R4	145,106	R5	145,860
R2	145,106	E5	146,112
S1/1	145,200	E7	146,112
S1/2	145,200	E8	146,634
S1/3	145,203	E6	146,634
S1/4	145,203	S1/1B	147,154
S2/4	145,597	S1/2B	147,154

APARATOS - SAN FERNANDO-BAHIA SUR - (C1)			
Nº	Modelo	P.K. 1	VEL.
4		145,135	30.0
2		145,135	30.0
17		145,668	30.0
19		145,668	30.0
15		145,677	50.0
13		145,752	50.0
11		145,760	50.0
9		145,835	50.0

ACTUALIZACIONES				NOMBRE	
VERSION	MOTIVO	FECHA	ELABORADO	REVISADO	ALONSO
7	CONSIGNA	11/03/2020	I. PEÑA	ELABORADO	MANZANO
8	CONSIGNA	17/03/2022	A.VAZQUEZ	APROBADO	J. A. DELGADO
				T-40011-C1-51406-A	
				HOJA: 1 de 2	
				NOMBRE DE FICHERO	
				T-40011-C1 S. FERNANDO-BAHIA_V.08	




GERENCIA DE AREA DE
PROG. DE INSTALACIONES

**SAN FERNANDO-BAHÍA
SUR**

5 Km/h.

SUR - (C1)

01Z - Km 145,365

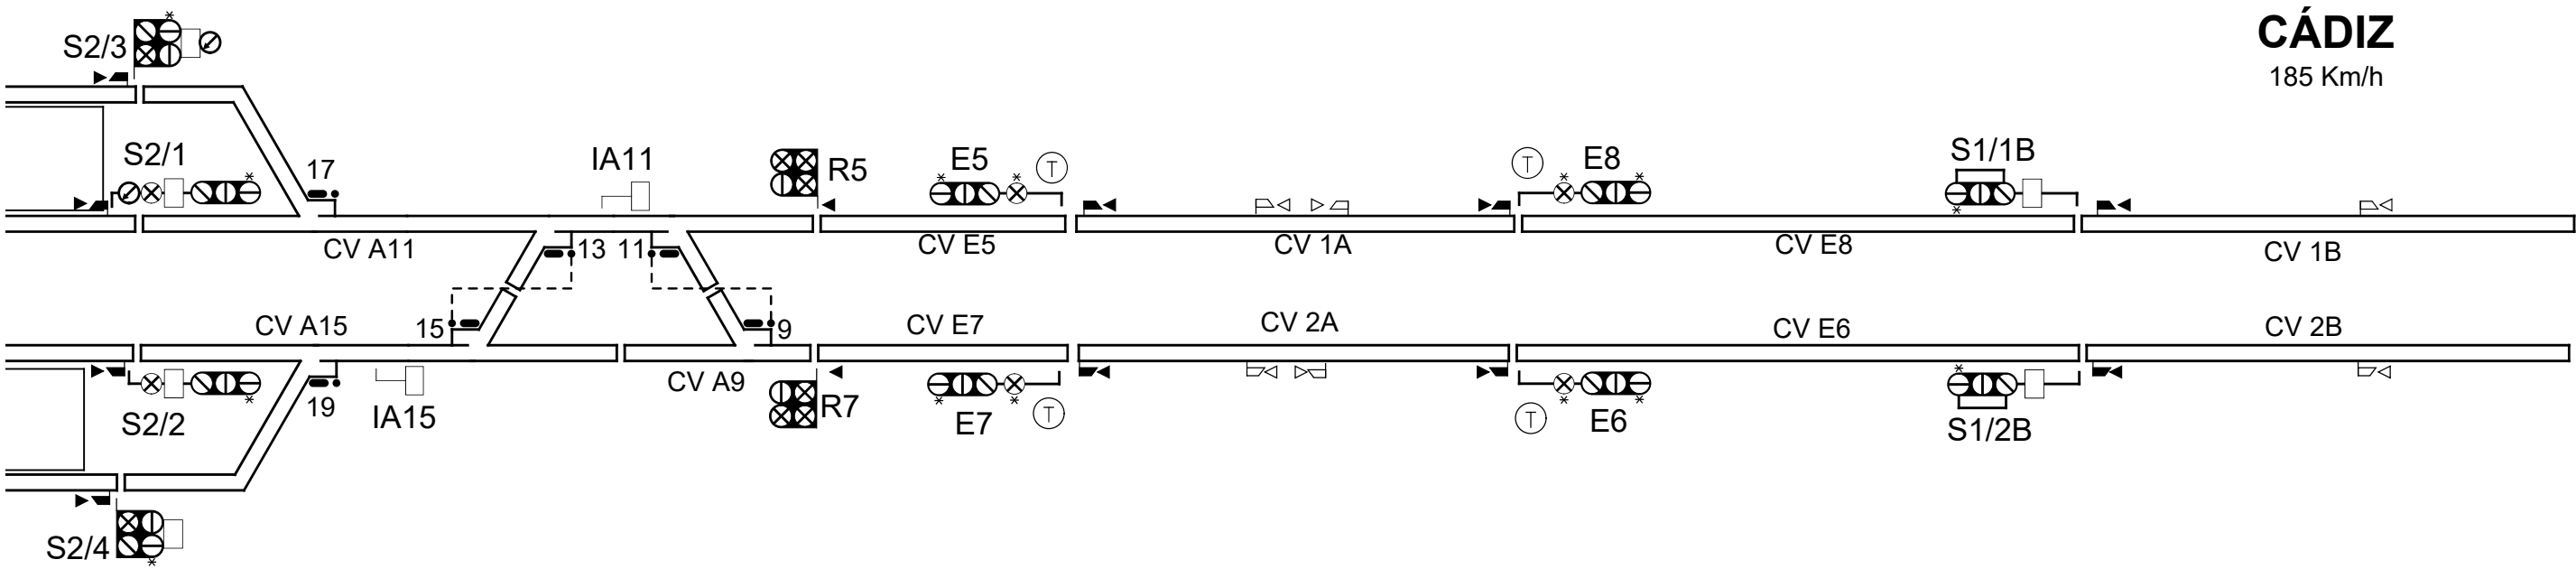

588

SEÑALES
S2/1
S2/2 AMARILLO + 90
S2/3
S2/4

viceversa.

ACTUALIZACIONES				NOMBRE	
VERSION	MOTIVO	FECHA	ELABORADO	REVISADO	ALONSO
7	CONSIGNA	11/03/2020	I. PEÑA	ELABORADO	MANZANO
8	CONSIGNA	17/03/2022	A.VAZQUEZ	APROBADO	J. A. DELGADO
				T-40011-C1-51406-A	
				HOJA: 2 de 2	
				NOMBRE DE FICHERO	
				T-40011-C1 S. FERNANDO-BAHIA_V.08	

 GERENCIA DE AREA DE
PROG. DE INSTALACIONES

**SAN FERNANDO-BAHÍA
SUR**