


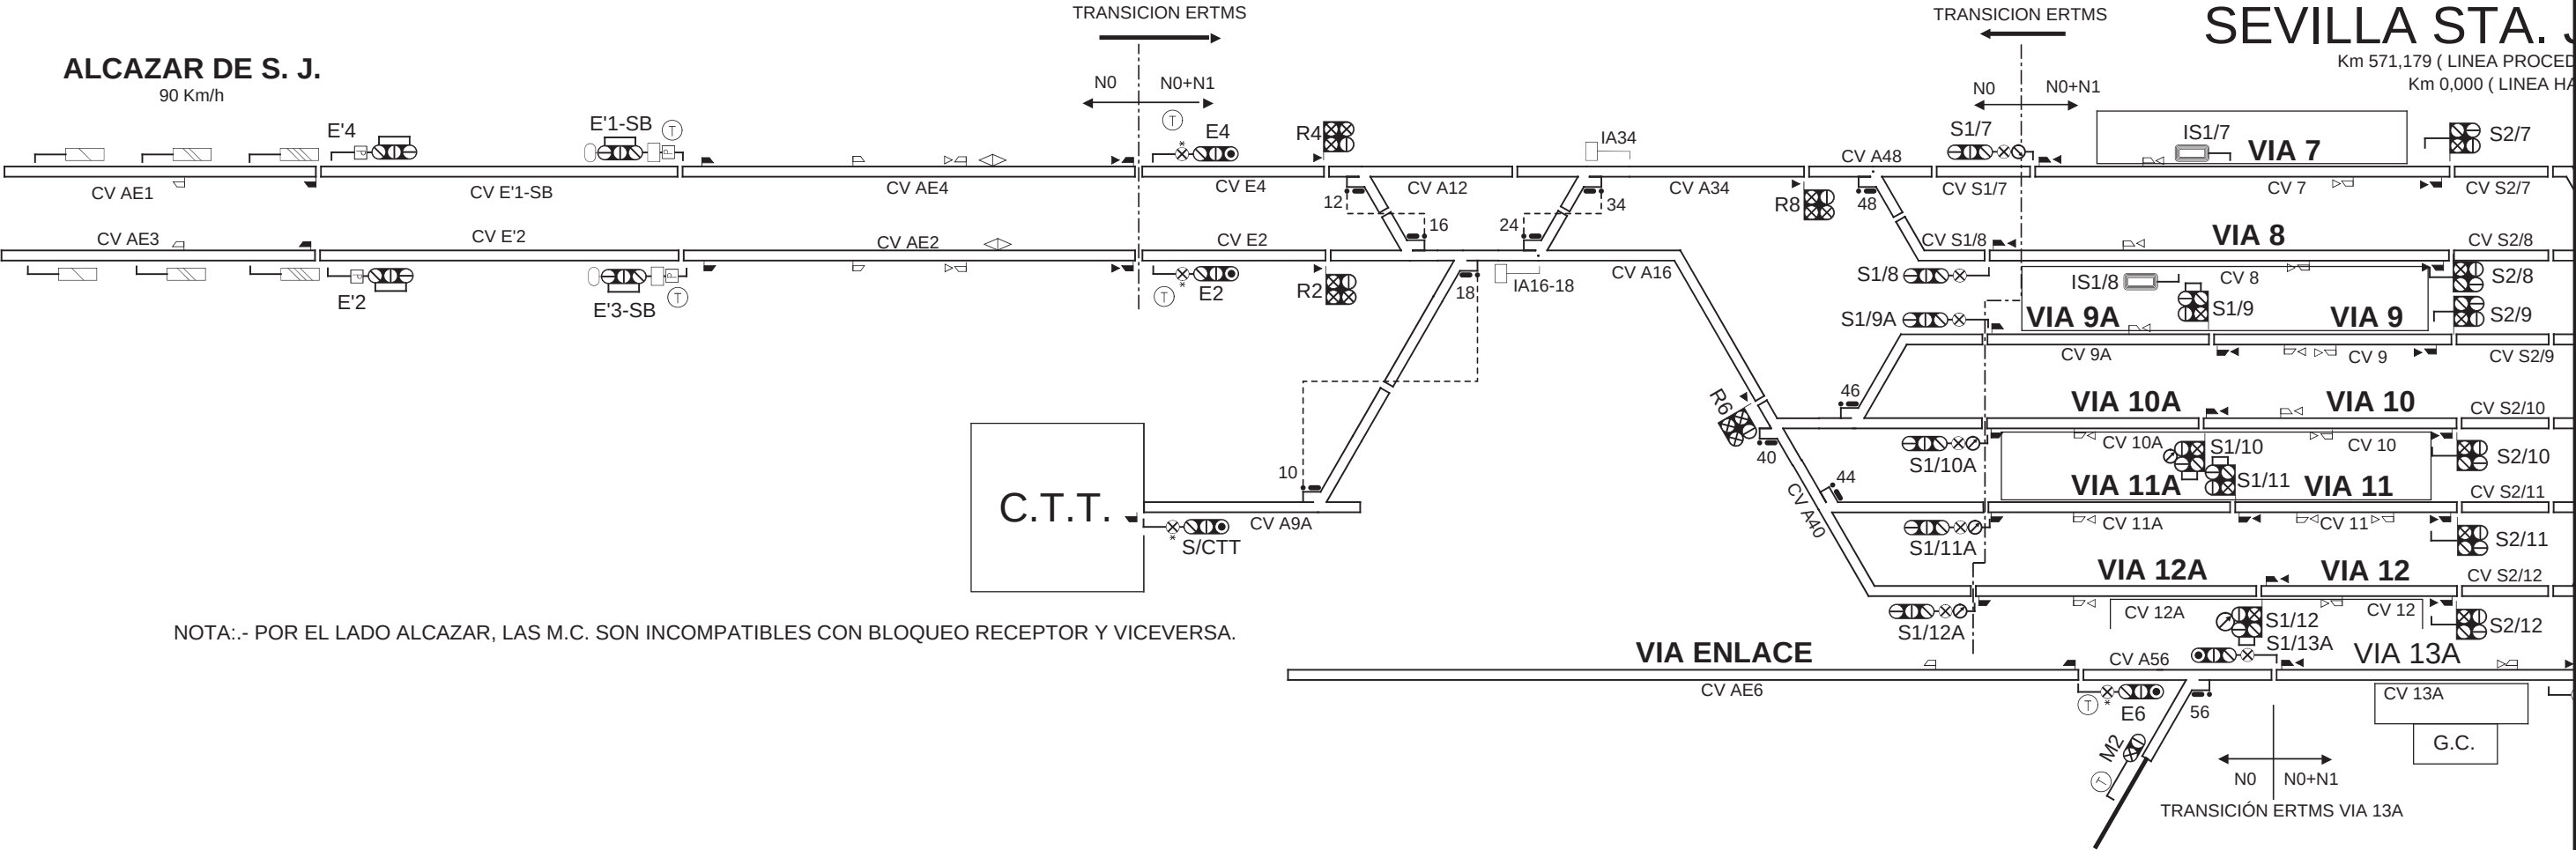

NOTA:- POR EL LADO ALCAZAR, LAS M.C. SON INCOMPATIBLES CON BLOQUEO RECEPTOR Y VICEVERSA.

APARATOS - SEVILLA STA. JUSTA - (C1)									
Nº	Modelo	P.K. 1	P.K. 2	VEL.	Nº	Modelo	P.K. 1	P.K. 2	VEL.
TOP M1		0,766			56		570,980		30.0
10		570,449		30.0	19		571,631	0,452	30.0
12		570,474		30.0	17		571,637	0,458	30.0
16		570,537		30.0	15		571,647	0,468	30.0
18		570,576		30.0	13		571,674	0,495	30.0
24		570,581		30.0	11		571,683	0,504	30.0
34		570,644		30.0	9		571,719	0,540	30.0
40		570,693		30.0	7		571,751	0,572	30.0
48		570,711		30.0	5		571,752	0,573	30.0
46		570,749		30.0	3		571,855	0,676	30.0
44		570,749		30.0	1		571,927	0,748	30.0

SEÑALES - SEVILLA STA. JUSTA - (C1)							
Nombre	P.K.	Nombre	P.K.	Nombre	P.K.	Nombre	P.K.
S2/11	0,210	E3	1,021	R4	570,453	E6	570,945
S2/9	0,210	E1	1,021	IA16-18	570,583	M2	570,984
S2/8	0,210	18	1,756	IA34	570,659	S1/11	571,048
S2/10	0,210	20	1,786	R6	570,674	S1/10	571,048
S2/12	0,210	E'3	1,800	R8	570,690	S1/9	571,048
S2/7	0,210	E'1	1,800	S1/12A	570,819	S1/12	571,048
S2/13A	0,255	E'2	569,240	S1/11A	570,820	IS1/7	571,050
S2/13	0,470	E'4	569,240	S1/9A	570,832	IS1/8	571,050
M1	0,640	E2	570,202	S1/10A	570,832	S1/13A	571,138
R3	0,750	E4	570,204	S1/7	570,922		
R1	0,767	R2	570,453	S1/8	570,922		

ACTUALIZACIONES				NOMBRE	
VERSION	MOTIVO	FECHA	ELABORADO	REVISADO	ALONSO
7	CONSIGNA	17/05/2019	MANZANO	ELABORADO	I. PEÑA
8	CONSIGNA	20/07/2019	MANZANO	APROBADO	J. A. DELGADO
9	CONSIGNA	01/08/2019	MANZANO		
10	CONSIGNA	07/11/2019	MANZANO		
11	CONSIGNA	11/03/2020	I. PEÑA	HOJA:	1 de 2
				NOMBRE DE FICHERO	
				T-40009-C1 SEVILLA STA. JUSTA_V.10	



GERENCIA DE AREA DE
PROG. DE INSTALACIONES

SEVILLA SANTA JUSTA

(ERTMS)

STA. JUSTA - (C1)


LINEA PROCEDENTE DE ALCAZAR)
000 (LINEA HACIA CADIZ)

SAN BERNARDO (APD.)

Km 1,956

Km 2,874

LA SALUD
160 Km/h

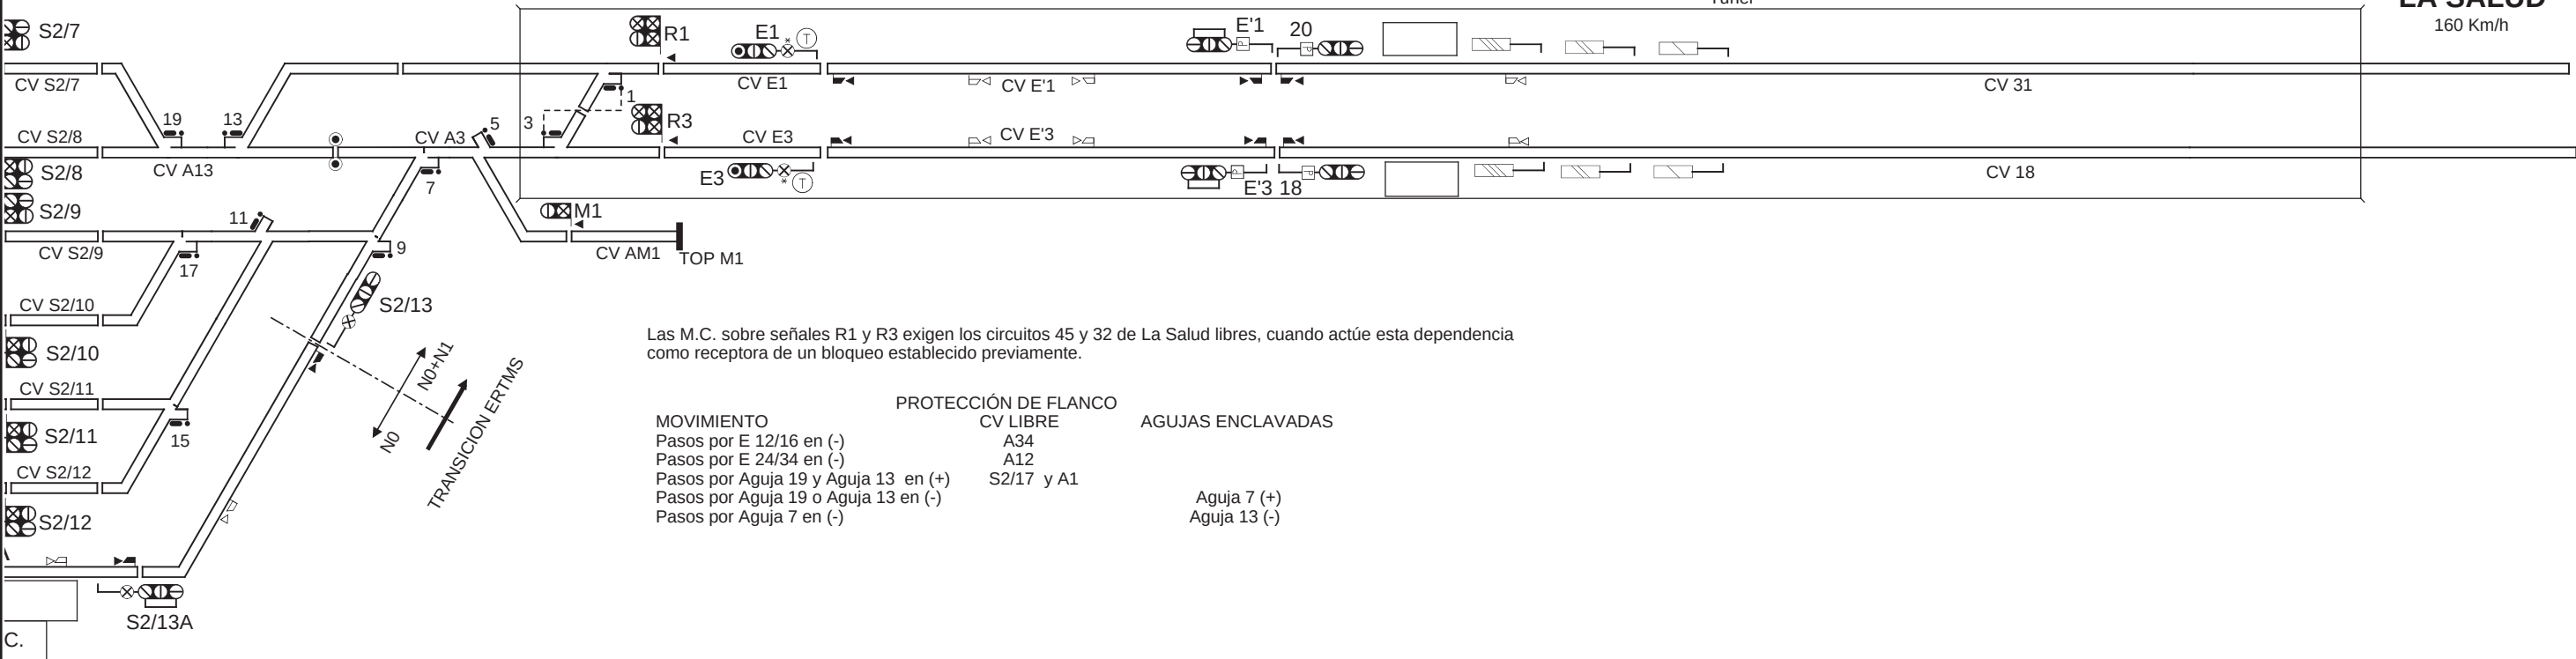

ACTUALIZACIONES				NOMBRE	
VERSION	MOTIVO	FECHA	ELABORADO	REVISADO	ALONSO
7	CONSIGNA	17/05/2019	MANZANO	ELABORADO	I. PEÑA
8	CONSIGNA	20/07/2019	MANZANO	APROBADO	J. A. DELGADO
9	CONSIGNA	01/08/2019	MANZANO	T-40009-C1-51003	
10	CONSIGNA	07/11/2019	MANZANO		
11	CONSIGNA	11/03/2020	I. PEÑA	HOJA:	2 de 2
				NOMBRE DE FICHERO	
				T-40009-C1 SEVILLA STA. JUSTA_V.10	



GERENCIA DE AREA DE
PROG. DE INSTALACIONES

SEVILLA SANTA JUSTA
(ERTMS)