


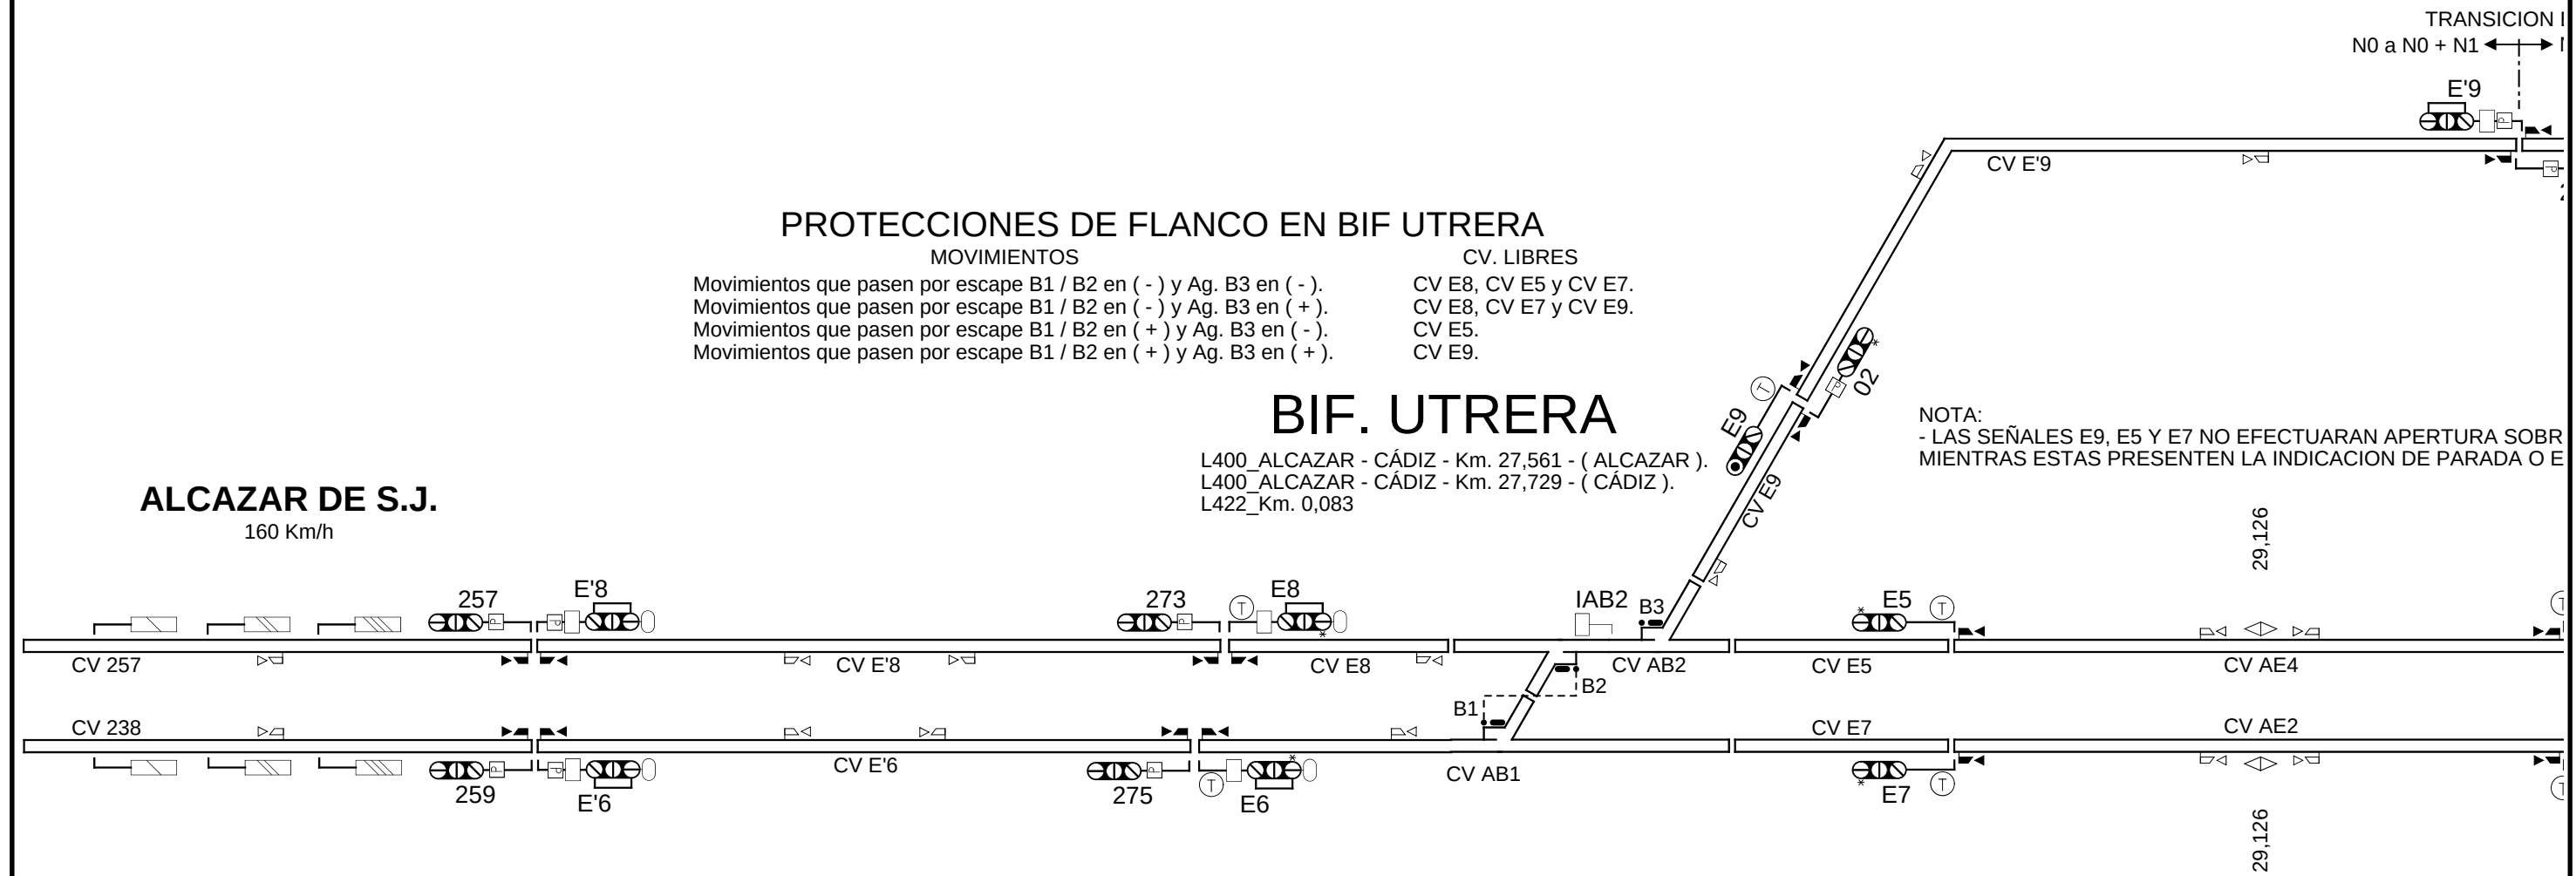

PROTECCIONES DE FLANCO EN BIF UTRERA

MOVIMIENTOS

Movimientos que pasen por escape B1 / B2 en (-) y Ag. B3 en (-).

Movimientos que pasen por escape B1 / B2 en (-) y Ag. B3 en (+).

Movimientos que pasen por escape B1 / B2 en (+) y Ag. B3 en (-).

Movimientos que pasen por escape B1 / B2 en (+) y Ag. B3 en (+).

CV. LIBRES

CV E8, CV E5 y CV E7.

CV E8, CV E7 y CV E9.

CV E5.

CV E9.

BIF. UTRERA

L400_ALCAZAR - CÁDIZ - Km. 27,561 - (ALCAZAR).

L400_ALCAZAR - CÁDIZ - Km. 27,729 - (CÁDIZ).

L422_Km. 0,083

NOTA:

- LAS SEÑALES E9, E5 Y E7 NO EFECTUARAN APERTURA SOBR MIENTRAS ESTAS PRESENTEN LA INDICACION DE PARADA O E'9

TRANSICION DE 200 A 160 Km / h.

SENTIDO CÁDIZ - SEVILLA

SEÑALES DE SALIDA	S1/1A, S1/2 y S1/4A	E7 y E5
VERDE	VERDE CONDICIONAL	VERDE CONDICIONAL
VERDE CONDICIONAL	AMARILLO	AMARILLO
VERDE CONDICIONAL	AMARILLO	ROJO
VERDE CONDICIONAL	AMARILLO	APAGADA

NOTA:


El aspecto maximo de las señales S1/1A, S1/2, S1/4A, E5 y E7 es de VERDE CONDICIONAL.

ACTUALIZACIONES				NOMBRE	
VERSION	MOTIVO	FECHA	ELABORADO	REVISADO	ALONSO
1	CONSIGNA	21/08/2018	I. PEÑA	ELABORADO	I. PEÑA
2	CONSIGNA	11/03/2020	I. PEÑA	APROBADO	J. A. DELGADO
				T-40010-C1-51200	
				HOJA: 1 de 3	
				NOMBRE DE FICHERO	
				T-40010-C1 UTRERA_V.02	



GERENCIA DE AREA DE
PROG. DE INSTALACIONES

UTRERA

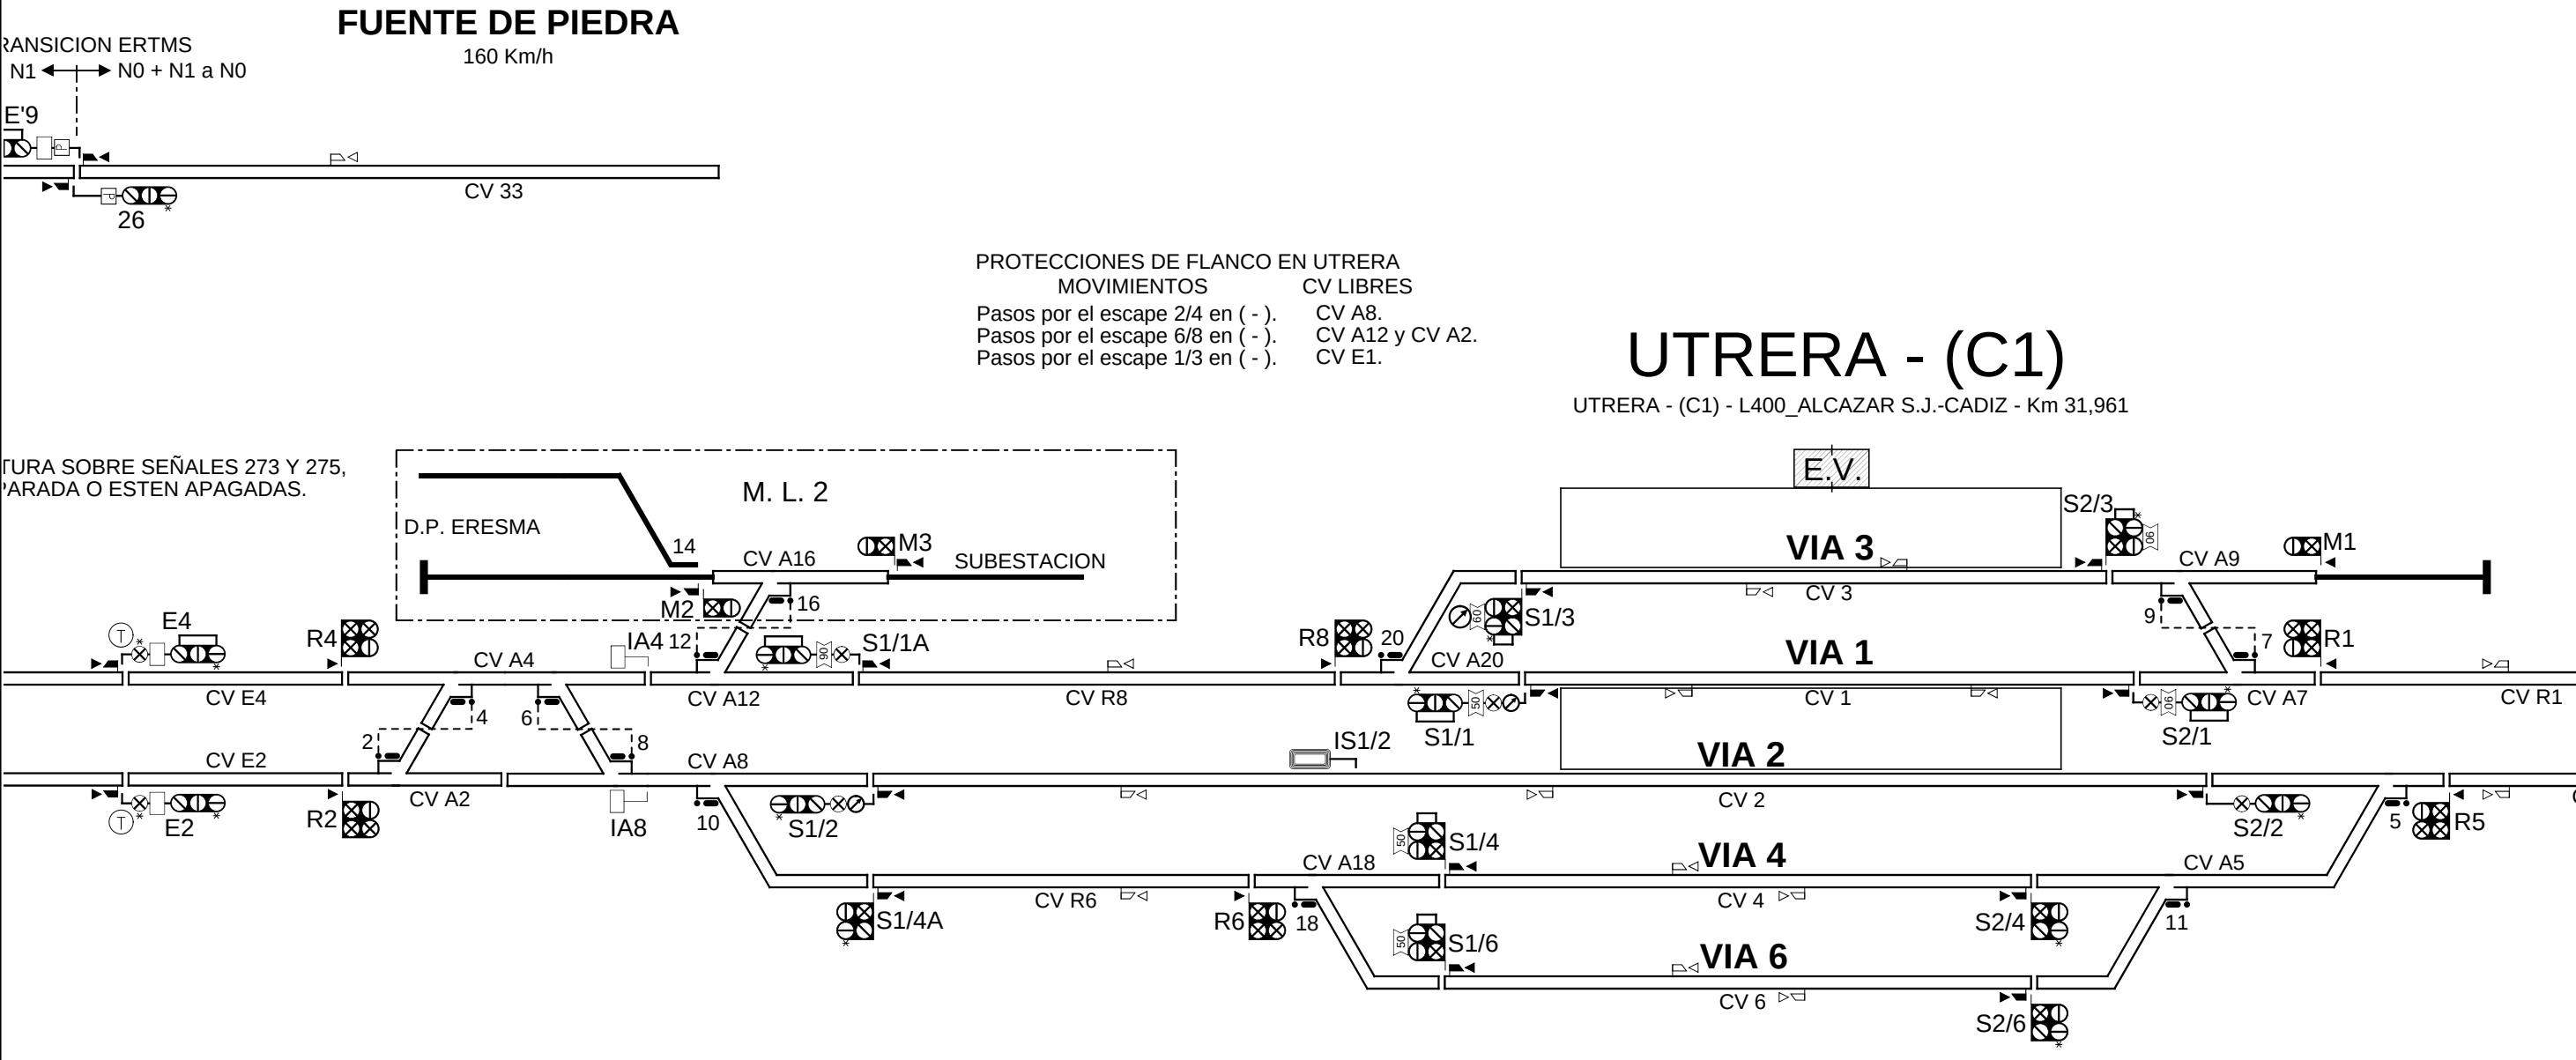

APARATOS - UTRERA - (C1)									
Nº	Modelo	P.K. 1	P.K. 2	VEL.	Nº	Modelo	P.K. 1	P.K. 2	VEL.
B1		27,341		100.0	16		30,894		50.0
B2		27,503		100.0	18		31,478		50.0
B3		27,729	-0,082	100.0	20		31,572		50.0
2		30,483		60.0	11		31,902		40.0
4		30,578		60.0	9		31,925		50.0
6		30,640		60.0	7		31,996		50.0
8		30,733		60.0	5		32,027		50.0
12		30,801		50.0	3		32,580		100.0
10		30,801		50.0	1		32,744		100.0

SEÑALES - UTRERA - (C1)											
Nombre	P.K.	Nombre	P.K.	Nombre	P.K.	Nombre	P.K.	Nombre	P.K.	Nombre	P.K.
02	0,217	275	27,084	R4	30,464	IS1/2	31,516	S2/1	31,923	330	33,055
E9	0,241	E8	27,089	IA4	30,796	S1/4	31,540	S2/2	31,949	E3	33,075
26	2,393	273	27,113	IA8	30,796	S1/6	31,540	M1	32,016	E1	33,075
E'9	2,418	IAB2	27,722	M2	30,815	R8	31,544	R1	32,016	350	35,000
E'6	25,372	E7	28,027	S1/1A	30,881	S1/1	31,643	R5	32,046	352	35,000
E'8	25,372	E5	28,027	S1/4A	30,893	S1/3	31,644	S2/2A	32,560	E'3	35,020
259	25,397	E2	30,213	S1/2	30,893	S2/4	31,841	S2/1A	32,560	E'1	35,020
257	25,397	E4	30,214	M3	30,906	S2/6	31,842	IA3	32,565		
E6	27,080	R2	30,463	R6	31,458	S2/3	31,903	R3	32,763		

ACTUALIZACIONES				NOMBRE	
VERSION	MOTIVO	FECHA	ELABORADO	REVISADO	ALONSO
1	CONSIGNA	21/08/2018	I. PEÑA	ELABORADO	I. PEÑA
2	CONSIGNA	11/03/2020	I. PEÑA	APROBADO	J. A. DELGADO
				T-40010-C1-51200	
				HOJA: 2 de 3	
				NOMBRE DE FICHERO	
				T-40010-C1 UTRERA_V.02	



UTRERA