


SEÑALIZACION
Vmax. 160 Km/h. ← Vmax. 140 Km/h.

AZNALCAZAR-PILAS - (C1)

AZNALCAZAR-PILAS - (C1) - L440_BIF. LOS NARANJOS - HUELVA - Km 35,560

P.a N. - S.B.E.
CLASE " C "
Km 35,784

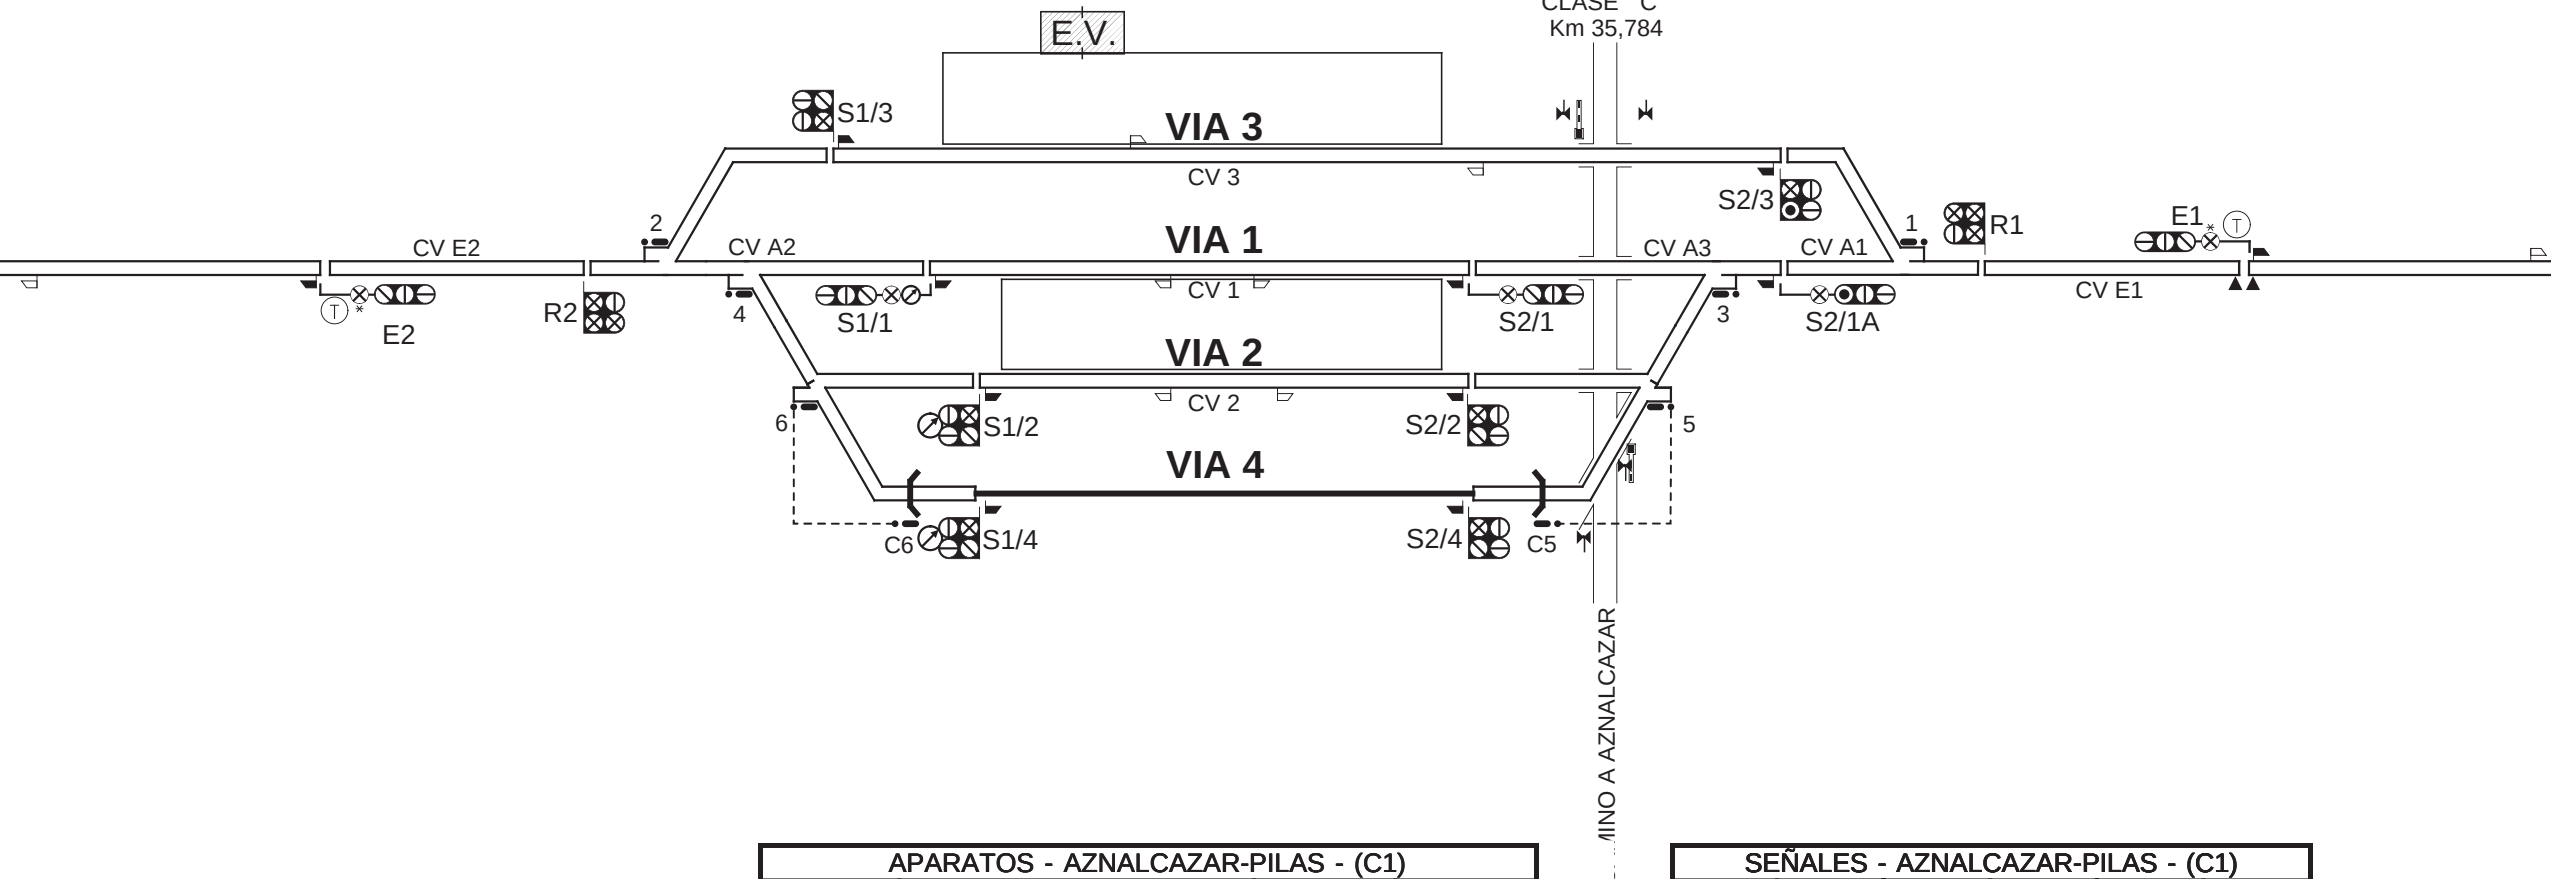

APARATOS - AZNALCAZAR-PILAS - (C1)			
Nº	Modelo	P.K. 1	VEL.
2		35,323	30.0
4		35,377	50.0
6		35,424	30.0
5		35,858	30.0
3		35,906	30.0
1		36,052	45.0

SEÑALES - AZNALCAZAR-PILAS - (C1)					
Nombre	P.K.	Nombre	P.K.	Nombre	P.K.
E'2	32,776	S1/4	35,493	S2/3	35,965
327	32,794	S1/2	35,493	R1	36,072
E2	35,040	S2/1	35,771	E1	36,328
R2	35,303	S2/4	35,771	E'1	38,140
S1/3	35,397	S2/2	35,771		
S1/1	35,459	S2/1A	35,965		

ACTUALIZACIONES			NOMBRE	
VERSION	MOTIVO	FECHA	REVISADO	ALONSO
1	CONSIGNA	12/08/2019	ELABORADO	I. PEÑA
			APROBADO	J. A. DELGADO
			T-4401-C1	
			HOJA:	16 de 17
			NOMBRE DE FICHERO	
			T-4401-C1 BIF.CARTUJA-AZNALCAZAR-PILAS_V.01	



GERENCIA DE AREA DE
PROG. DE INSTALACIONES

**BIF. CARTUJA -
AZNALCAZAR-PILAS**