


SEÑALES - HUELVA-MERCANCÍAS											
Nombre	P.K.	Nombre	P.K.	Nombre	P.K.	Nombre	P.K.	Nombre	P.K.	Nombre	P.K.
E'2	101,800	D1	104,285	S2/10	105,050	S2/4A	105,592	E3	106,002	E'5/S1	108,524
E2	103,379	S1/4	104,290	S2/8	105,052	S2/T	105,592	E1	106,228	E'7	109,211
R2	103,785	S1/6	104,359	S2/6	105,102	S2/2	105,629	S6	107,287	E'9	109,211
R4	103,795	S1/L	104,370	S2/4	105,191	M3	105,645	SB	107,297	E'4	177,764
M6	103,940	S1/30	104,370	M7	105,283	S4	105,660	E5	107,653	E4	179,258
M9	103,980	S1/8	104,391	E11	105,306	M1	105,729	E2/HT	107,653		
M4	104,063	S1/12	104,408	M2	105,403	R3	105,802	E9	107,772		
S1/2	104,135	S1/10	104,408	M5	105,465	R1	105,976	E7	107,776		

HUELVA-MERCANCÍAS

HUELVA-MERCANCÍAS - L440_BIF. LOS NARANJOS - HUELVA - Km 104,720
HUELVA-MERCANCÍAS - L512_ZAFRA - HUELVA-MERCANCÍAS - Km 180,840

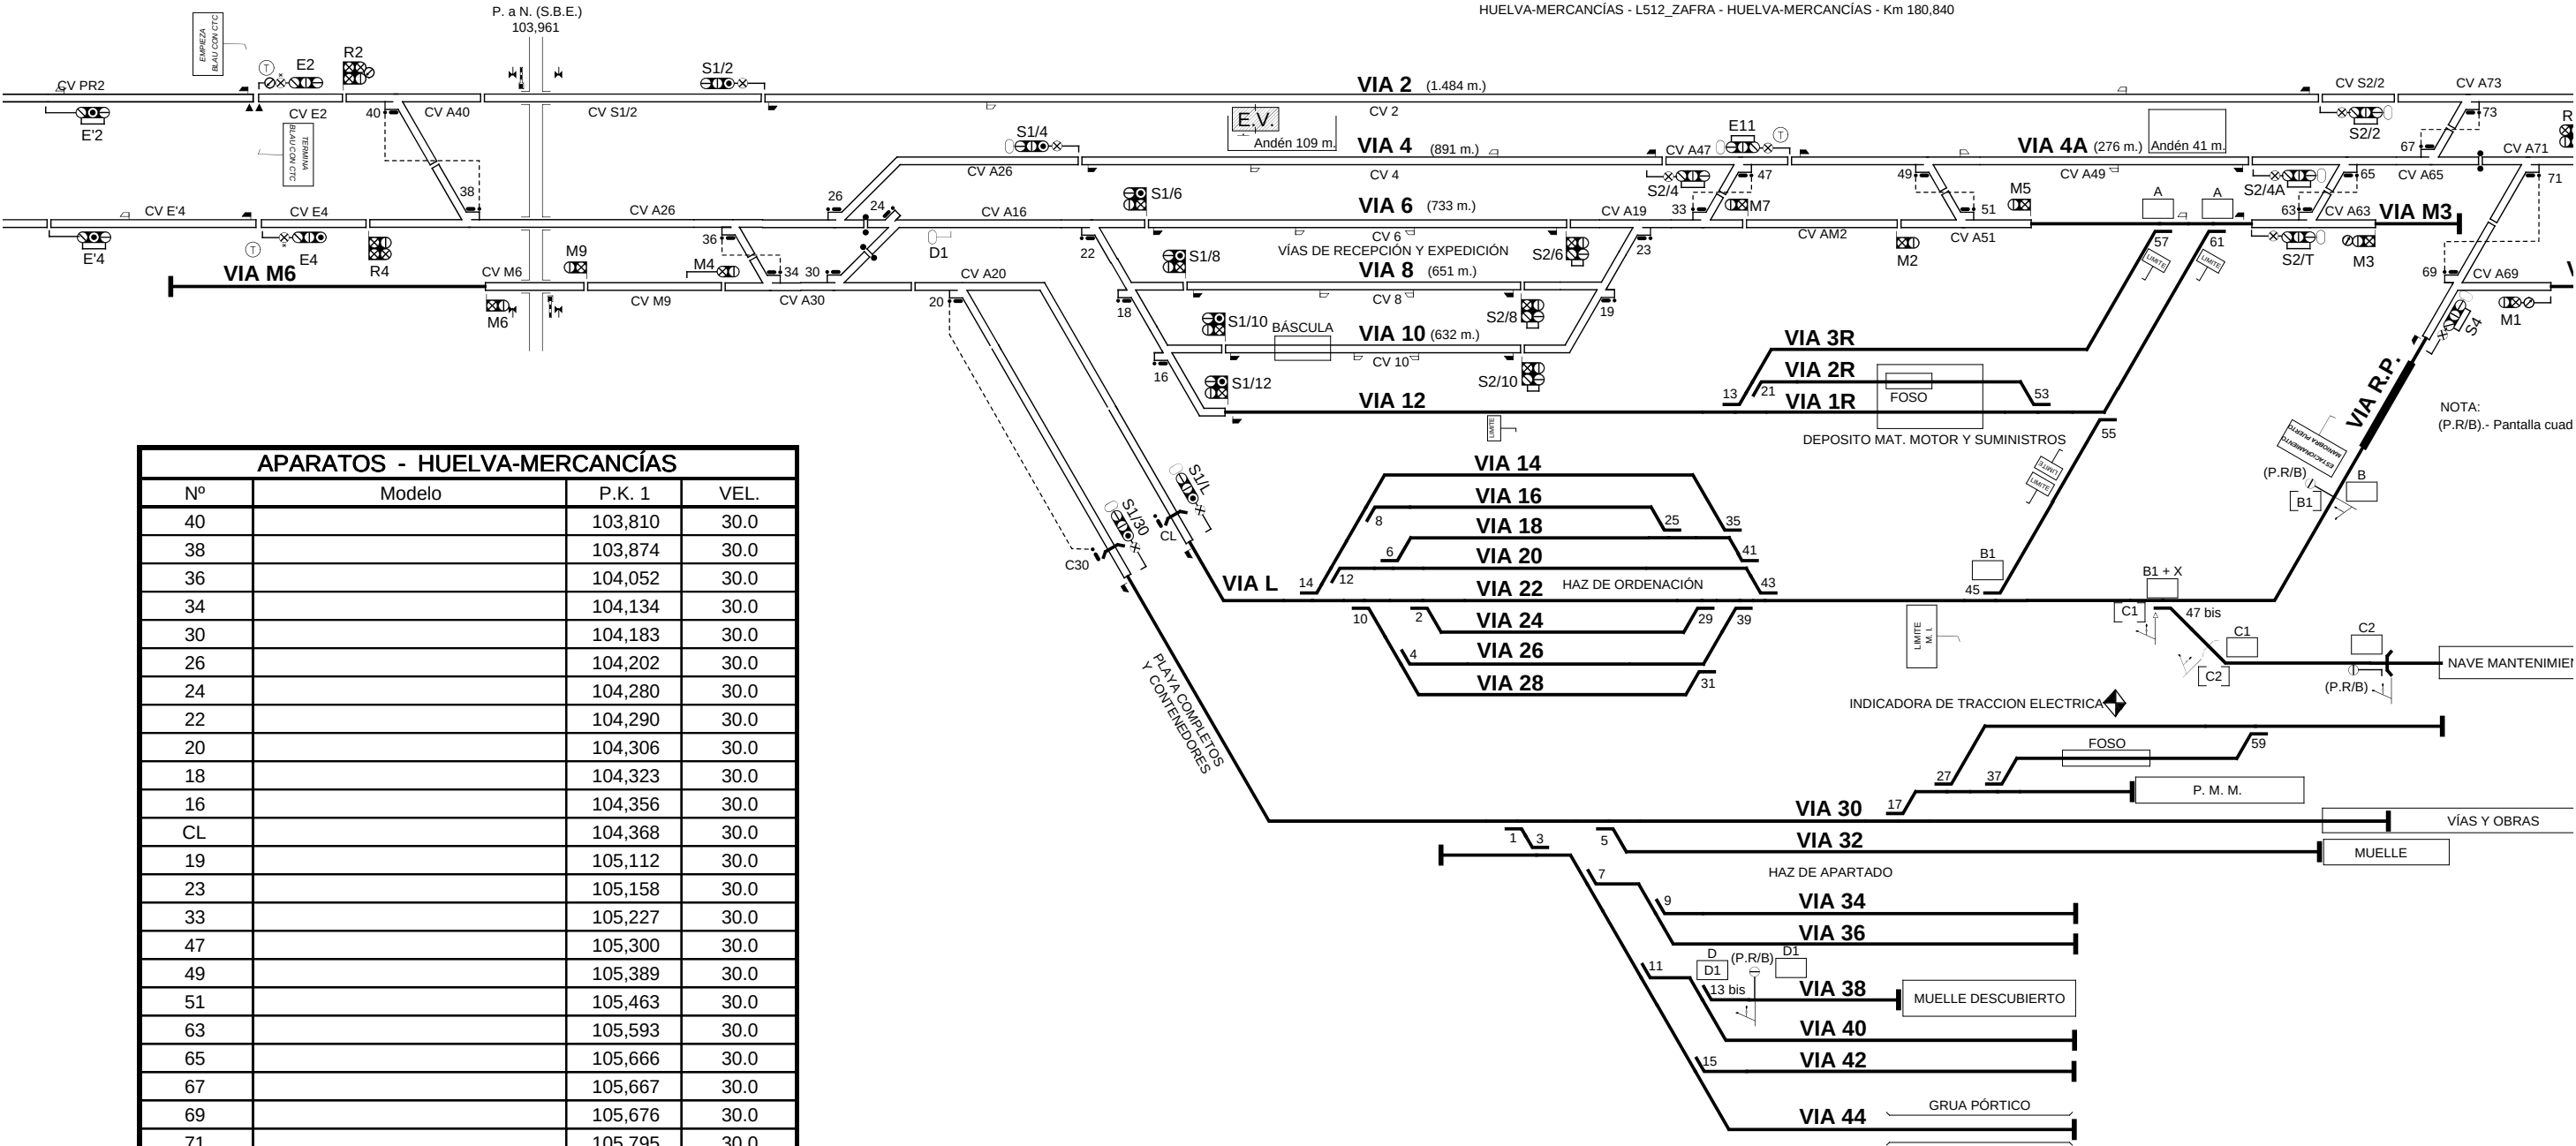


APARATOS - HUELVA-MERCANCÍAS			
Nº	Modelo	P.K. 1	VEL.
40		103,810	30.0
38		103,874	30.0
36		104,052	30.0
34		104,134	30.0
30		104,183	30.0
26		104,202	30.0
24		104,280	30.0
22		104,290	30.0
20		104,306	30.0
18		104,323	30.0
16		104,356	30.0
CL		104,368	30.0
19		105,112	30.0
23		105,158	30.0
33		105,227	30.0
47		105,300	30.0
49		105,389	30.0
51		105,463	30.0
63		105,593	30.0
65		105,666	30.0
67		105,667	30.0
69		105,676	30.0
71		105,795	30.0
73		105,956	30.0
75		107,367	30.0
77		107,380	30.0
79		107,584	30.0

ACTUALIZACIONES			NOMBRE	
VERSION	MOTIVO	FECHA	REVISADO	ALONSO
3	CONSIGNA	04/07/2016	ELABORADO	MANZANO
4	CONSIGNA	12/02/2018	APROBADO	RINCON
5	CONSIGNA	19/03/2018	L: T-4402-C1	
6	CONSIGNA	05/04/2018	HOJA: 19 de 23	
			NOMBRE DE FICHERO	
			T-4402-C1 AZNALCAZAR P.-HUELVA_V.06	



SUBDIRECCION DE
PROG. DE INSTALACIONES

**AZNALCAZAR PILAS -
HUELVA**

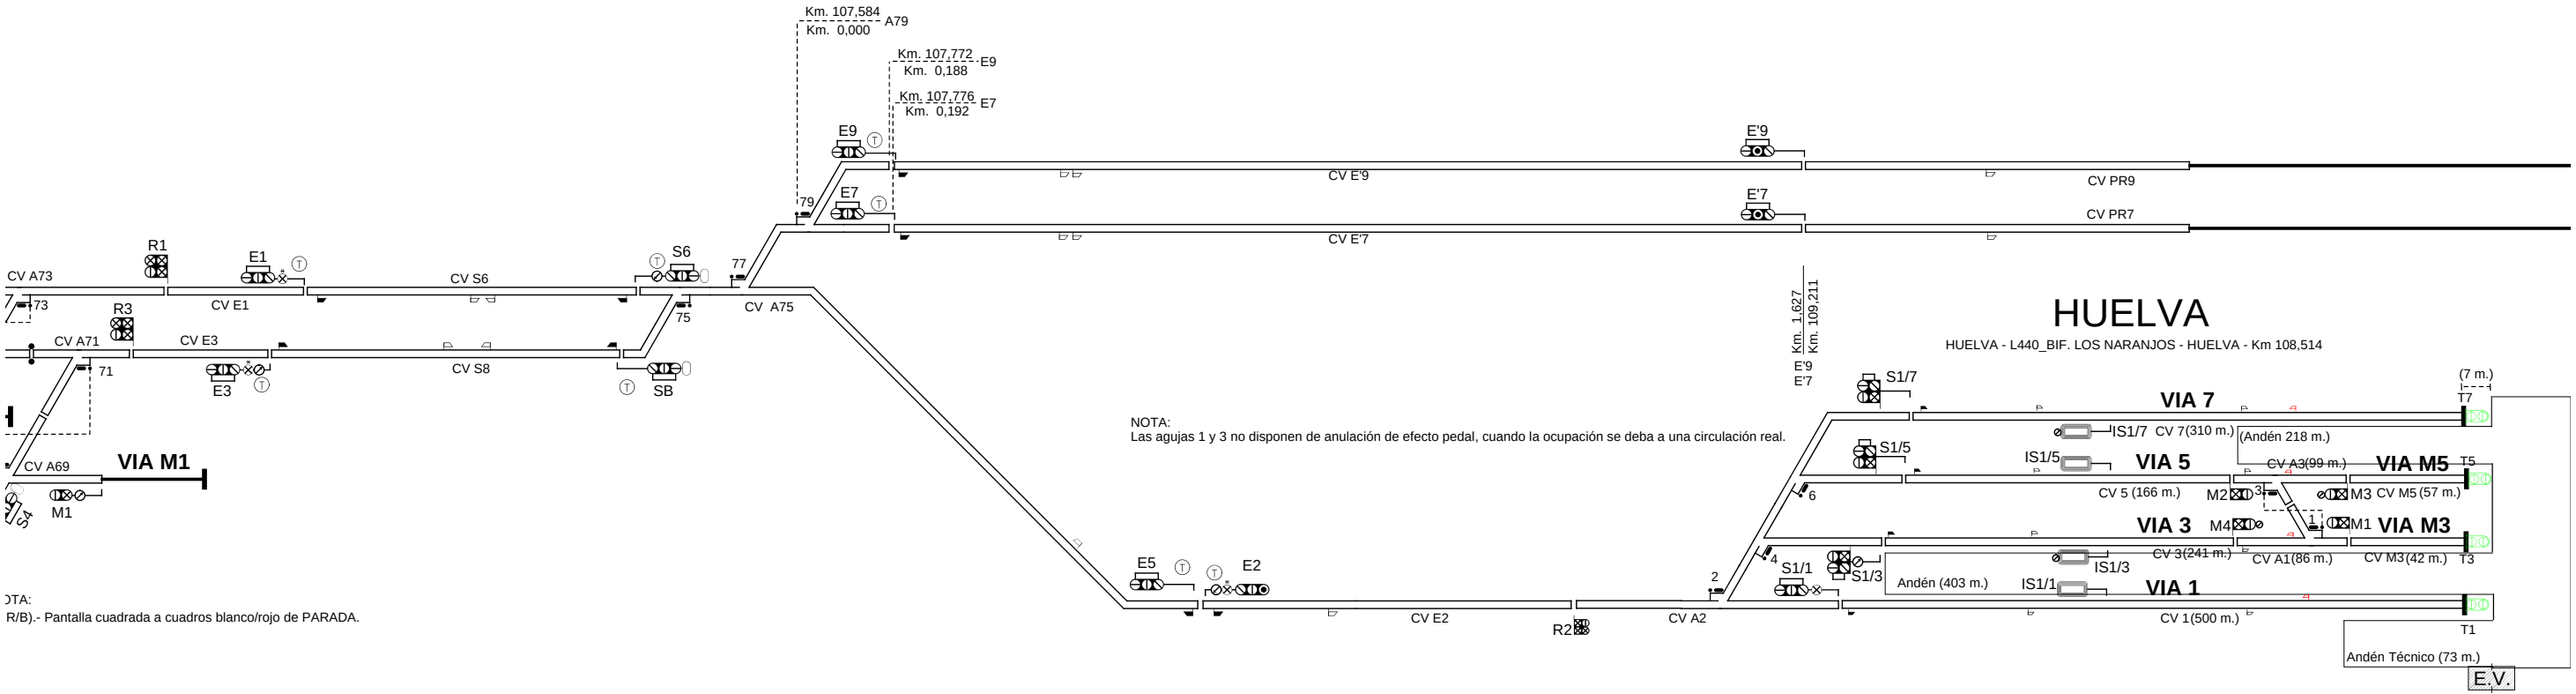

DTA:
R/B).- Pantalla cuadrada a cuadros blanco/rojo de PARADA.

IAVE MANTENIMIENTO

ÍAS Y OBRAS

SEÑALES - HUELVA			
Nombre	P.K.	Nombre	P.K.
S6/8	107,276	IS1/1	108,299
E5	107,653	IS1/3	108,299
E2	107,653	IS1/5	108,299
R2	107,912	IS1/7	108,299
S1/1	108,014	M2	108,358
S1/3	108,145	M4	108,386
S1/5	108,192	M3	108,457
S1/7	108,204	M1	108,472

APARATOS - HUELVA			
Nº	Modelo	P.K. 1	VEL.
2		107,932	60.0
4		108,060	60.0
6		108,110	60.0
3		108,374	50.0
1		108,454	50.0
T7		108,514	
T5		108,514	
T3		108,514	
T1		108,514	

BALIZAS L7 108,444
BALIZAS L7 108,374

ACTUALIZACIONES			NOMBRE	
VERSION	MOTIVO	FECHA	REVISADO	ALONSO
3	CONSIGNA	04/07/2016	ELABORADO	MANZANO
4	CONSIGNA	12/02/2018	APROBADO	RINCON
5	CONSIGNA	19/03/2018	L: T-4402-C1	
6	CONSIGNA	05/04/2018	HOJA: 20 de 23	
			NOMBRE DE FICHERO	
			T-4402-C1 AZNALCAZAR P.-HUELVA_V.06	

 SUBDIRECCION DE
PROG. DE INSTALACIONES

**AZNALCAZAR PILAS -
HUELVA**