


ALCAZAR DE S.J.
160 Km/h

EL CAÑAMO (APD.)
Km 559,191

LA RINCONADA (APD.)
Km 559,912

MAJARABIQUE - (C1) - ESTACION


L400_ALCAZAR S.J.-CADIZ - MAJARABIQUE - Km 563,327

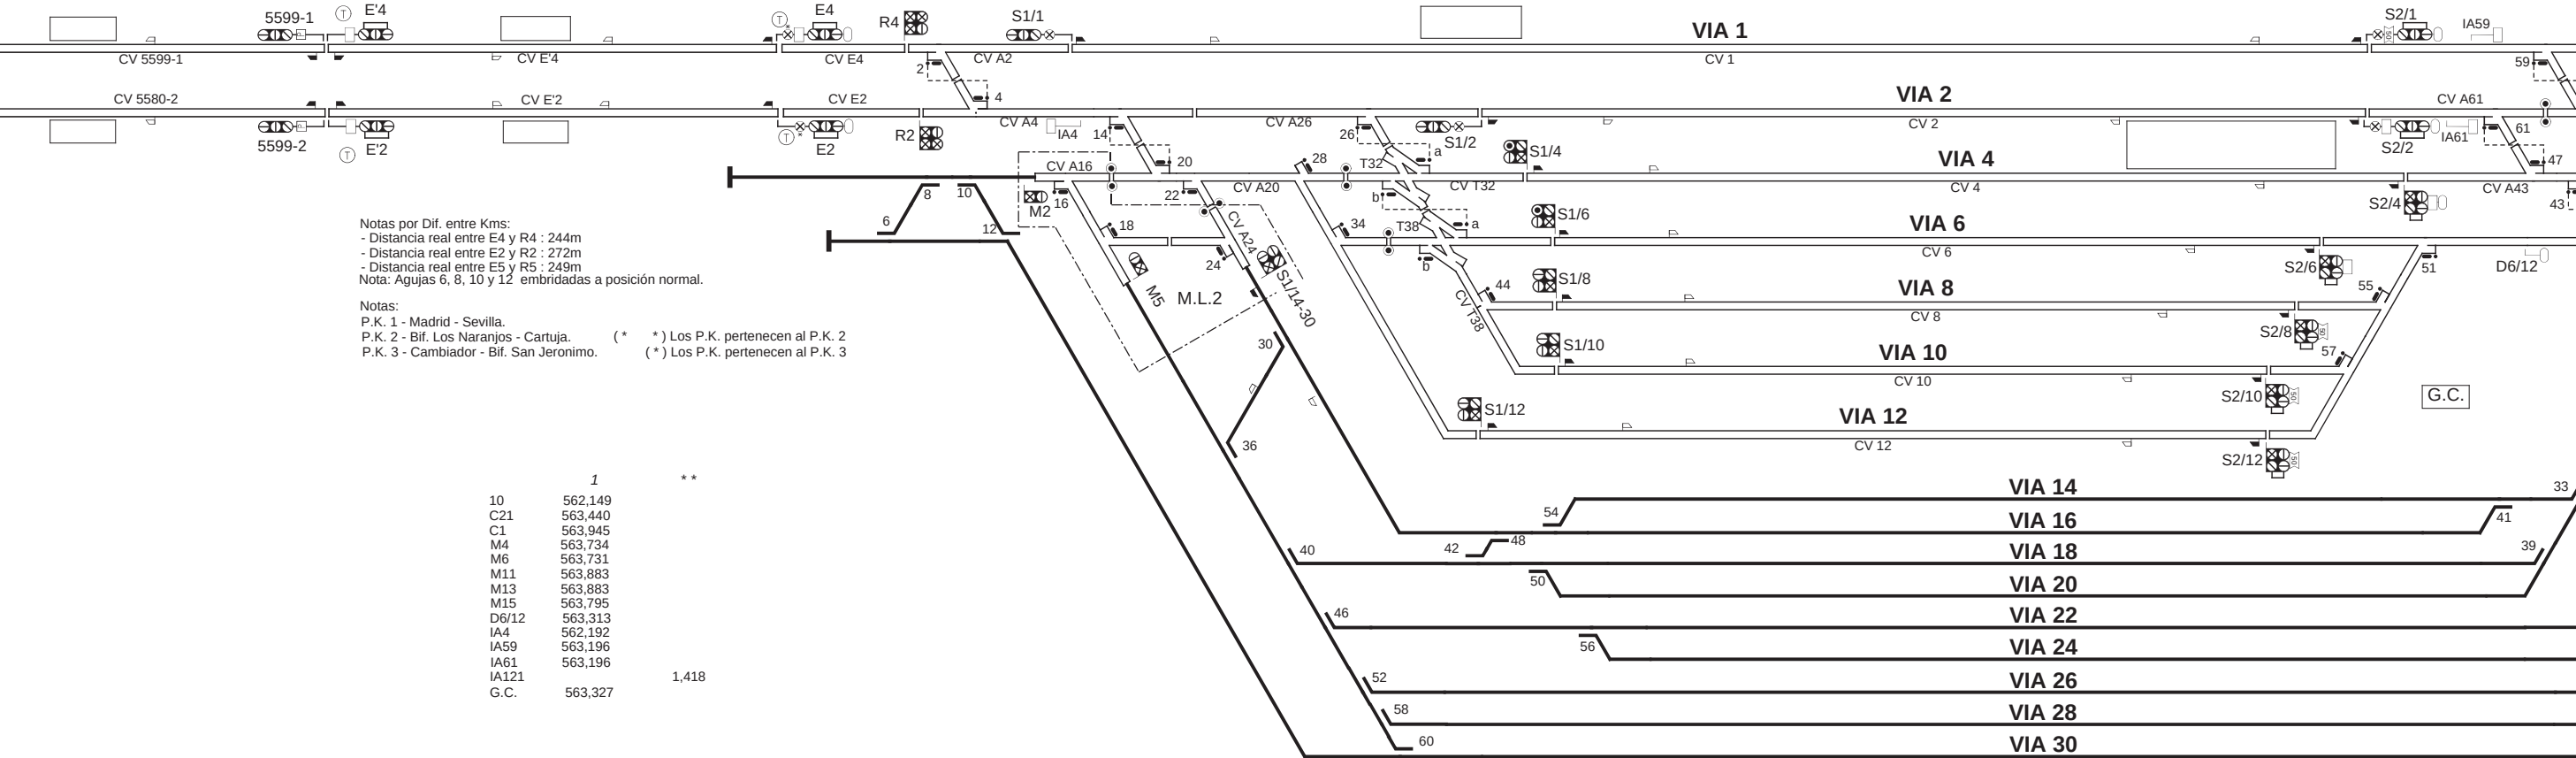

APARATOS - MAJARABIQUE - (C1)														
Nº	Modelo	P.K. 1	P.K. 2	VEL.	Nº	Modelo	P.K. 1	P.K. 2	VEL.	Nº	Modelo	P.K. 1	P.K. 2	VEL.
131		0,844	0,844 *	30.0	53		563,288		50.0	7		563,658		30.0
TOP M7		0,955	0,955 *		51		563,304		30.0	TOP M3		563,697		
123		1,276	*1,276 *	60.0	49		563,311		30.0	3		563,722		30.0
121		1,367	*1,367 *	60.0	47		563,317		30.0	119		563,789	0,140 *	30.0
2		562,024		50.0	43		563,345		30.0	117		563,796	0,146 *	30.0
4		562,095		50.0	C31		563,394			1		563,888		30.0
14		562,196		50.0	31		563,400		30.0	115		564,555		50.0
16		562,199		30.0	27		563,424		30.0	C115		564,616		
18		562,240		30.0	25		563,431		30.0	113		564,667		50.0
20		562,274		30.0	T23		563,452		30.0	TOP M9		564,670		
22		562,283		30.0			563,478			111		564,689		50.0
24		562,354		30.0	T21		563,471		30.0	109		564,761		50.0
26		562,393		50.0			563,496			129		564,805		50.0
28		562,422		30.0	T19		563,498		30.0	127		564,852	1,287 *	50.0
34		562,467		30.0			563,524			107		564,882	*0,146 *	60.0
T32		562,495		30.0	T17		563,516		30.0	105		564,889	*0,139 *	60.0
		562,469					563,542			125	1,377 *	564,943	*1,162 *	50.0
T38		562,539		30.0	C3		563,526			103		564,979	*0,049 *	60.0
		562,515			T15		563,562		30.0	101		565,028	*0,000 *	60.0
44		562,559		30.0			563,588			CAMB.		563,649	0,000 *	
61		563,204		30.0	13		563,594		30.0	6		562,082		
57		563,211		30.0	11		563,594		30.0	8		562,149		
59		563,216		50.0	9		563,658		30.0	C131			0,905 *	
55		563,257		30.0	5		563,658		30.0	C21		563,440		

SENALES - MAJARABIQUE - (C1)							
Nombre	P.K.	Nombre	P.K.	Nombre	P.K.	Nombre	P.K.
M6	0,082 *	E'2	559,851	S2/10	563,147	E1	563,974
M4	0,085 *	E'4	559,851	S2/2	563,192	E22	564,233
M15	0,146 *	5599-2	559,871	S2/1	563,193	E24	564,355
M11	0,244 *	5599-1	559,871	IA59	563,196	E16	564,490
M13	0,251 *	E'2	561,777	IA61	563,196	E14	564,490
E18	*0,337 *	E4	561,777	S2/8	563,196	E26	564,532
E20	*0,337 *	R4	561,994	S2/6	563,236	M9	564,619
E28	0,824 *	R2	562,022	S2/4	563,244	IA105	564,885
M7	0,909 *	S1/1	562,106	D6/12	563,313	IA107	564,886
E12	*0,944 *	IA4	562,192	S2/14-20	563,392	IA103	565,028
E10	*0,944 *	M2	562,195	S2/22-30	563,438	IA101	565,094
IA123	*1,189 *	M5	562,298	M3	563,528	E11	565,275
IA125	*1,251 *	S1/14-30	562,371	R15	563,572	E13	565,275
IA121	*1,418 *	S1/2	562,476	R5	563,632	E'2BT	565,614
E9	*1,603 *	S1/4	562,525	R3	563,725	E'4BT	565,614
E7	*1,641 *	S1/12	562,530	R1	563,745	E'13	566,315
E'6	*2,671 *	S1/6	562,571	E5	563,908	E'11	566,315
E'8	*2,671 *	S1/8	562,622	M1	563,950		
E'7	*2,974 *	S1/10	562,625	E15	563,960		
E'9	*2,992 *	S2/12	563,146	E3	563,974		

ACTUALIZACIONES				NOMBRE	
VERSION	MOTIVO	FECHA	ELABORADO	REVISADO	ALONSO
1	CONSIGNA	21/08/2018	I. PEÑA	ELABORADO	I. PEÑA
2	CONSIGNA	11/02/2020	I. PEÑA	APROBADO	J. A. DELGADO
				T-40008-C1-50709	
				HOJA: 1 de 2	
				NOMBRE DE FICHERO	
				T-40008-C1 MAJARABIQUE_V.02	

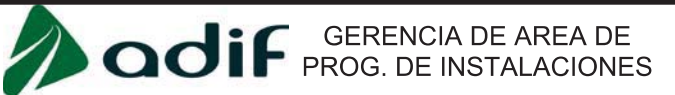

MAJARABIQUE

