


SALTERAS - (C1)

SALTERAS - (C1) - L440_BIF. LOS NARANJOS - HUELVA - Km 12,881

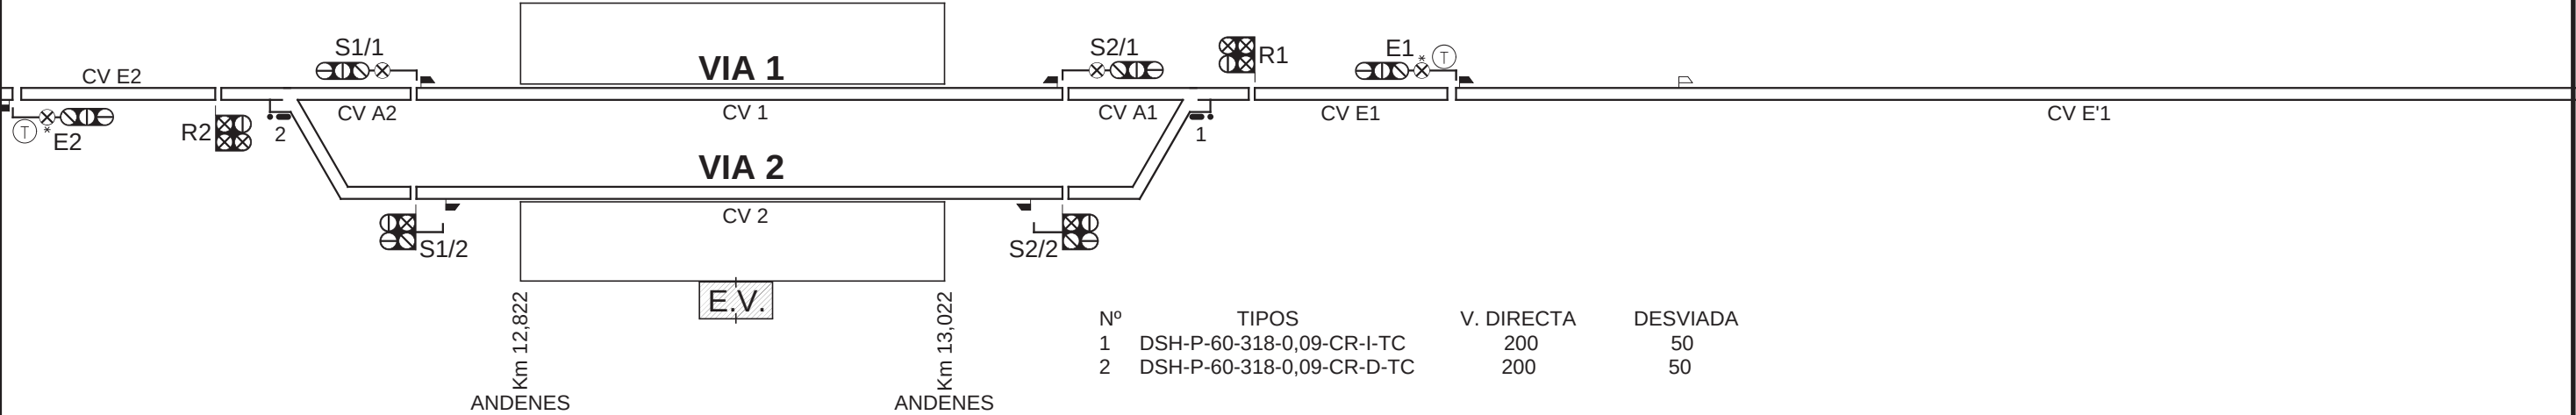

APARATOS - SALTERAS - (C1)			
Nº	Modelo	P.K. 1	VEL.
2		12,745	50.0
1		13,101	50.0

SEÑALES - SALTERAS - (C1)			
Nombre	P.K.	Nombre	P.K.
E'2	10,615	S2/1	13,030
E'1V	10,633	S2/2	13,030
E2	12,450	R1	13,121
R2	12,725	E1	13,371
S1/1	12,815	E'2V	16,188
S1/2	12,815	E'1	16,206

ACTUALIZACIONES			NOMBRE	
VERSION	MOTIVO	FECHA	REVISADO	ALONSO
1	CONSIGNA	12/08/2019	ELABORADO	I. PEÑA
			APROBADO	J. A. DELGADO
			T-4401-C1	
			HOJA:	6 de 17
			NOMBRE DE FICHERO	
			T-4401-C1 BIF.CARTUJA-AZNALCAZAR-PILAS_V.01	



GERENCIA DE AREA DE
PROG. DE INSTALACIONES

BIF. CARTUJA -
AZNALCAZAR-PILAS