


SAN JUAN DEL PUERTO-MOGUER

SAN JUAN DEL PUERTO-MOGUER - L440\_BIF. LOS NARANJOS - HUELVA - Km 96,650

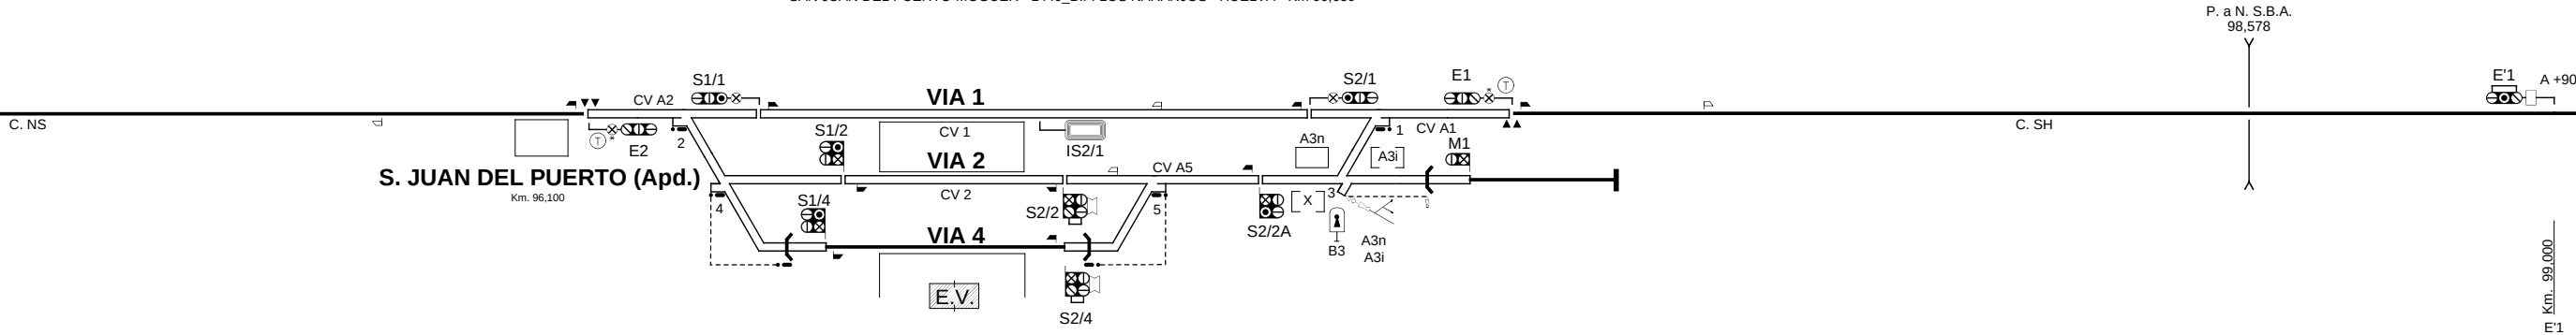

| SEÑALES - SAN JUAN DEL PUERTO-MOGUER |        |        |        |
|--------------------------------------|--------|--------|--------|
| Nombre                               | P.K.   | Nombre | P.K.   |
| E'2                                  | 94,592 | S2/4   | 96,873 |
| E2                                   | 96,255 | S2/2A  | 97,214 |
| S1/1                                 | 96,405 | M1     | 97,291 |
| S1/4                                 | 96,425 | S2/1   | 97,306 |
| S1/2                                 | 96,431 | E1     | 97,435 |
| IS2/1                                | 96,753 | E'1    | 99,000 |
| S2/2                                 | 96,873 |        |        |

| APARATOS - SAN JUAN DEL PUERTO-MOGUER |        |        |      |
|---------------------------------------|--------|--------|------|
| Nº                                    | Modelo | P.K. 1 | VEL. |
| 2                                     |        | 96,310 | 30.0 |
| 4                                     |        | 96,358 | 50.0 |
| 5                                     |        | 96,949 | 30.0 |
| 3                                     |        | 97,230 | 30.0 |
| 1                                     |        | 97,375 | 50.0 |

| ACTUALIZACIONES |          |            | NOMBRE                              |         |
|-----------------|----------|------------|-------------------------------------|---------|
| VERSION         | MOTIVO   | FECHA      | REVISADO                            | ALONSO  |
| 3               | CONSIGNA | 04/07/2016 | ELABORADO                           | MANZANO |
| 4               | CONSIGNA | 12/02/2018 | APROBADO                            | RINCON  |
| 5               | CONSIGNA | 19/03/2018 | L: T-4402-C1                        |         |
| 6               | CONSIGNA | 05/04/2018 | HOJA: 17 de 23                      |         |
|                 |          |            | NOMBRE DE FICHERO                   |         |
|                 |          |            | T-4402-C1 AZNALCAZAR P.-HUELVA_V.06 |         |

 SUBDIRECCION DE  
PROG. DE INSTALACIONES

**AZNALCAZAR PILAS -  
HUELVA**