

N. - S.L.A.
ASE " B "
h 16,660


CAMINO DE LOS GRANADILLOS

P. a N. - S.L.A.
CLASE " B "
Km 17,961

CAMINO DE VILLANUEVA
A OLIVARES

VILLANUEVA DEL AR

VILLANUEVA DEL AR-OL - (C1) - L440_BIF. LOS NARANJO

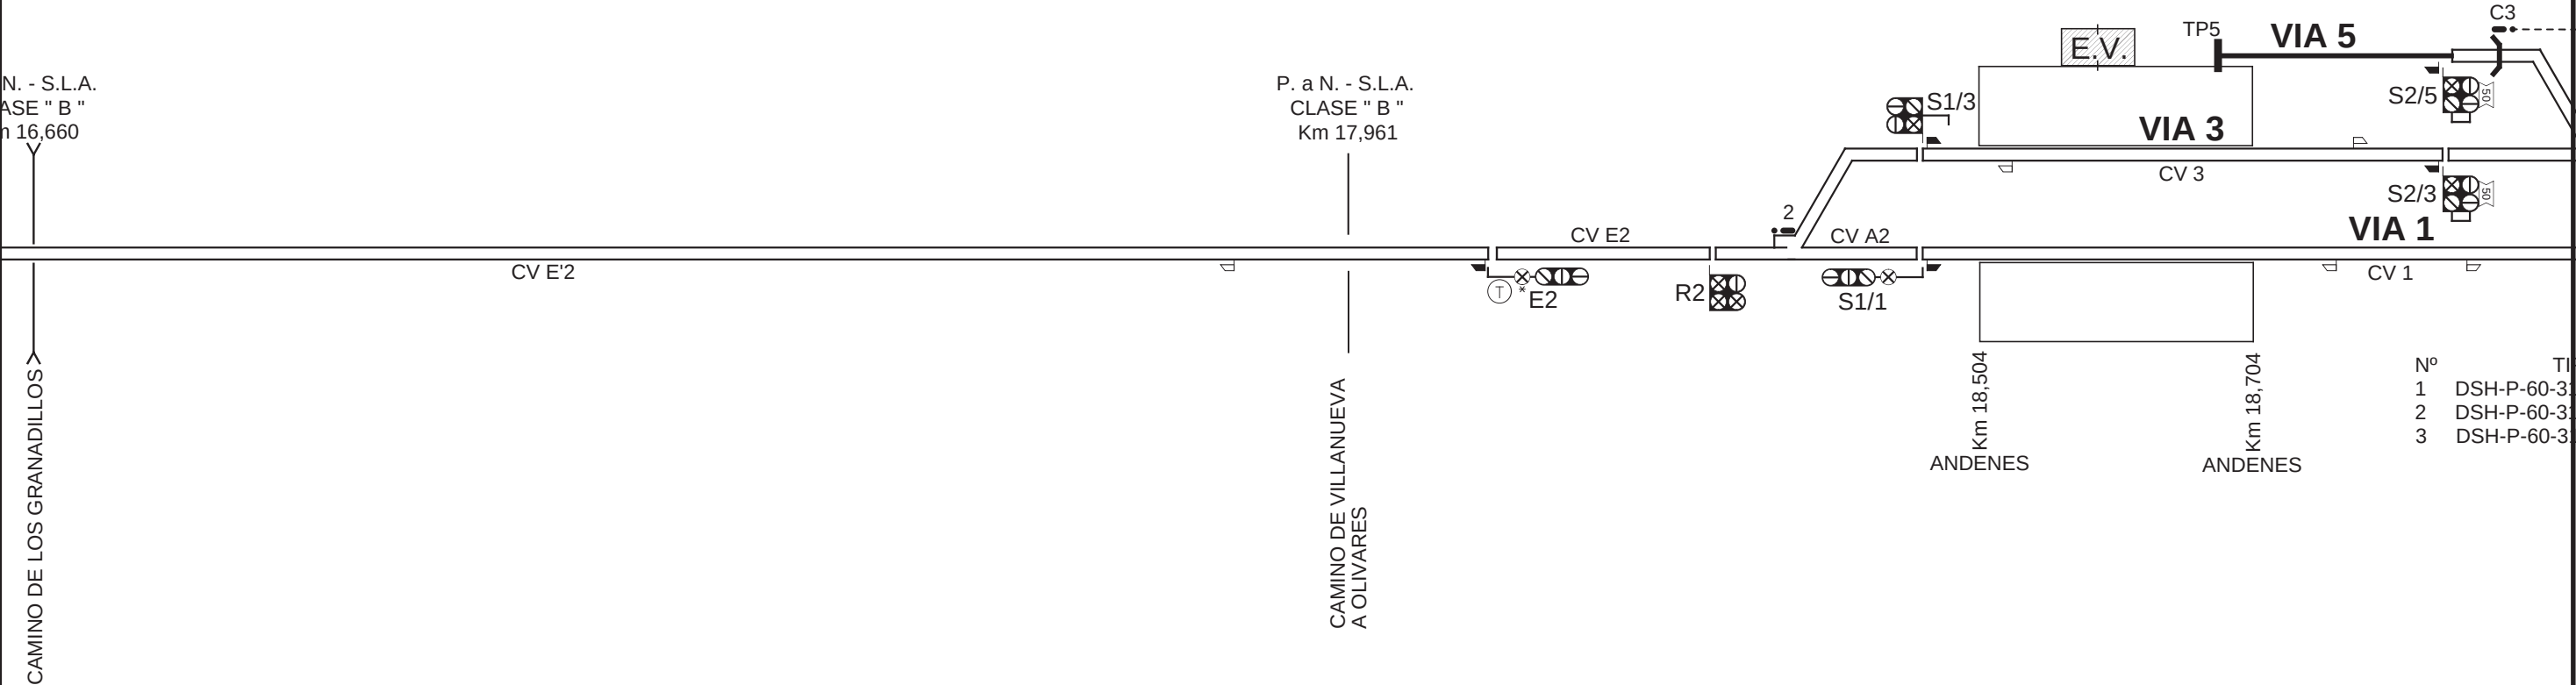

APARATOS - VILLANUEVA DEL AR-OL - (C1)			
Nº	Modelo	P.K. 1	VEL.
2		18,403	50.0
TP5		18,610	
3		18,795	50.0
1		19,148	50.0

SEÑALES - VILLANUEVA DEL AR-OL - (C1)					
Nombre	P.K.	Nombre	P.K.	Nombre	P.K.
E'2	16,188	S1/3	18,498	R1	19,168
E'1	16,206	S2/5	18,731	E1	19,428
E2	18,128	S2/3	18,731	212	21,202
R2	18,383	S2/1	19,068	E'1	21,220
S1/1	18,498	S2/3A	19,068		

ACTUALIZACIONES			NOMBRE	
VERSION	MOTIVO	FECHA	REVISADO	ALONSO
1	CONSIGNA	12/08/2019	ELABORADO	I. PEÑA
			APROBADO	J. A. DELGADO
			T-4401-C1	
			HOJA:	8 de 17
			NOMBRE DE FICHERO	
			T-4401-C1 BIF.CARTUJA-AZNALCAZAR-PILAS_V.01	




GERENCIA DE AREA DE
PROG. DE INSTALACIONES

BIF. CARTUJA -
AZNALCAZAR-PILAS

DEL AR-OL - (C1)

440_BIF. LOS NARANJOS - HUELVA - Km 18,576

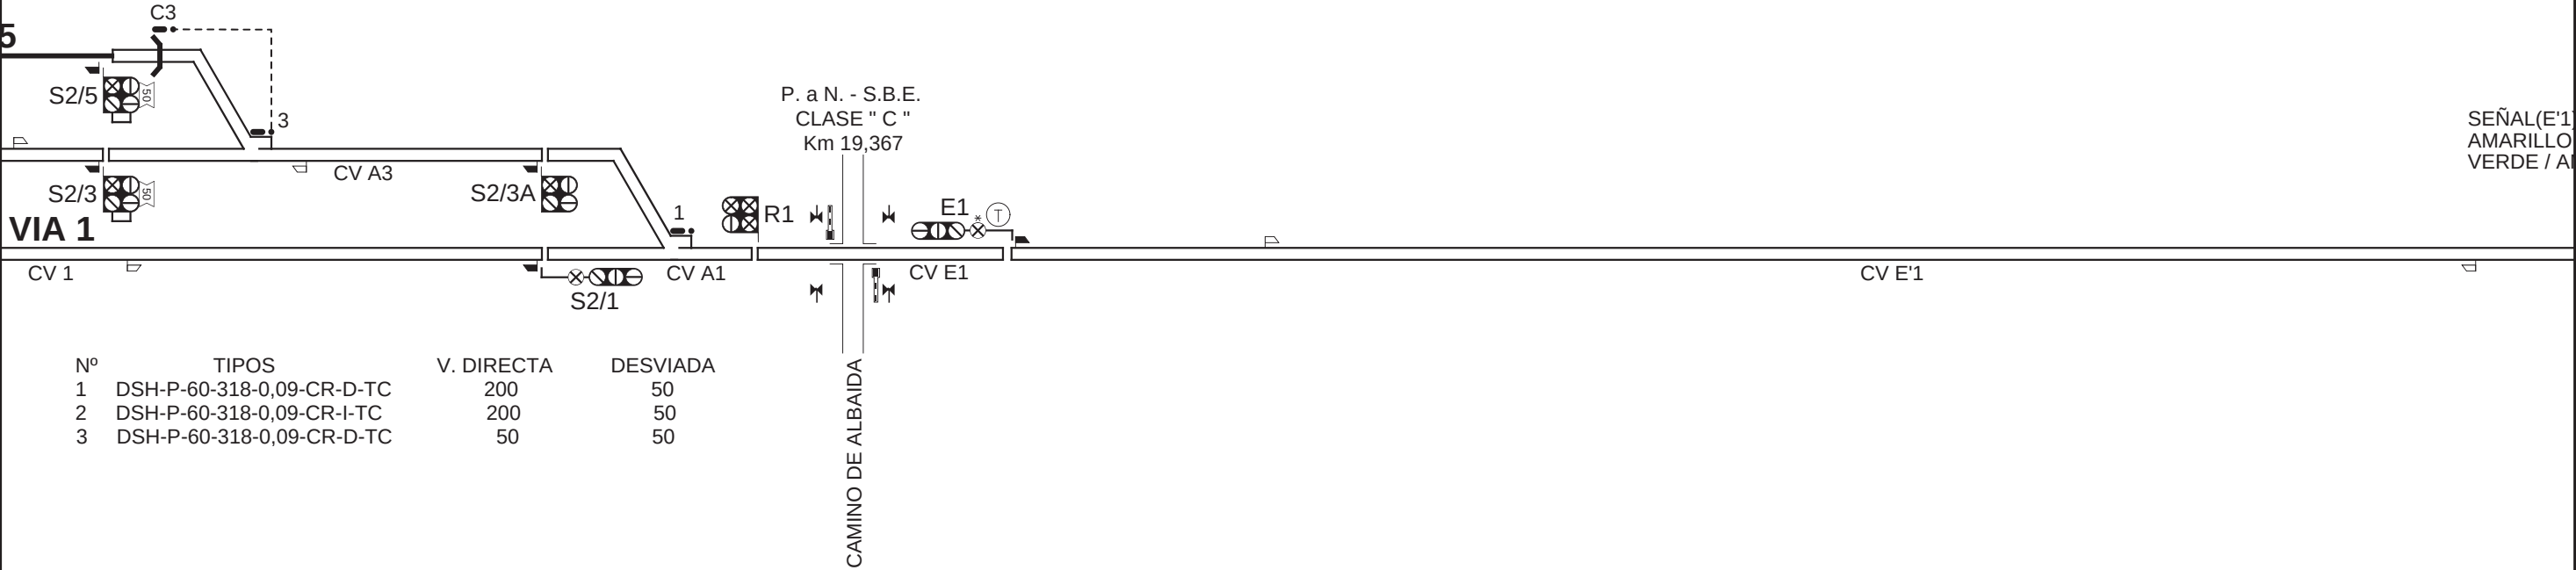

Nº	TIPOS	V. DIRECTA	DESVIADA
1	DSH-P-60-318-0,09-CR-D-TC	200	50
2	DSH-P-60-318-0,09-CR-I-TC	200	50
3	DSH-P-60-318-0,09-CR-D-TC	50	50

ACTUALIZACIONES			NOMBRE	
VERSION	MOTIVO	FECHA	REVISADO	ALONSO
1	CONSIGNA	12/08/2019	ELABORADO	I. PEÑA
			APROBADO	J. A. DELGADO
			T-4401-C1	
			HOJA: 9 de 17	
			NOMBRE DE FICHERO	
			T-4401-C1 BIF.CARTUJA-AZNALCAZAR-PILAS_V.01	



GERENCIA DE AREA DE
PROG. DE INSTALACIONES

BIF. CARTUJA -
AZNALCAZAR-PILAS