


AGUJAS	P.K.
2	515/510
4	515/620
6	515/713
8	515/745
10	515/820
12	515/781
14	515/819
16	515/853

SEÑALES	P.K.
E2	515/472
E1	516/444
E5	516/675

AGUJAS	P.K.
7	516/249
5	516/308
3	516/329
1	516/393

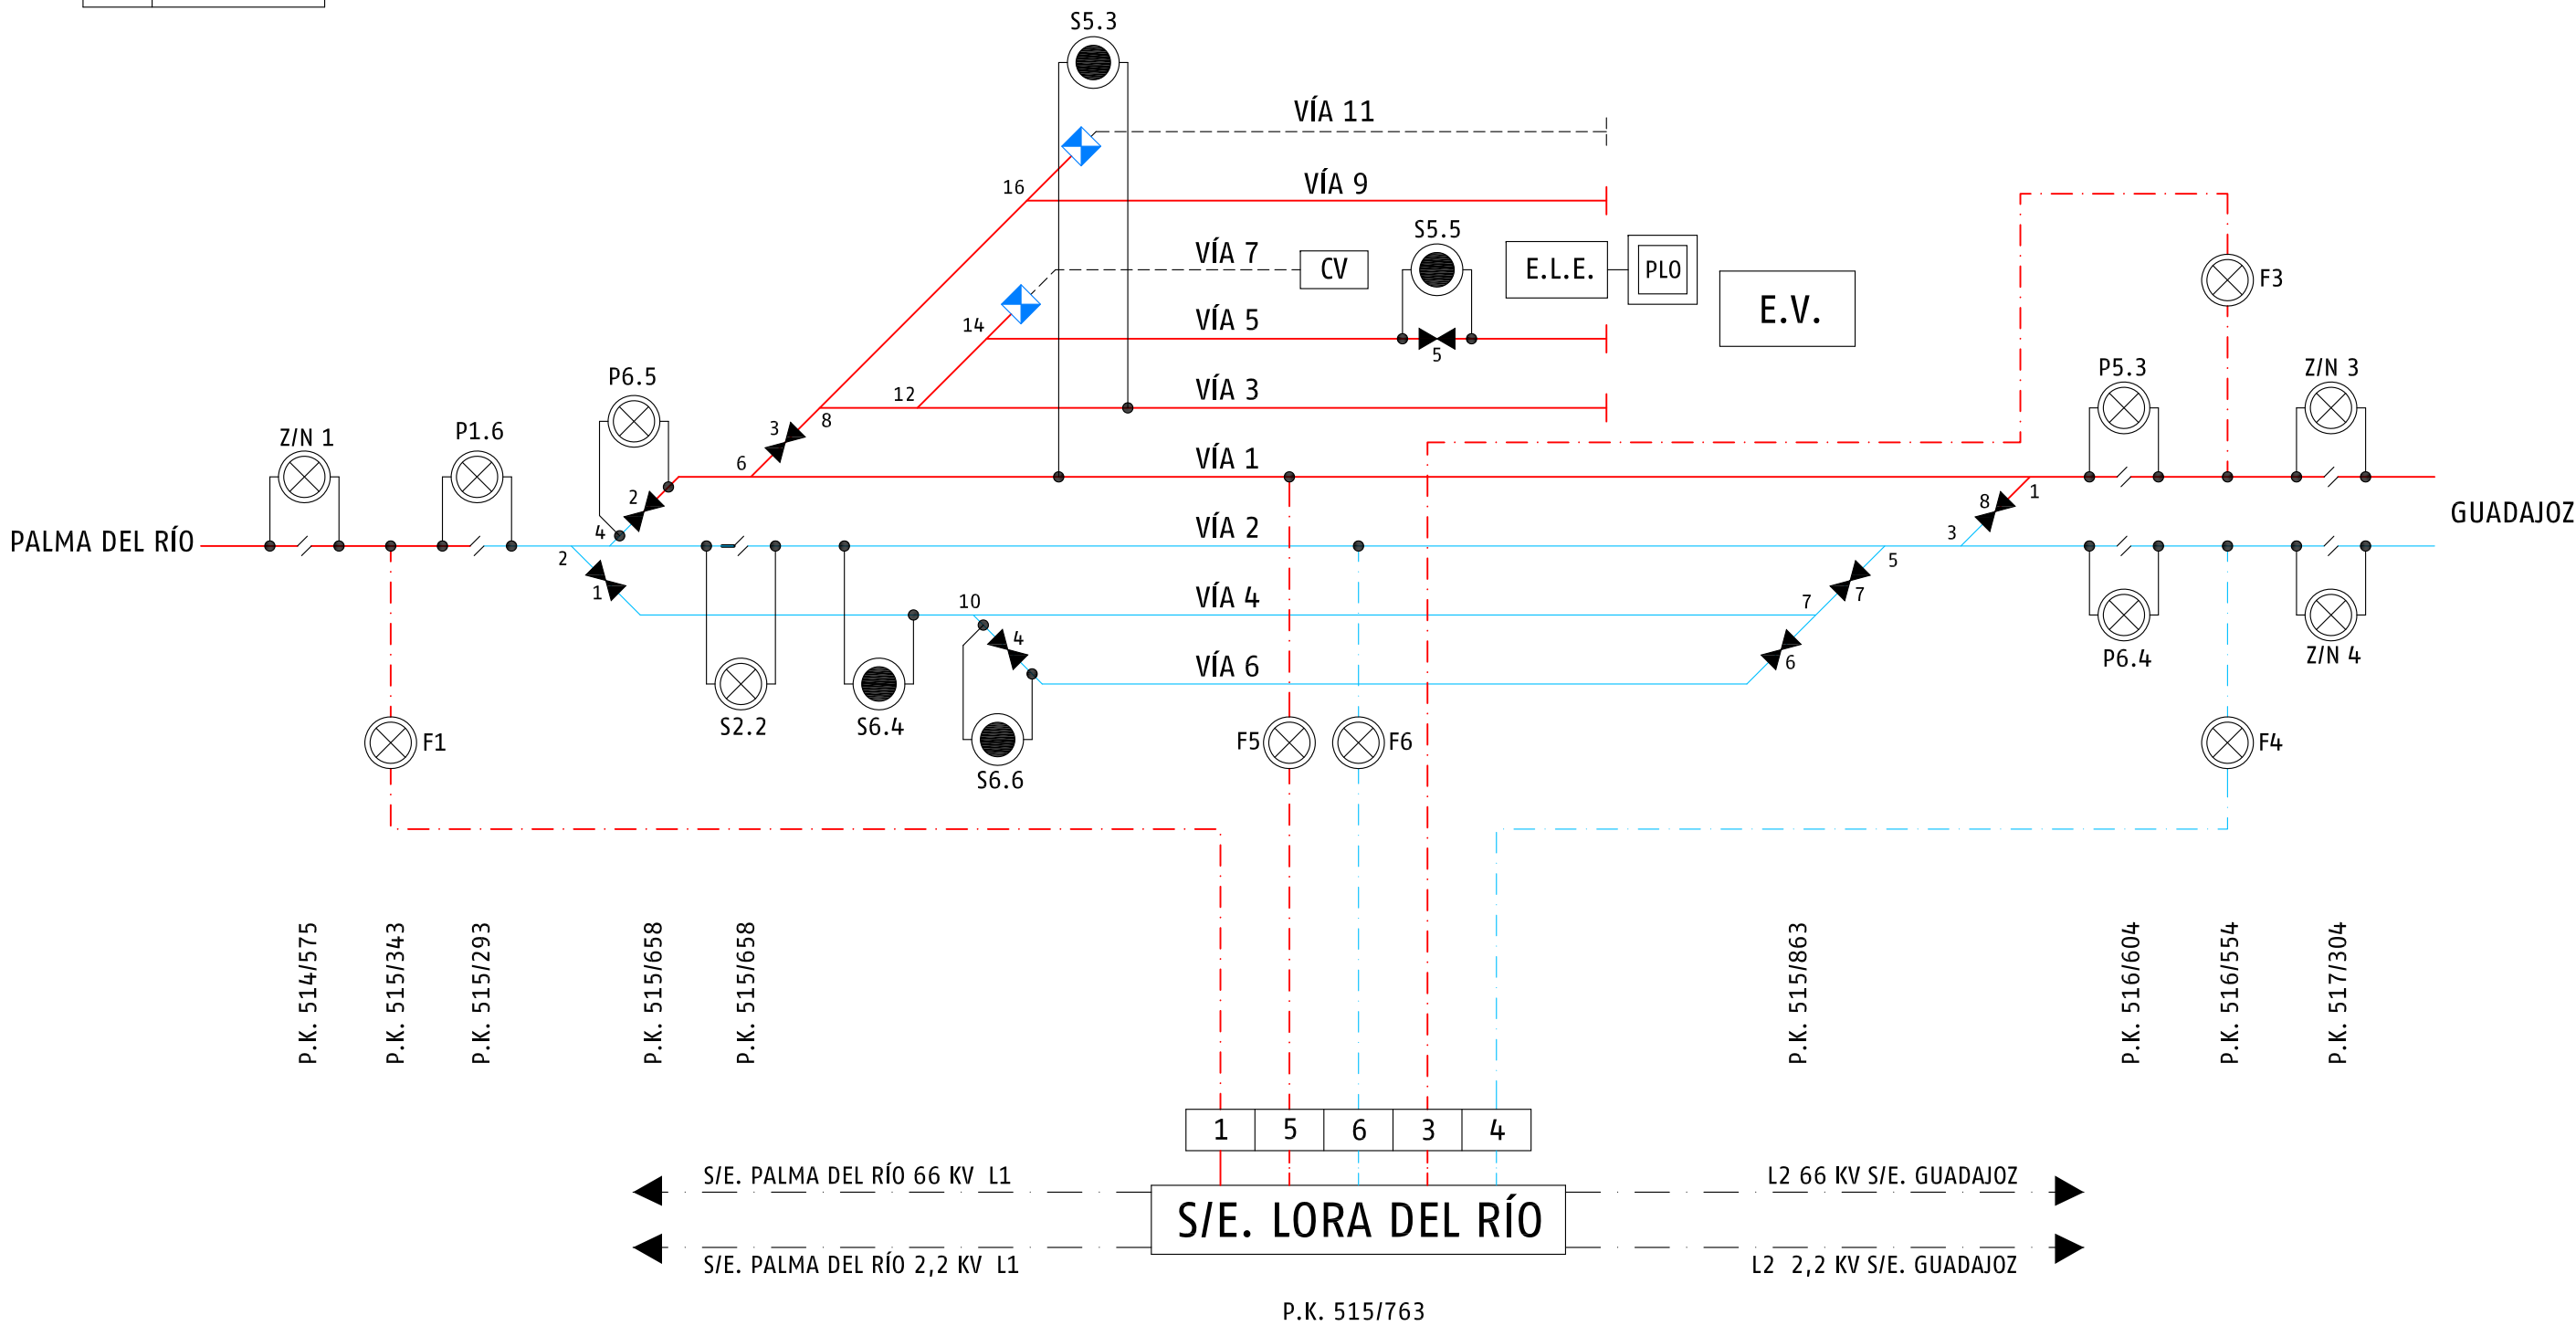

SUBDIRECCIÓN DE OPERACIONES
RED CONVENCIONAL SUR
JEFATURA DE ÁREA DE
MANTENIMIENTO DE SEVILLA

Dibujado por: J.G.J.
Aprobado por: Jose Angel Gomez Flores
Firma: Jose Angel Gomez Flores
Fecha: 19-JULIO-2024

ESQUEMA ELÉCTRICO L.A.C.
P.E. 17 LÍNEA DE MADRID A SEVILLA
LORA DEL RÍO

Plano nº 1 de 1
Sustituye a: Hoja 2 de 8 de 26/11/15
Hoja nº 2 de 11