


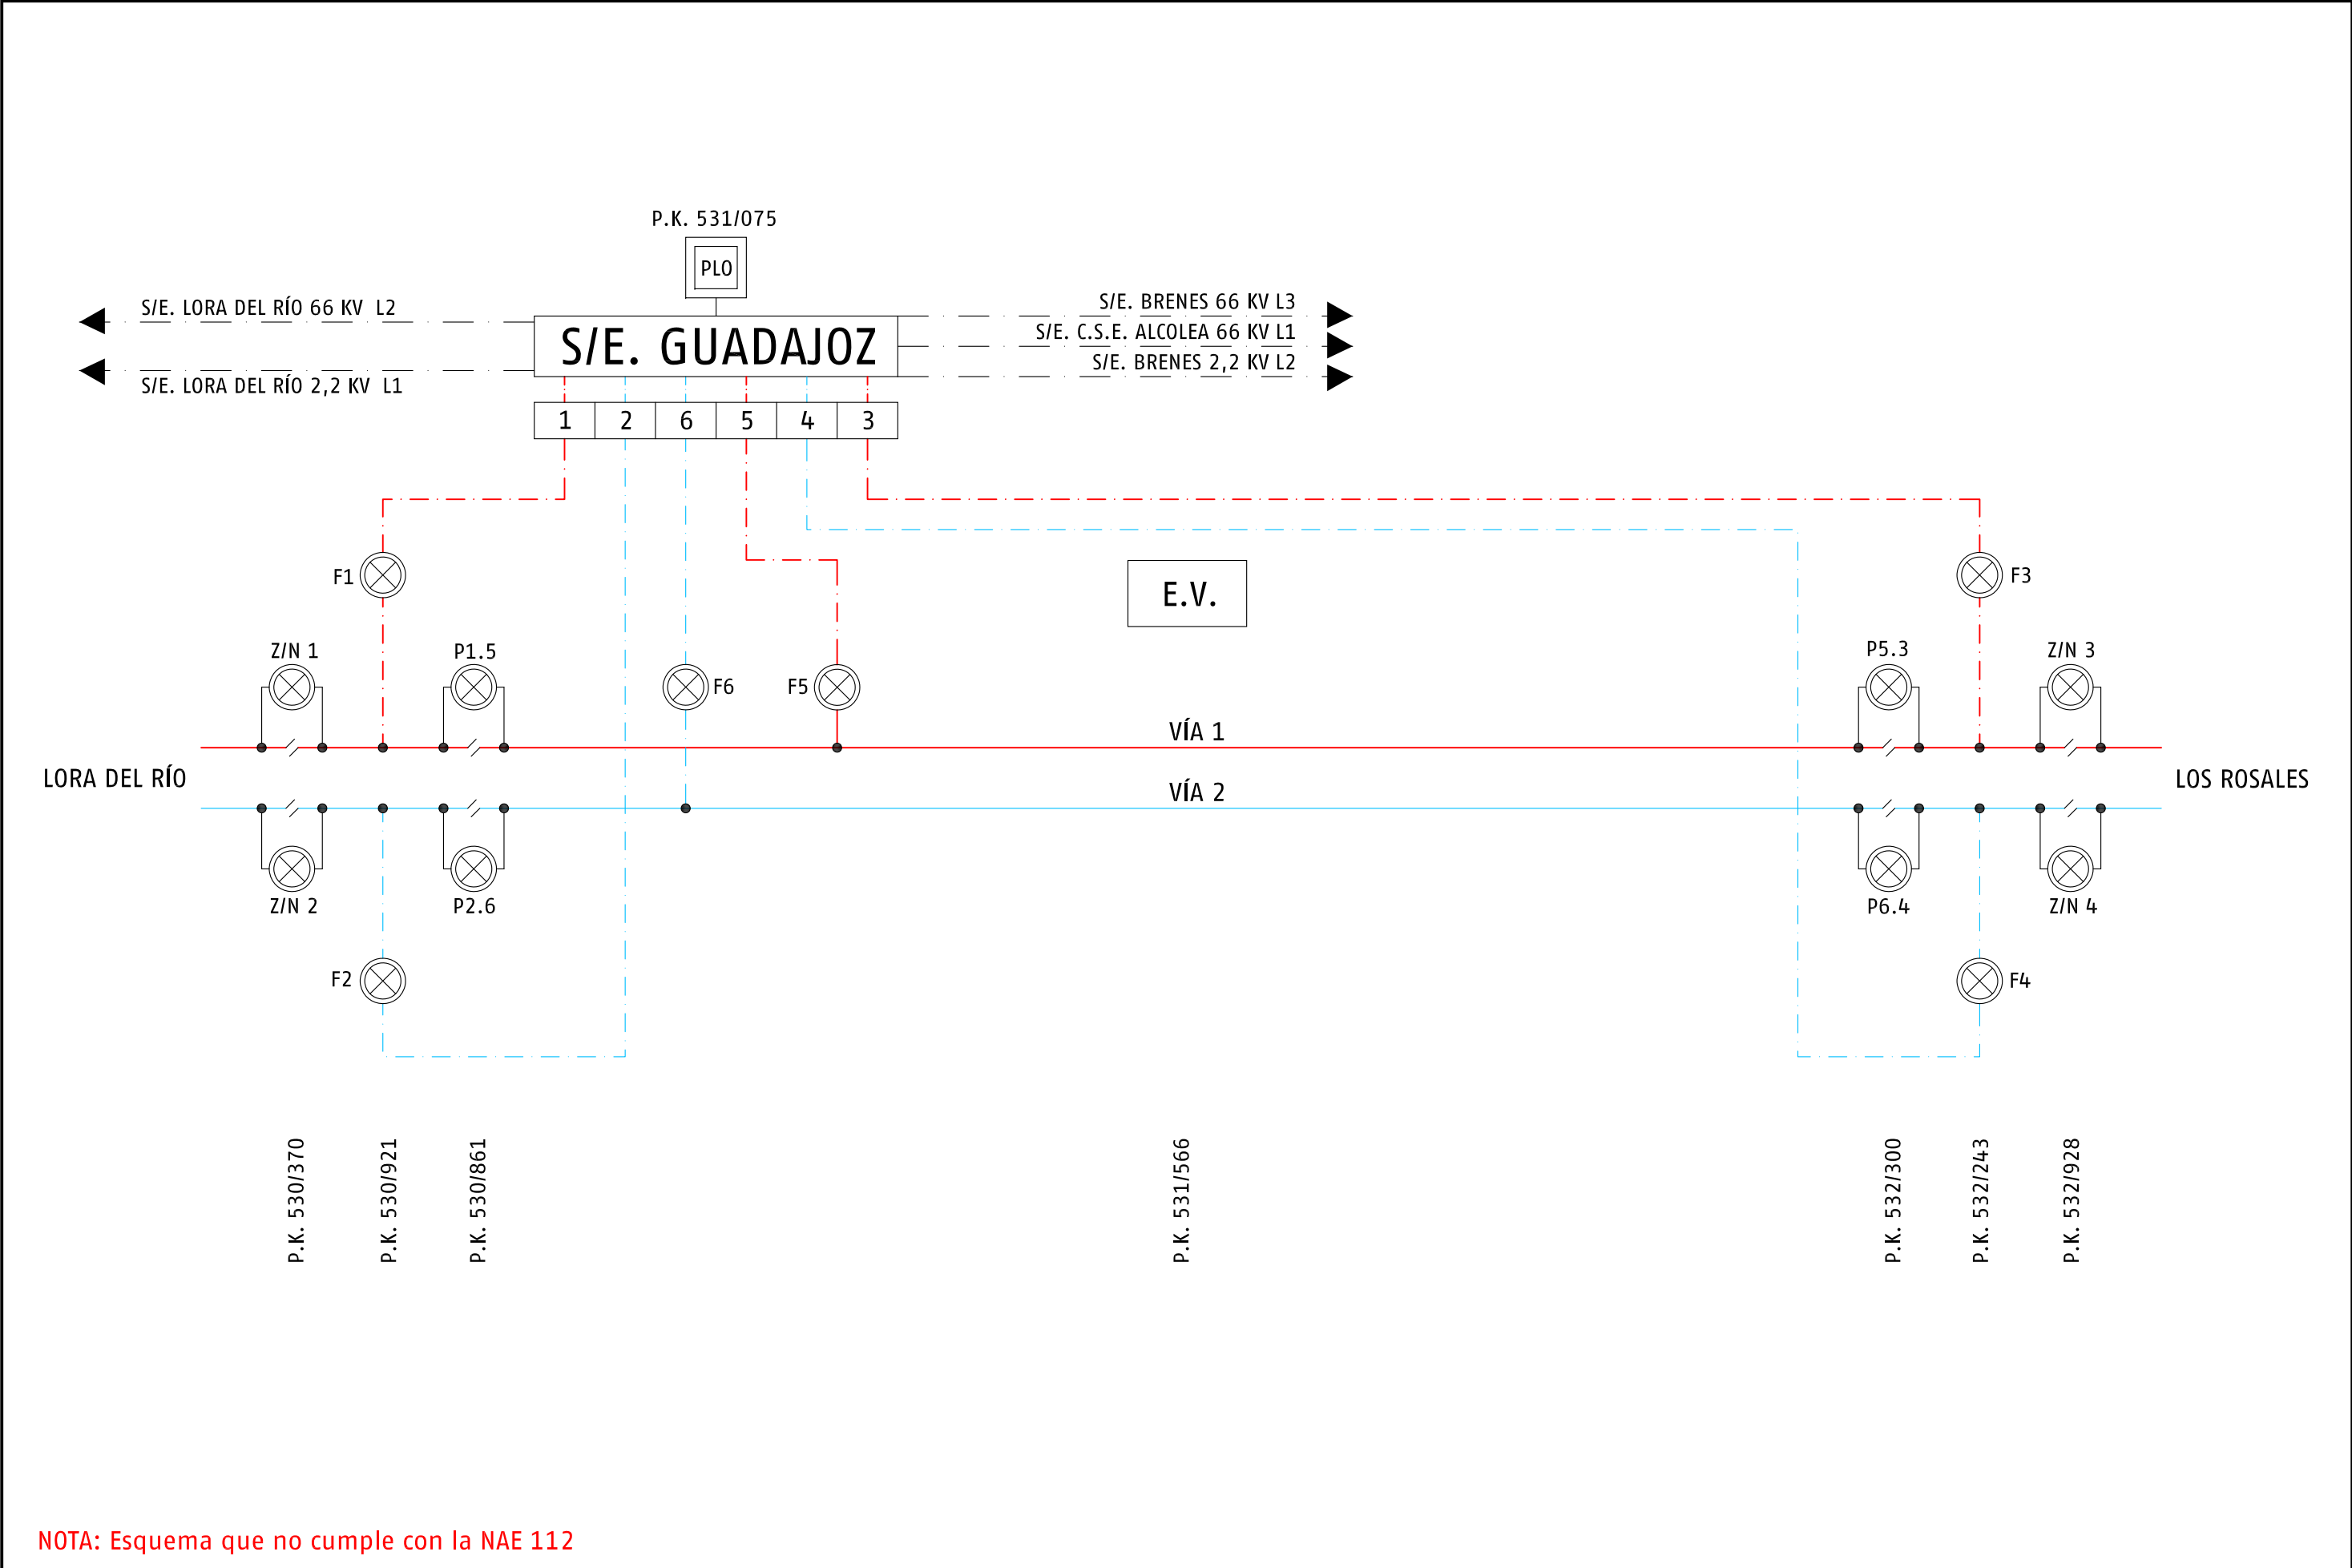

NOTA: Esquema que no cumple con la NAE 112

	SUBDIRECCIÓN DE OPERACIONES RED CONVENCIONAL SUR JEFATURA DE ÁREA DE MANTENIMIENTO DE SEVILLA	Dibujado por: J.G.J.	ESQUEMA ELÉCTRICO L.A.C. P.E. 17 LÍNEA DE MADRID A SEVILLA GUADAJÓZ	Plano nº 1 de 1
		Aprobado por: Jose Angel Gomez Flores Firma:  Fecha: 2024.07.19 11:19:16 +02'00'		Sustituye a: Hoja 3 de 8 de 26/11/15
		Fecha: 19-JULIO-2024		Hoja nº 3 de 11