


| AGUJAS | P.K.    |
|--------|---------|
| 2      | 549/732 |
| 4      | 549/810 |
| 6      | 549/850 |
| 8      | 550/108 |
| 10     | 550/050 |
| 12     | 549/900 |
| 14     | 550/000 |

| SEÑALES | P.K.    |
|---------|---------|
| E2      | 549/407 |
| E4      | 549/407 |
| E1      | 550/916 |
| E3      | 550/916 |

| AGUJAS | P.K.    |
|--------|---------|
| 1      | 550/662 |
| 3      | 550/590 |
| 5      | 550/560 |

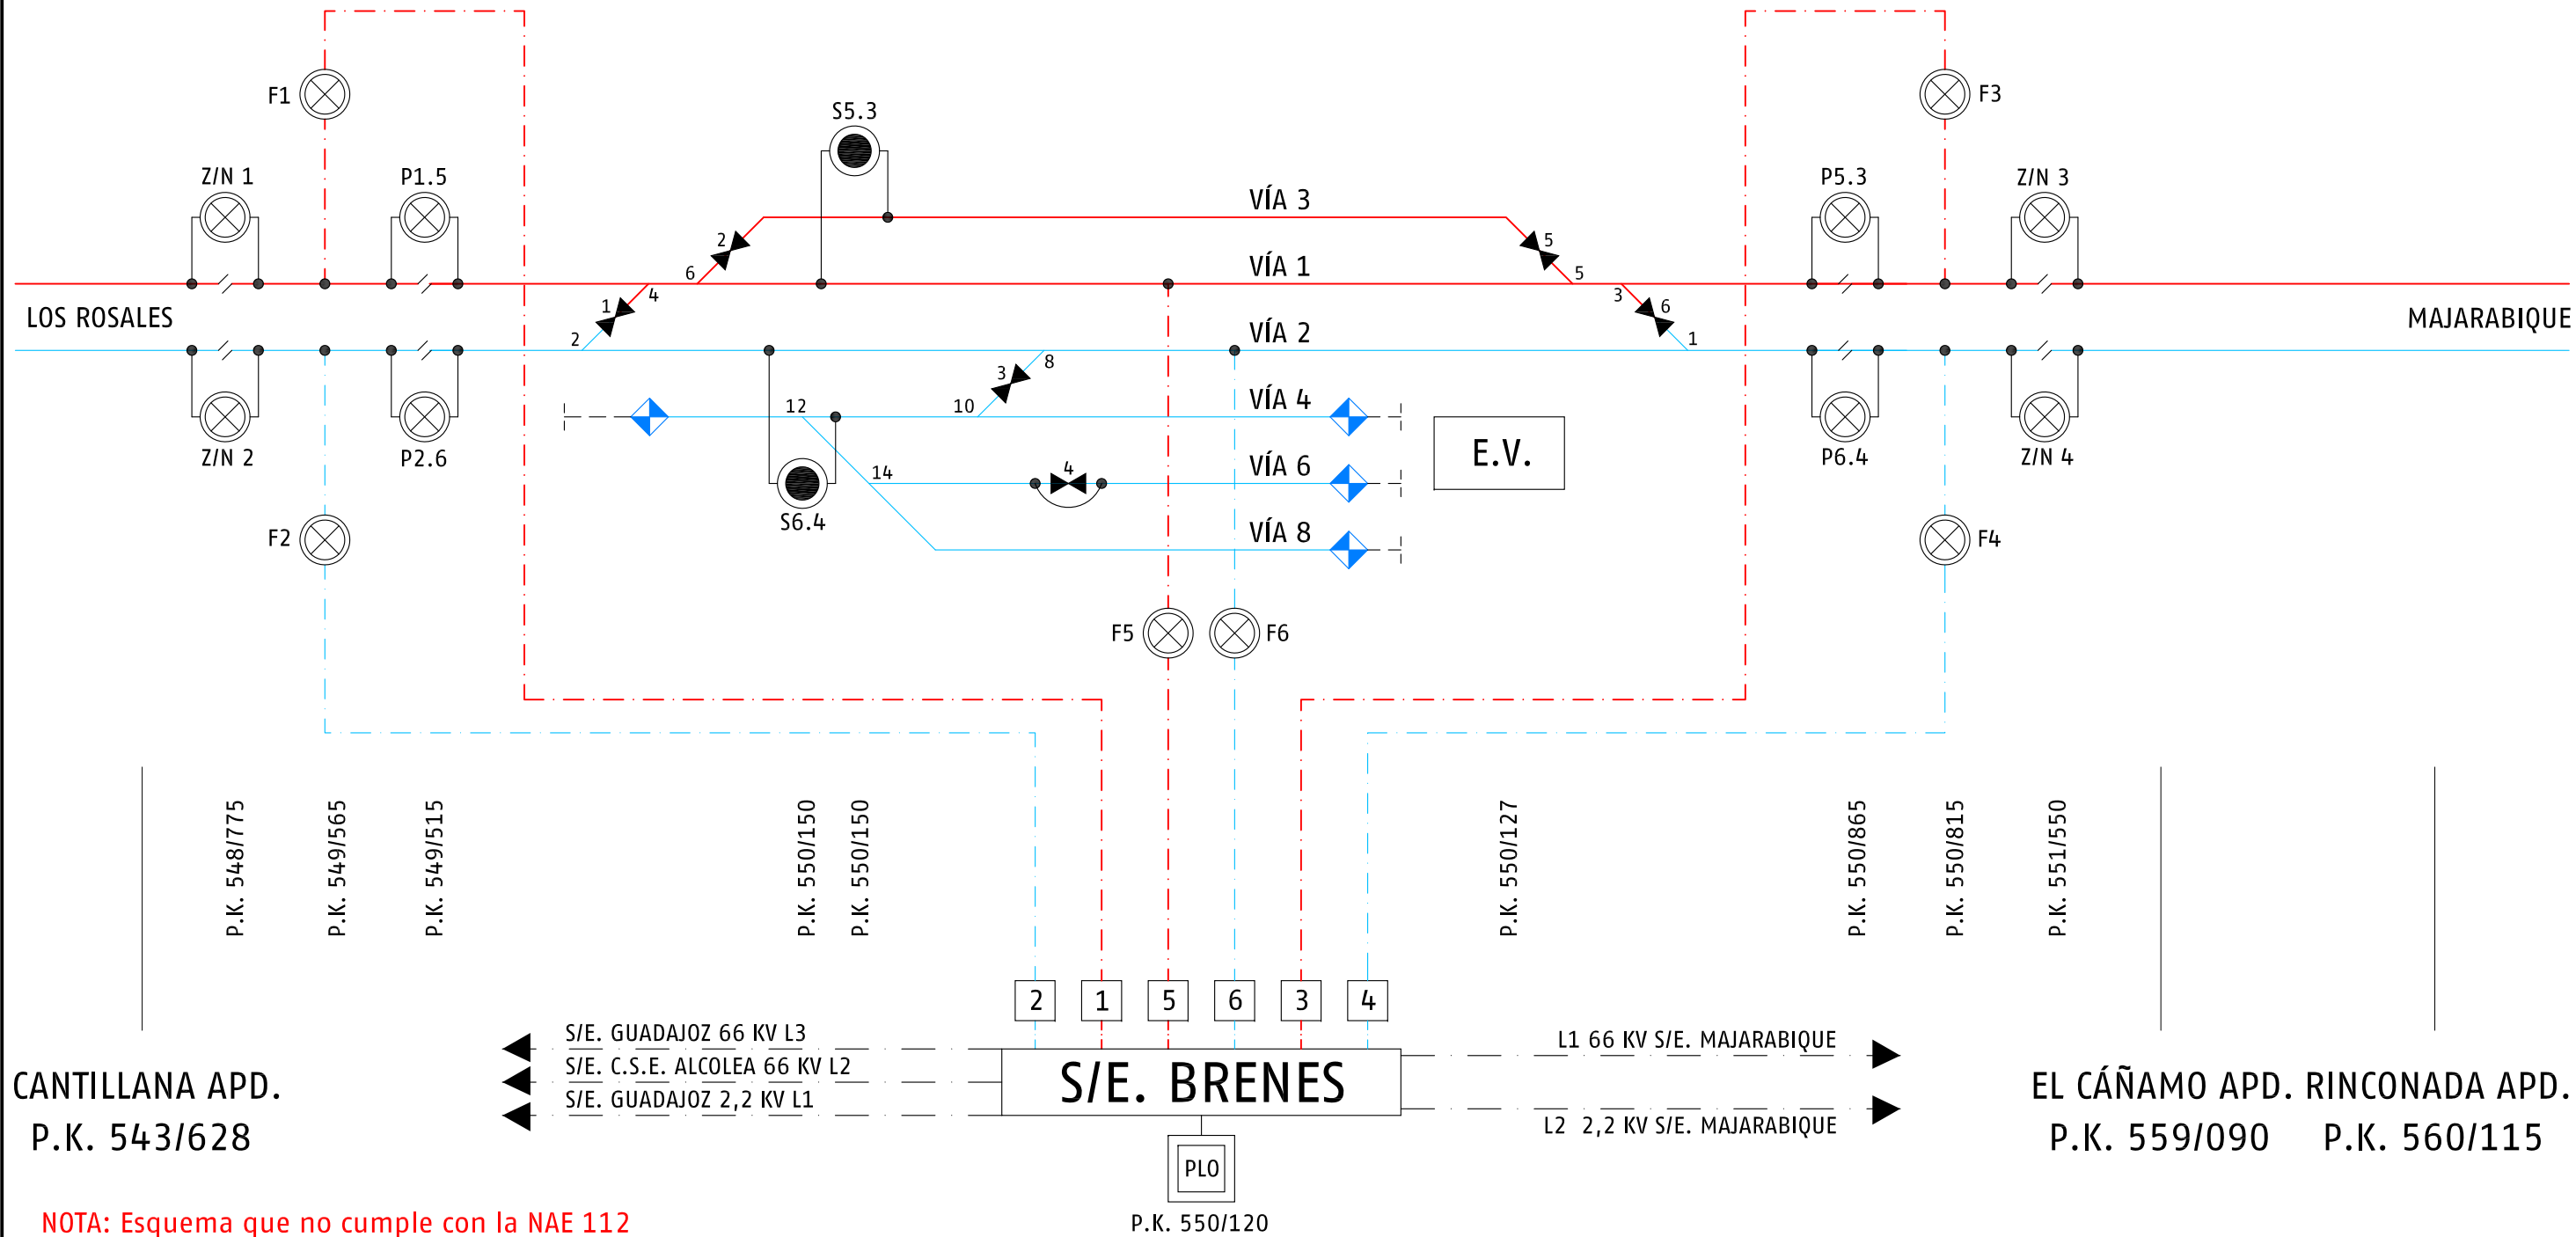

CANTILLANA APD.  
P.K. 543/628

S/E. GUADAJÓZ 66 KV L3  
S/E. C.S.E. ALCOLEA 66 KV L2  
S/E. GUADAJÓZ 2,2 KV L1

S/E. BRENES

L1 66 KV S/E. MAJARABIQUE  
L2 2,2 KV S/E. MAJARABIQUE

EL CÁÑAMO APD. RINCONADA APD.  
P.K. 559/090 P.K. 560/115

NOTA: Esquema que no cumple con la NAE 112



SUBDIRECCIÓN DE OPERACIONES  
RED CONVENCIONAL SUR  
JEFATURA DE ÁREA DE  
MANTENIMIENTO DE SEVILLA

Dibujado por: J.G.J.  
Aprobado por: Jose Angel Gomez Flores  
Firma: Jose Angel Gomez Flores  
Fecha: 19-JULIO-2024

ESQUEMA ELÉCTRICO L.A.C.  
P.E. 17 LÍNEA DE MADRID A SEVILLA  
BRENES

Plano nº 1 de 1  
Sustituye a: Hoja 5 de 8 de 26/11/15  
Hoja nº 5 de 11