


E.V.

AGUJAS	P.K.	AGUJAS	P.K.
11	0/930 (2) 0/834 (3)	7	568/004 (1) 0/001 (3)
9	0/931 (2) 0/835 (3)	3	568/013 (1)
2	567/087 (1) 0/031 (2)	1	568/085 (1)
4	567/092 (1) 0/026 (2)	10	568/097 (1)
5	568/004 (1) 0/001 (3)	14	568/177 (1)

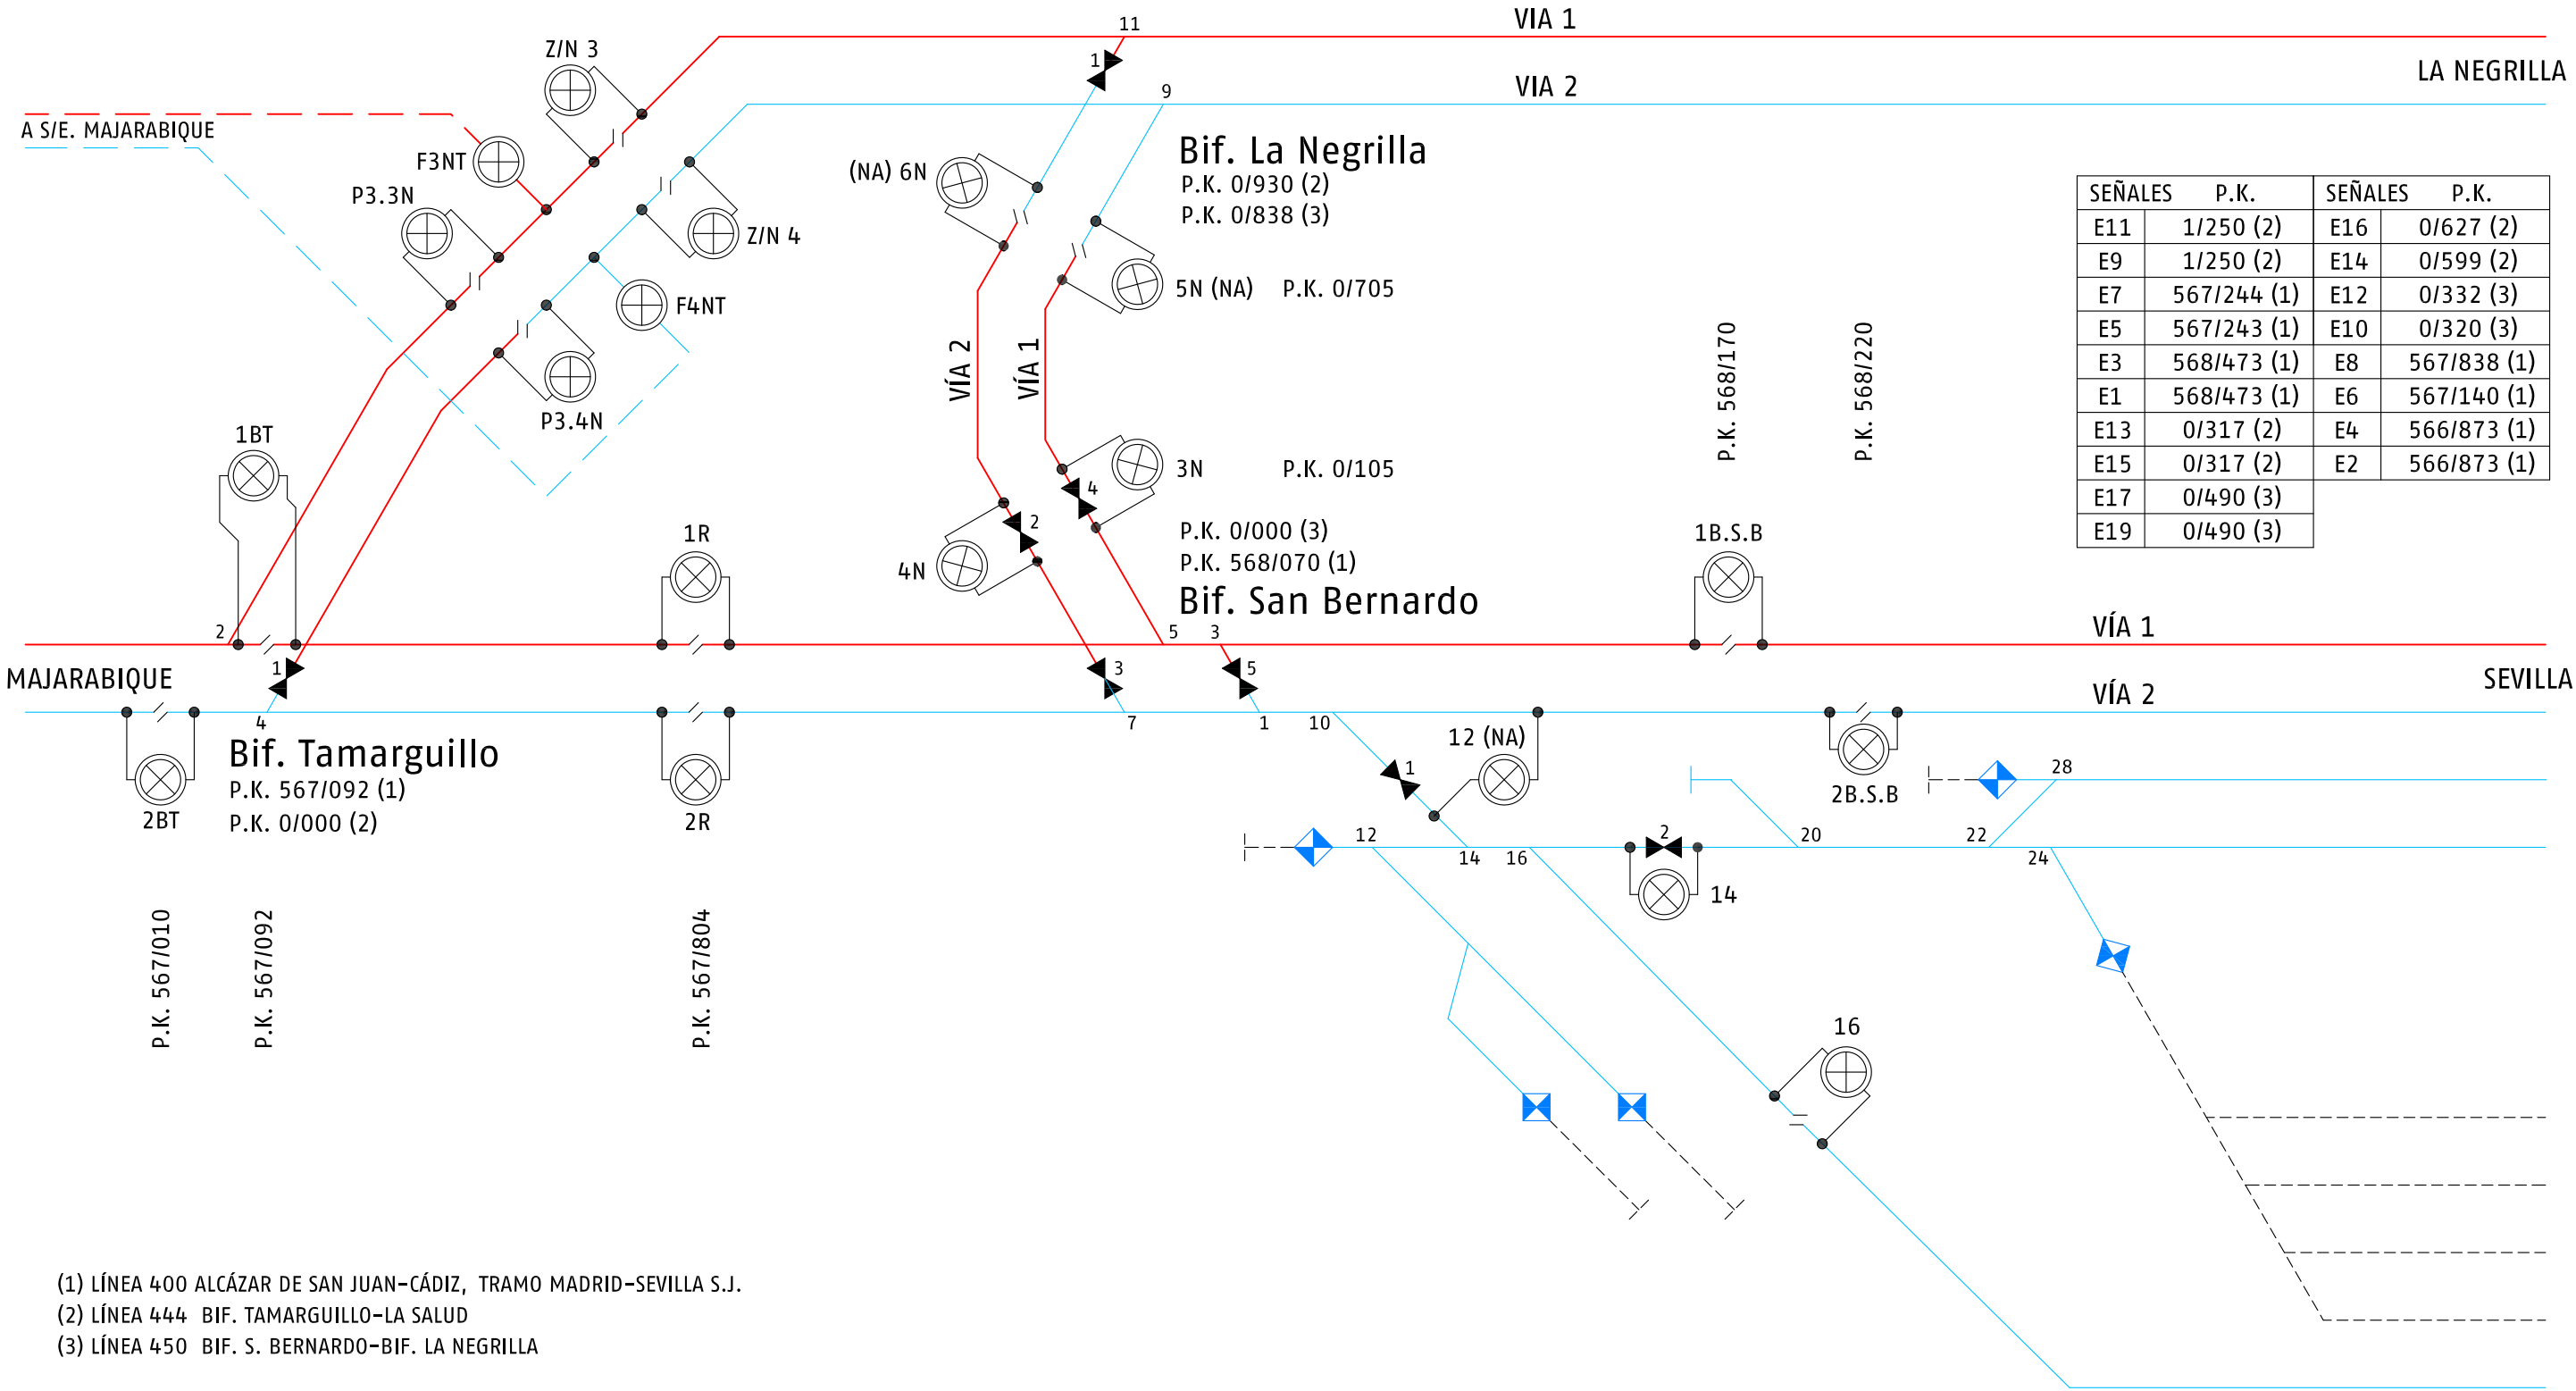

SEÑALES	P.K.	SEÑALES	P.K.
E11	1/250 (2)	E16	0/627 (2)
E9	1/250 (2)	E14	0/599 (2)
E7	567/244 (1)	E12	0/332 (3)
E5	567/243 (1)	E10	0/320 (3)
E3	568/473 (1)	E8	567/838 (1)
E1	568/473 (1)	E6	567/140 (1)
E13	0/317 (2)	E4	566/873 (1)
E15	0/317 (2)	E2	566/873 (1)
E17	0/490 (3)		
E19	0/490 (3)		

- (1) LÍNEA 400 ALCÁZAR DE SAN JUAN-CÁDIZ, TRAMO MADRID-SEVILLA S.J.
- (2) LÍNEA 444 BIF. TAMARGUILLO-LA SALUD
- (3) LÍNEA 450 BIF. S. BERNARDO-BIF. LA NEGRILLA

NOTA: Esquema que no cumple con la NAE 112



SUBDIRECCIÓN DE OPERACIONES
RED CONVENCIONAL SUR
JEFATURA DE ÁREA DE
MANTENIMIENTO DE SEVILLA

Dibujado por: J.G.J.
Aprobado por: Jose Angel Gomez Flores
Firma: Firmado digitalmente por Jose Angel Gomez Flores
Fecha: 2024.07.19 11:19:16 +02'00'
Fecha: 19-JULIO-2024

ESQUEMA ELÉCTRICO L.A.C.
P.E. 17 LÍNEA DE MADRID A SEVILLA
TRIANGULO TAMARGUILLO

Plano nº 1 de 1
Sustituye a: Hoja 7 de 8 de 26/11/15
Hoja nº 7 de 11