


AGUJAS	P.K.	AGUJAS	P.K.	AGUJAS	P.K.
2	5/118	14	5/340	26	5/469
4	5/188	16	5/366	28	5/506
6	5/190	18	5/375	30	5/516
8	5/262	20	5/404	32	5/543
10	5/290	22	5/433	34	5/552
12	5/315	24	5/469	36	5/300

SEÑALES	P.K.
E2	4/799
E4	4/799
E1	7/005
E3	7/005

AGUJAS	P.K.
1	6/686
3	6/616
7	6/368
9	6/298
11	6/245
T13a	6/207
T13b	6/182
15	6/169

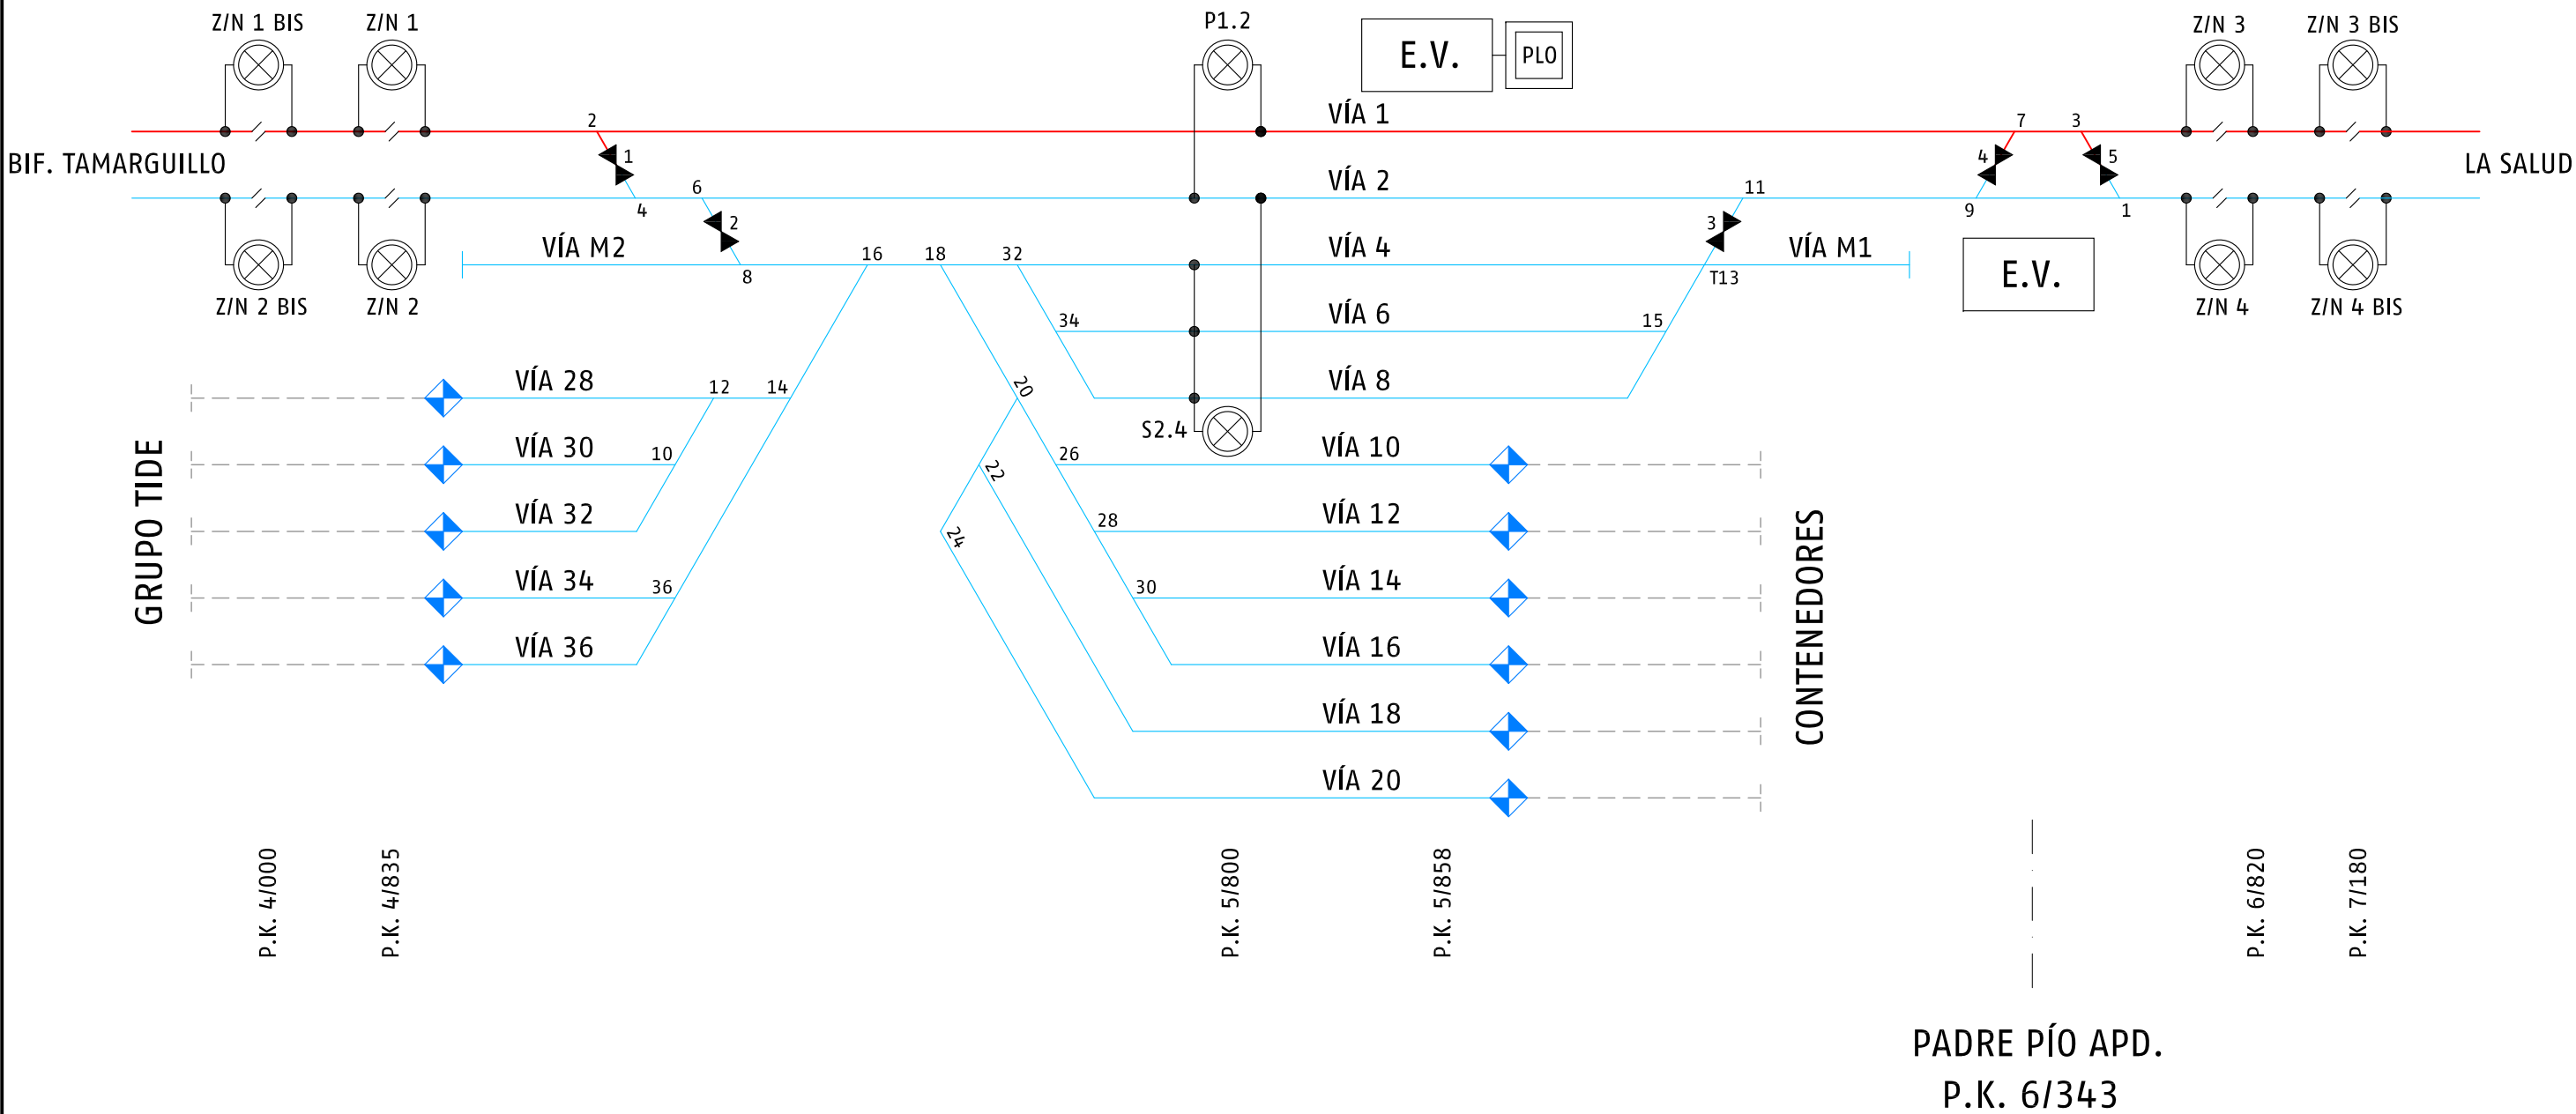

SUBDIRECCIÓN DE OPERACIONES
RED CONVENCIONAL SUR
JEFATURA DE ÁREA DE
MANTENIMIENTO DE SEVILLA

Dibujado por: J.G.J.
Aprobado por: Jose Angel Gomez Flores
Firma: Firmado digitalmente por Jose Angel Gomez Flores Fecha: 2024.07.19 11:19:16 +02'00'
Fecha: 19-JULIO-2024

ESQUEMA ELÉCTRICO L.A.C.
P.E. 17 LÍNEA DE MADRID A SEVILLA
LA NEGRILLA

Plano nº 1 de 1
Sustituye a:
Hoja nº 8 de 11