


AGUJAS	P.K.
2	14/346
4	14/435
6	14/668
8	14/712
10	14/792

SEÑALES	P.K.
E4	14/066
E2	14/066
E1	15/728
E3	15/728

AGUJAS	P.K.
5	15/372
3	15/381
1	15/452

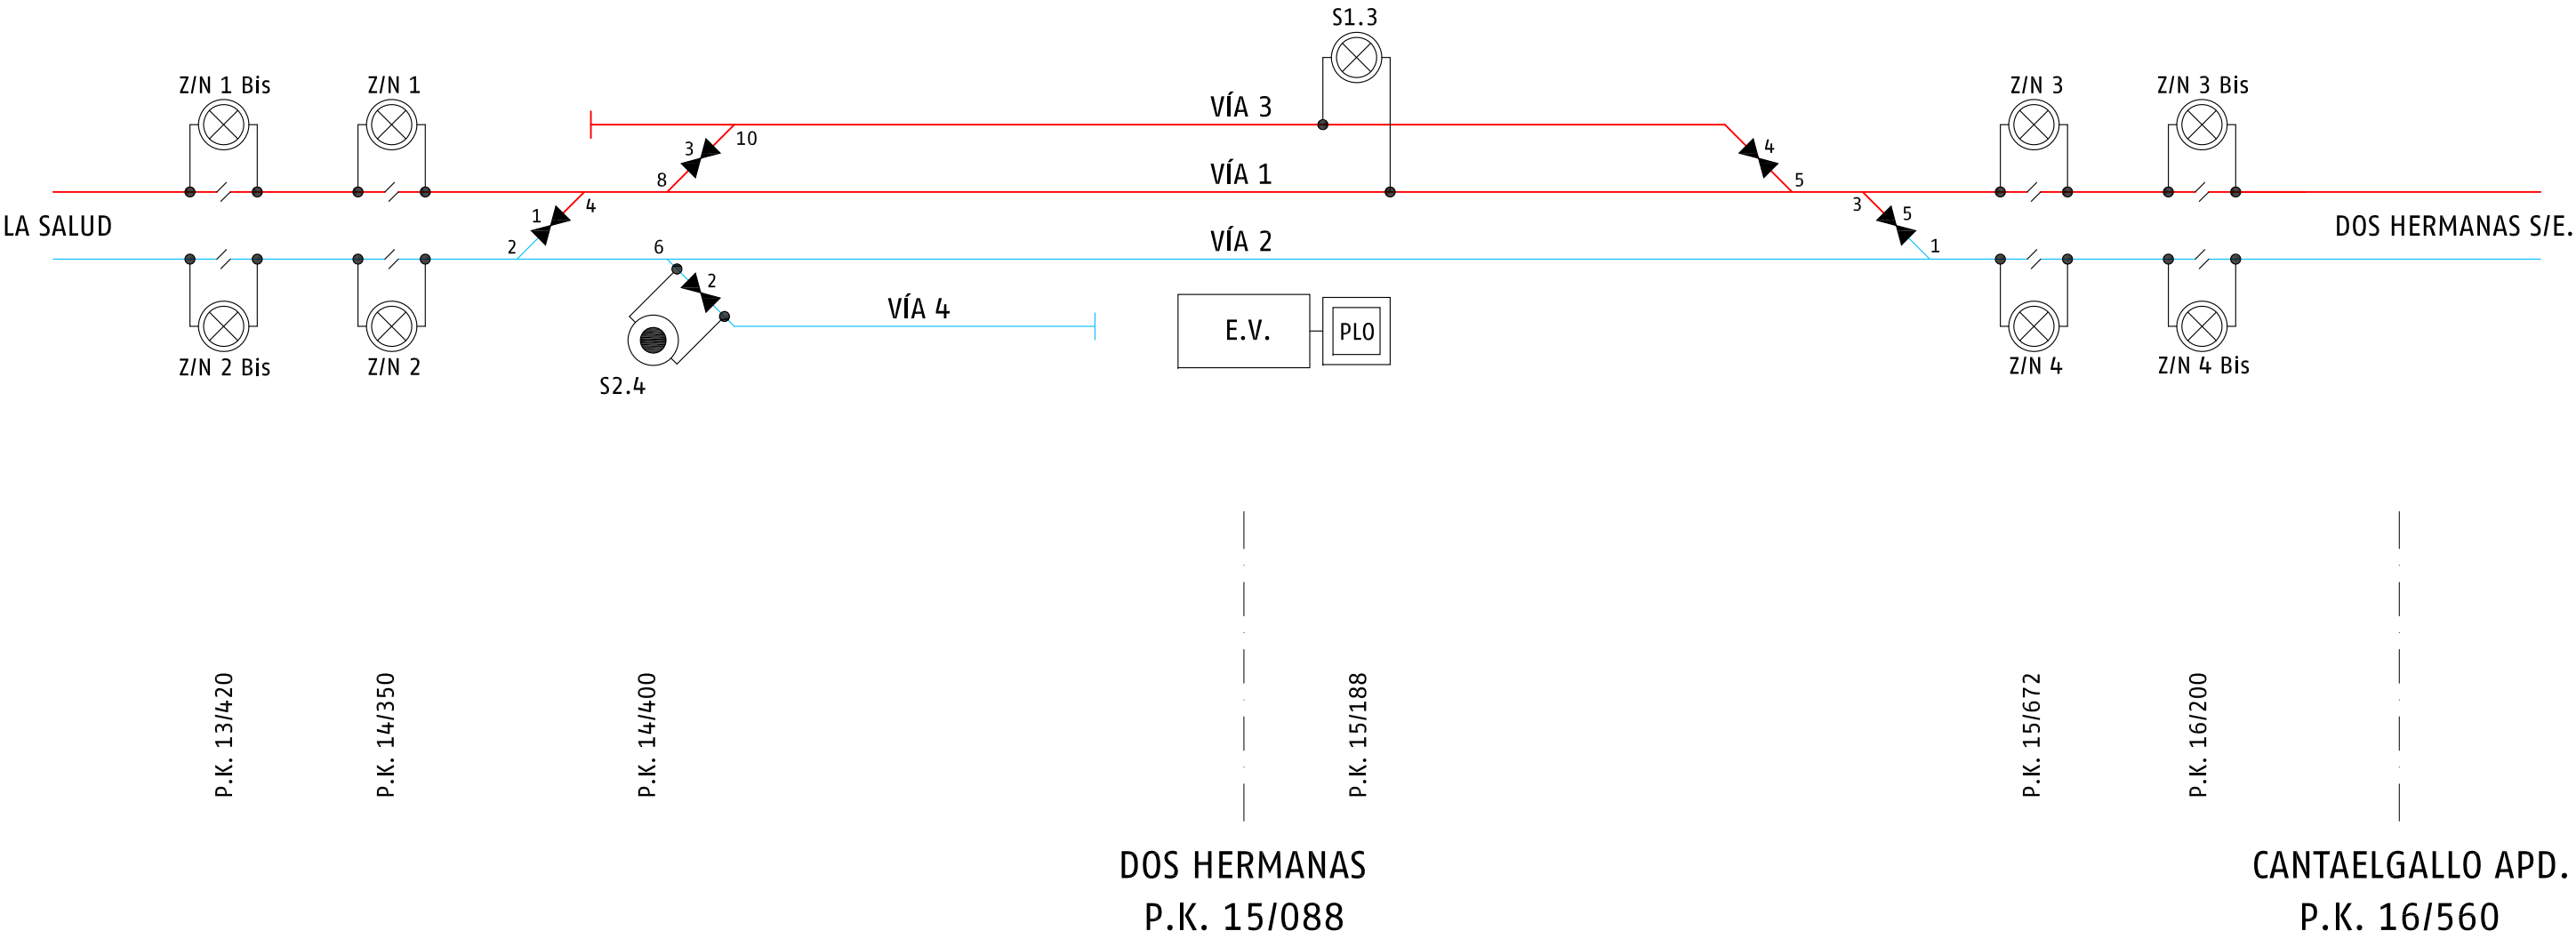

SUBDIRECCIÓN DE OPERACIONES
RED CONVENCIONAL SUR
JEFATURA DE ÁREA DE
MANTENIMIENTO DE SEVILLA

Dibujado por: J.G.J.
Aprobado por: Jose Angel Gomez Flores
Firma
Fecha: 19 FEBRERO 2025

ESQUEMA ELÉCTRICO L.A.C.
P.E. 24 LÍNEA DE SEVILLA A CÁDIZ
DOS HERMANAS

Plano nº
Sustituye a: Hoja 3 de 21 de 07/04/2021
Hoja nº 03 de 21