


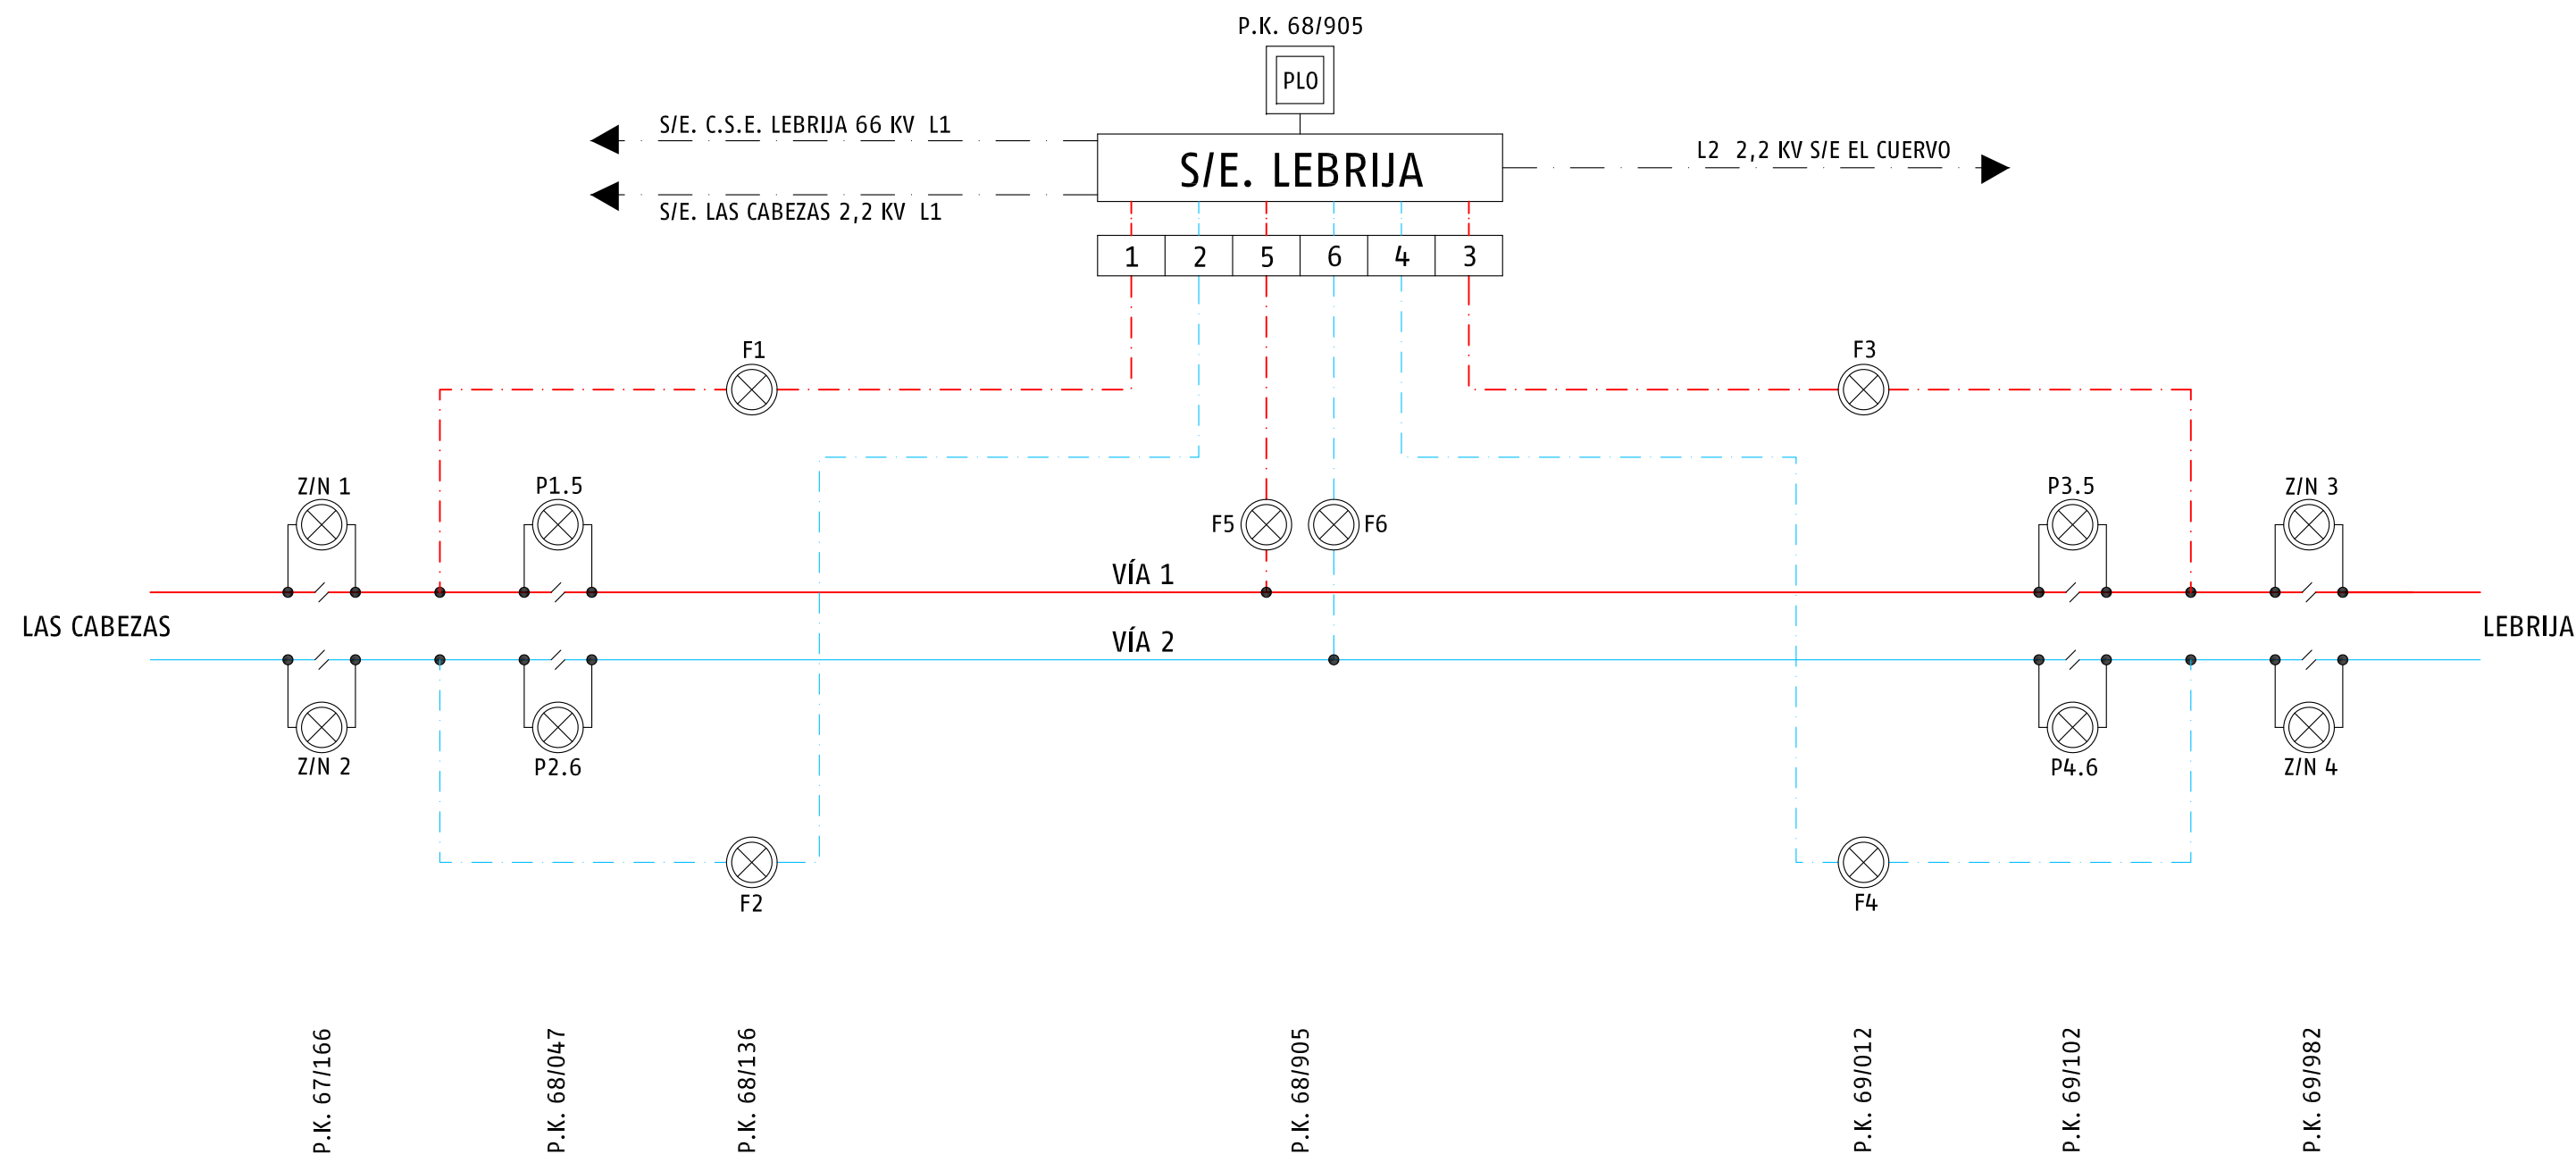

SUBDIRECCIÓN DE OPERACIONES
RED CONVENCIONAL SUR
JEFATURA DE ÁREA DE
MANTENIMIENTO DE SEVILLA

Dibujado por:	J.G.J.
Aprobado por:	Jose Angel Gomez Flores
Firma	
Fecha:	19 FEBRERO 2025

ESQUEMA ELÉCTRICO L.A.C.
P.E. 24 LÍNEA DE SEVILLA A CÁDIZ
LEBRIJA S/E.

Plano nº	1 de 1
Sustituye a:	Hoja 8 de 21 de 08/04/21
Hoja nº	08 de 21