
AGUJAS	P.K.
2	73/365
4	73/459
6	73/479
8	73/574
10	73/824
12	73/824
14	73/891
16	73/946

SEÑALES	P.K.
E2	73/094
E4	73/094
E1	74/959
E3	75/025

AGUJAS	P.K.
7	74/572
5	74/572
3	74/594
1	74/689

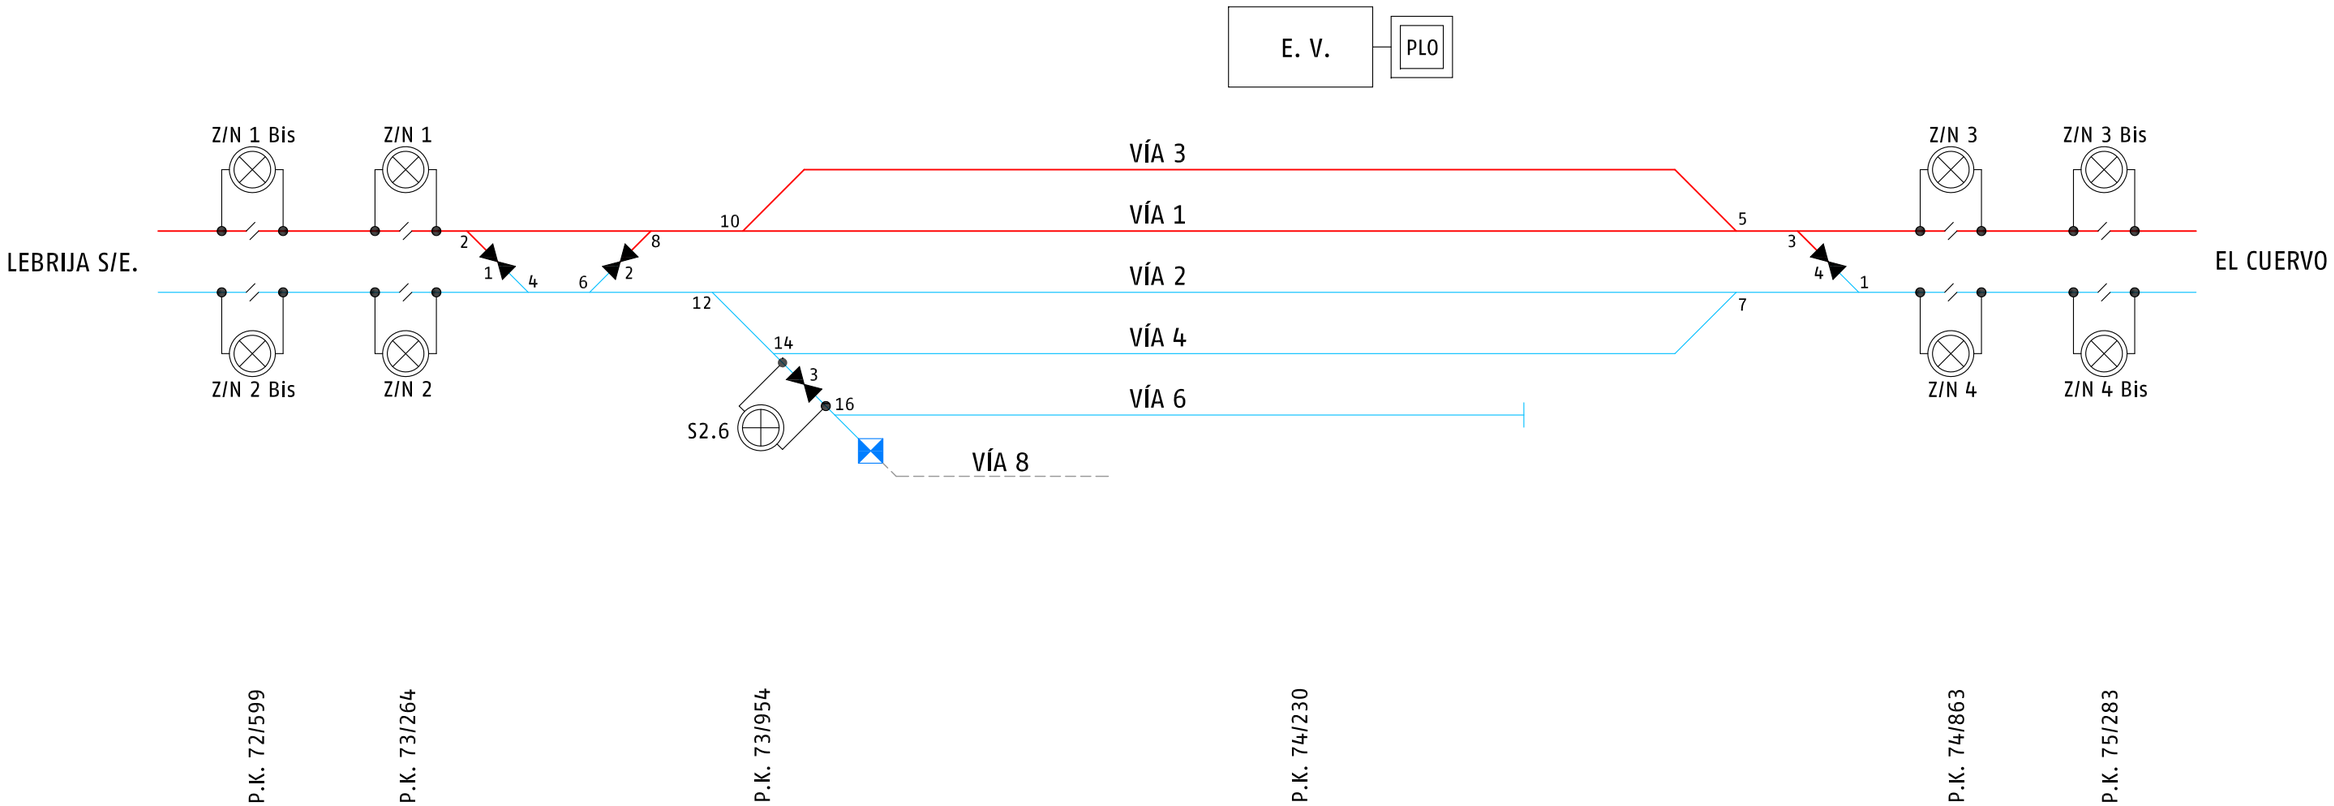

adif	SUBDIRECCIÓN DE OPERACIONES RED CONVENCIONAL SUR JEFATURA DE ÁREA DE MANTENIMIENTO DE SEVILLA	Dibujado por: J.G.J. Aprobado por: Jose Angel Gomez Flores Firma Fecha: 19 FEBRERO 2025	ESQUEMA ELÉCTRICO L.A.C. P.E. 24 LÍNEA DE SEVILLA A CÁDIZ LEBRIJA	Plano nº 1 de 1 Sustituye a: Hoja 9 de 21 de 08/03/21 Hoja nº 09 de 21