
AGUJAS	P.K.
2	103/653
4	103/744
6	103/784
8	103/836
10	103/896
12	103/958

SEÑALES	P.K.
E2	103/371
E4	103/371
E1	110/313
E3	110/481

AGUJAS	P.K.
9	109/818
7	109/902
5	109/812
3	109/987
1	110/042

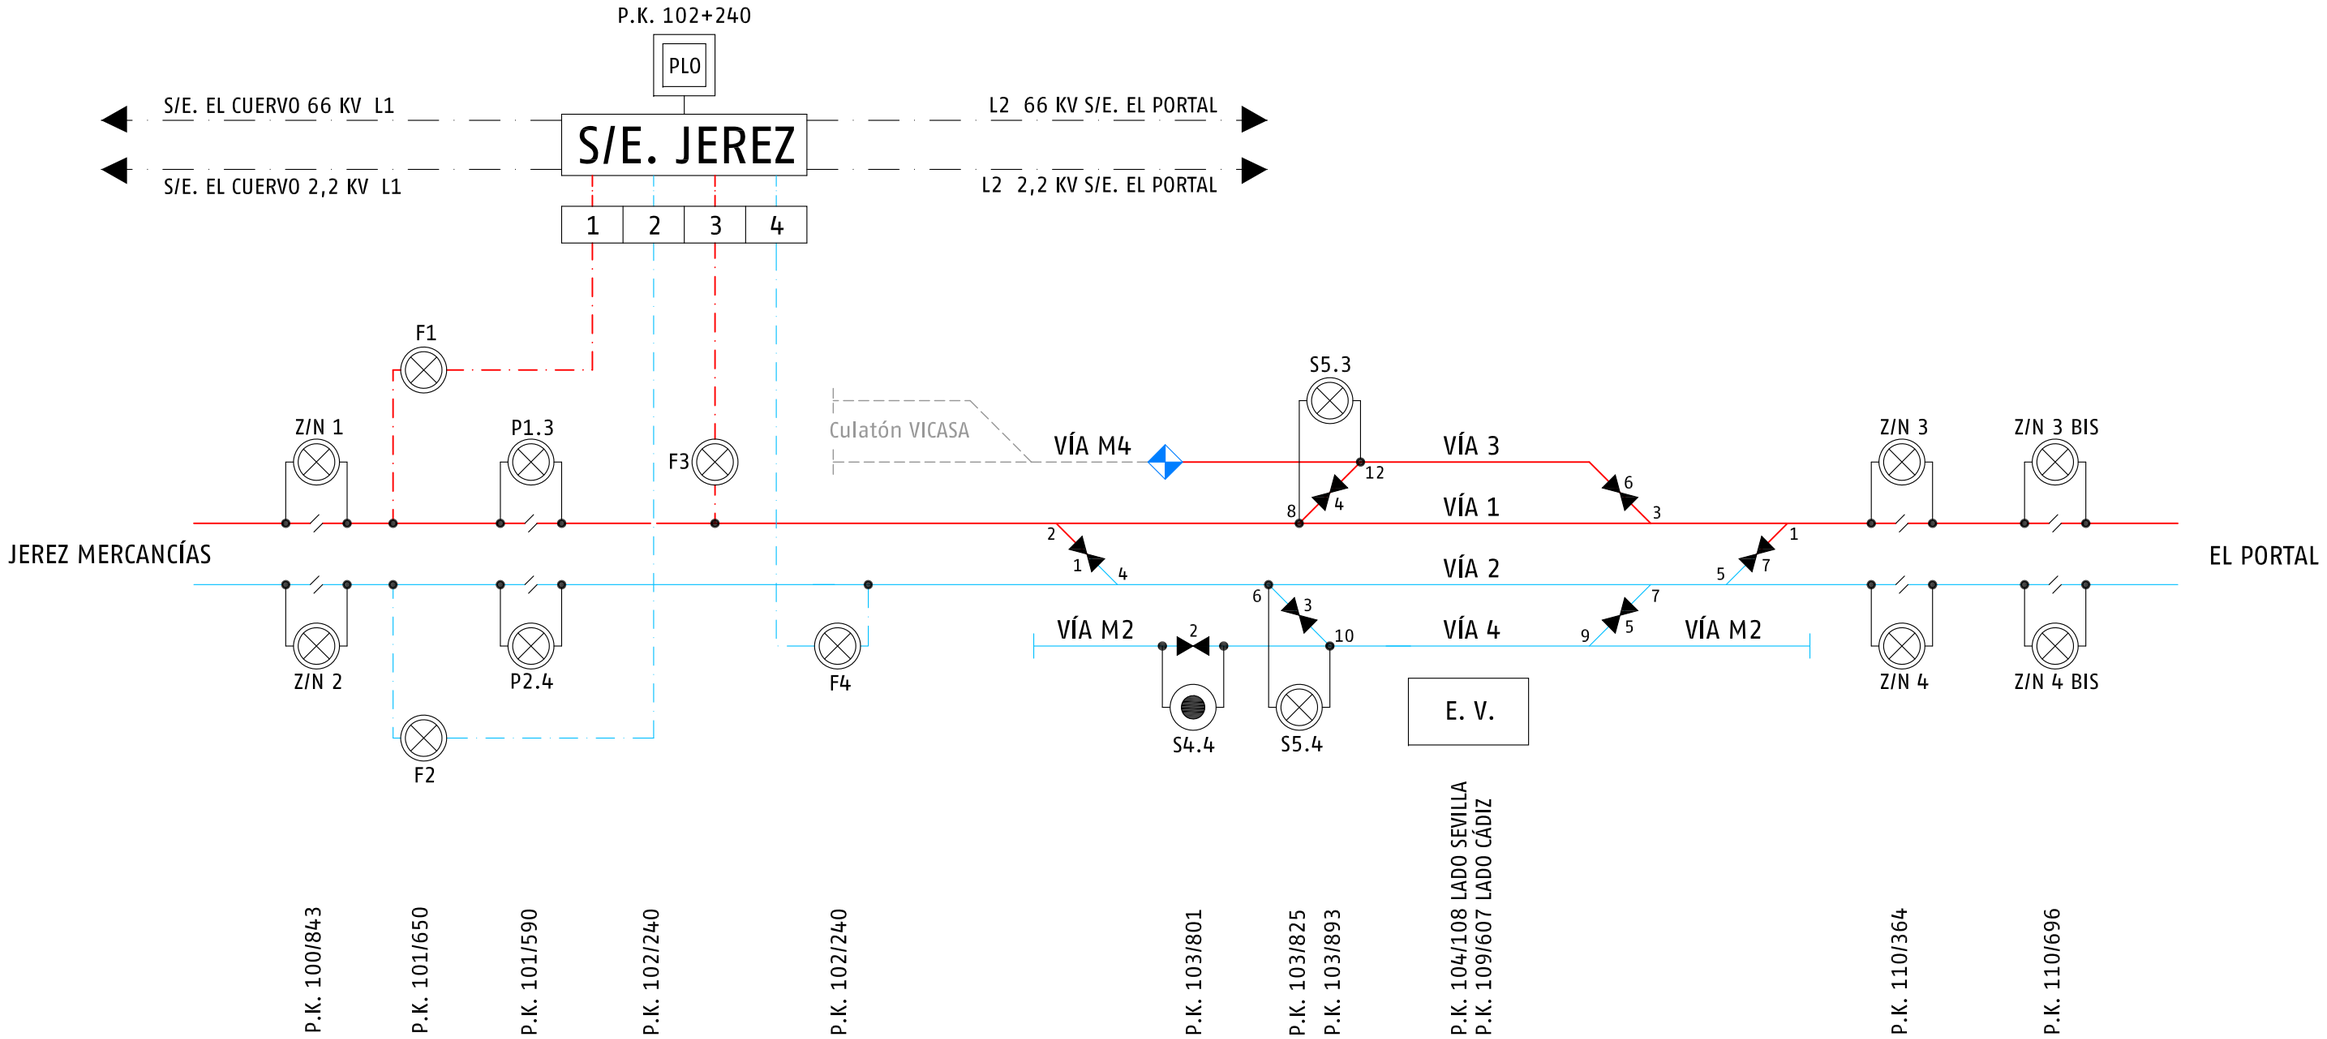

adif	SUBDIRECCIÓN DE OPERACIONES RED CONVENCIONAL SUR JEFATURA DE ÁREA DE MANTENIMIENTO DE SEVILLA	Dibujado por: J.G.J. Aprobado por: Jose Angel Gomez Flores Firma Fecha: 19 FEBRERO 2025	ESQUEMA ELÉCTRICO L.A.C. P.E. 24 LÍNEA DE SEVILLA A CÁDIZ JEREZ DE LA FRONTERA	Plano nº 1 de 1 Sustituye a: Hoja 13 de 21 de 12/04/21 Hoja nº 13 de 21