


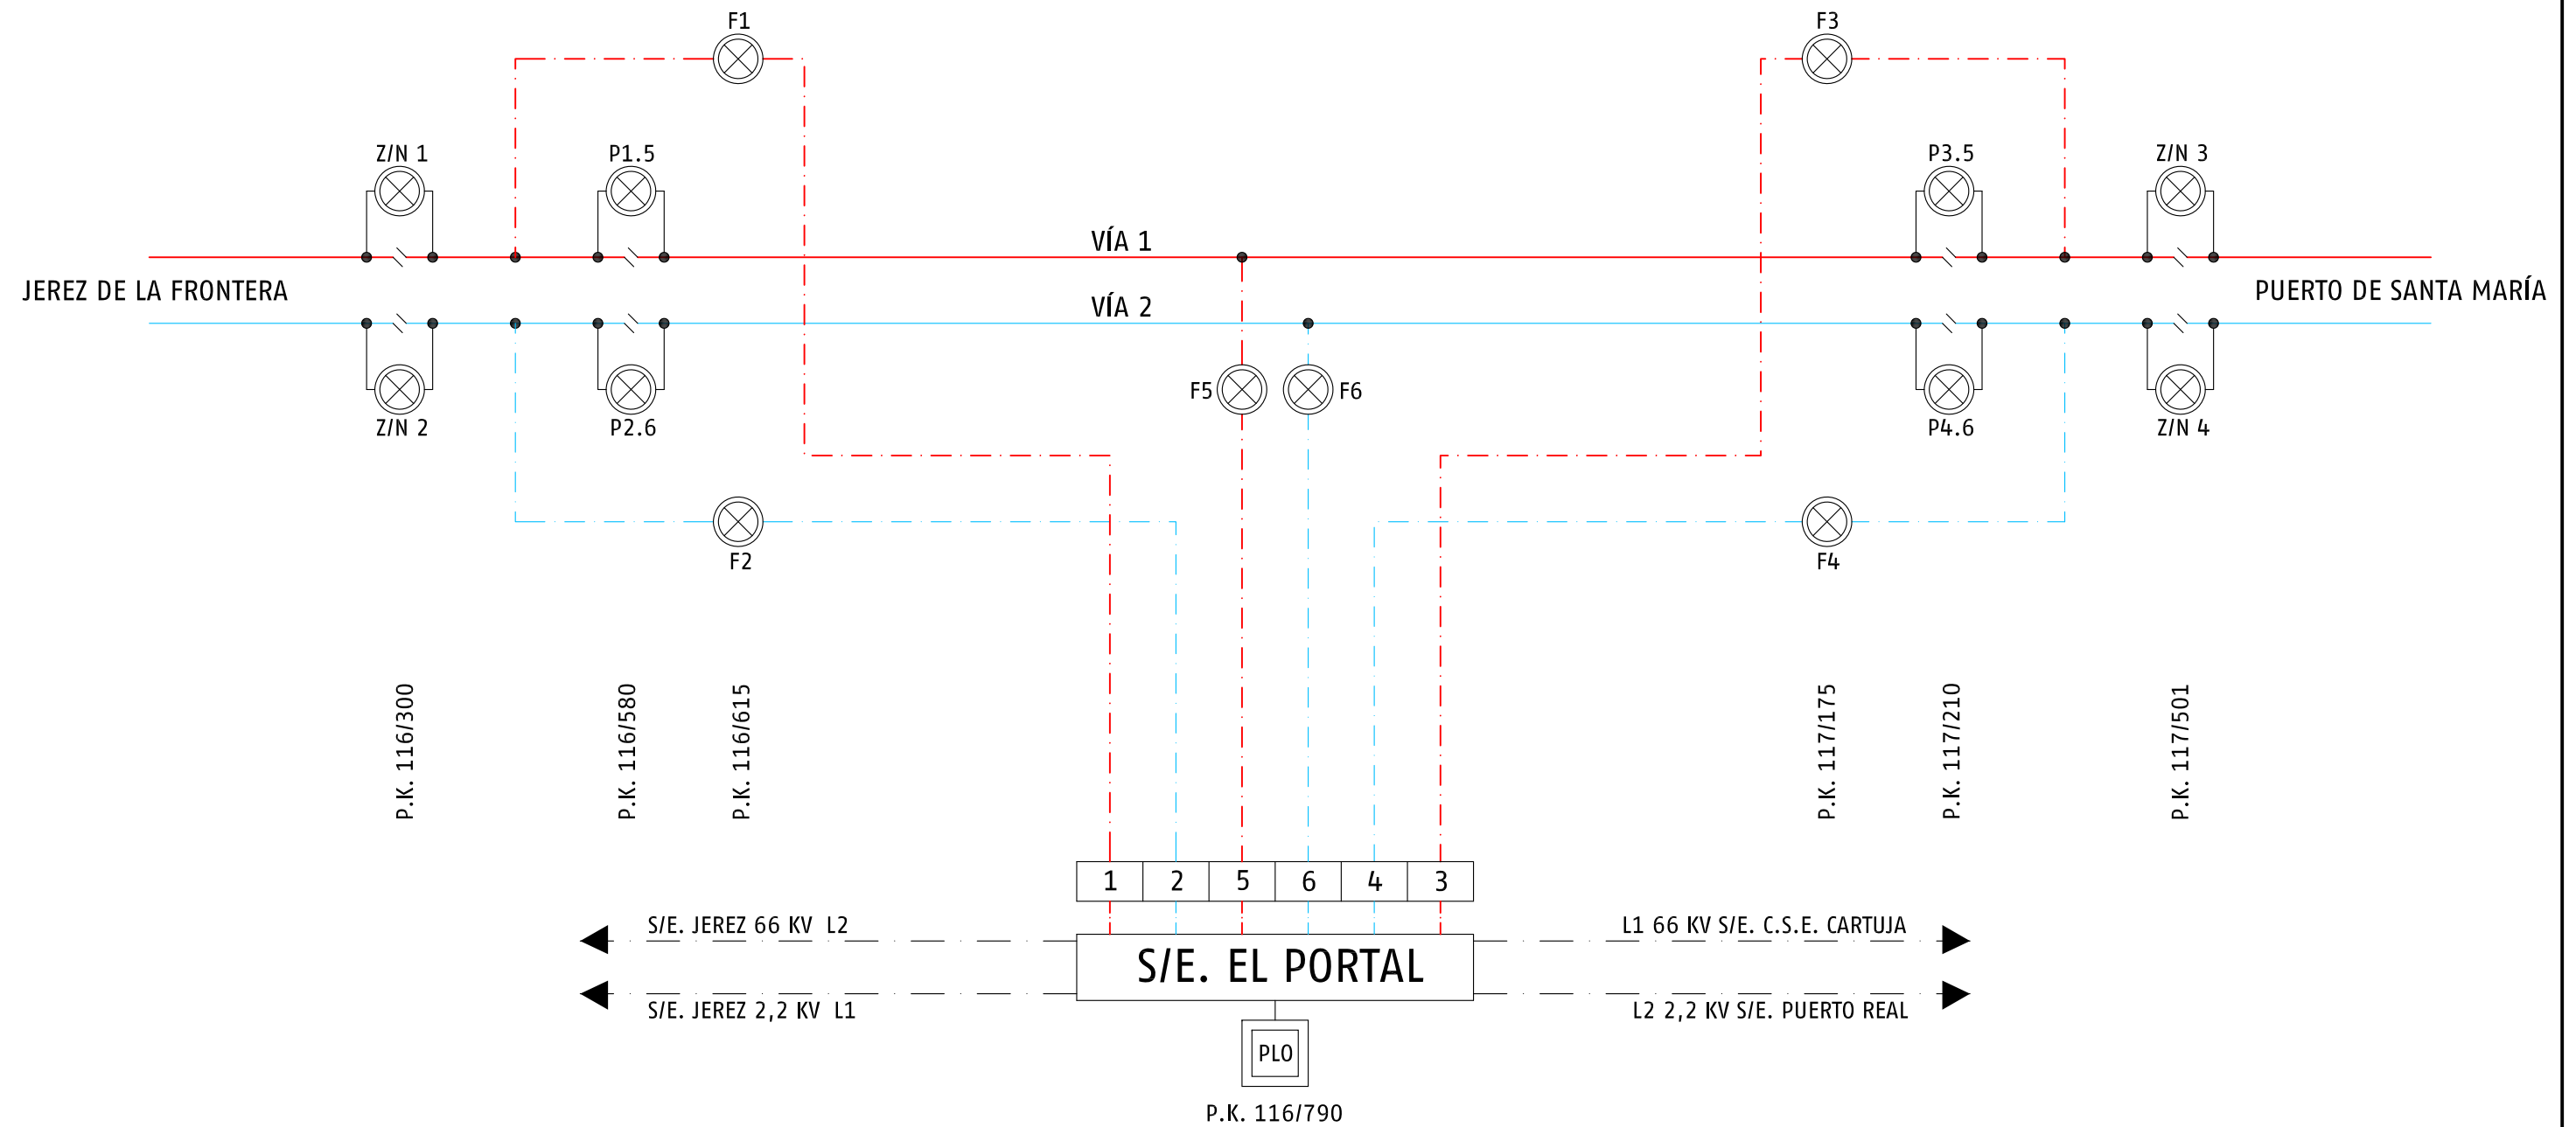

SUBDIRECCIÓN DE OPERACIONES
RED CONVENCIONAL SUR
JEFATURA DE ÁREA DE
MANTENIMIENTO DE SEVILLA

Dibujado por: J.G.J.
Aprobado por: Jose Angel Gomez Flores
Firma:
Fecha: 19 FEBRERO 2025

ESQUEMA ELÉCTRICO L.A.C.
P.E. 24 LÍNEA DE SEVILLA A CÁDIZ
EL PORTAL S/E.

Plano nº 1 de 1
Sustituye a: Hoja 14 de 21 de 17/04/21
Hoja nº 14 de 21