


AGUJAS S. FERNANDO -BAHÍA SUR	
P.K.	
2	145/135
4	145/135
17	145/668
19	145/668
15	145/677
13	145/752
11	145/760
9	145/835

SEÑALES S. FERNANDO -BAHÍA SUR		SEÑALES RÍO ARILLO	
P.K.		P.K.	
E2	144/708	E6	146/634
E4	144/709	E8	146/634
E5	146/112	E3	148/124
E7	146/112	E1	148/124

AGUJAS RÍO ARILLO	
P.K.	
7	147/737
5	147/737
1	147/808
3	147/808

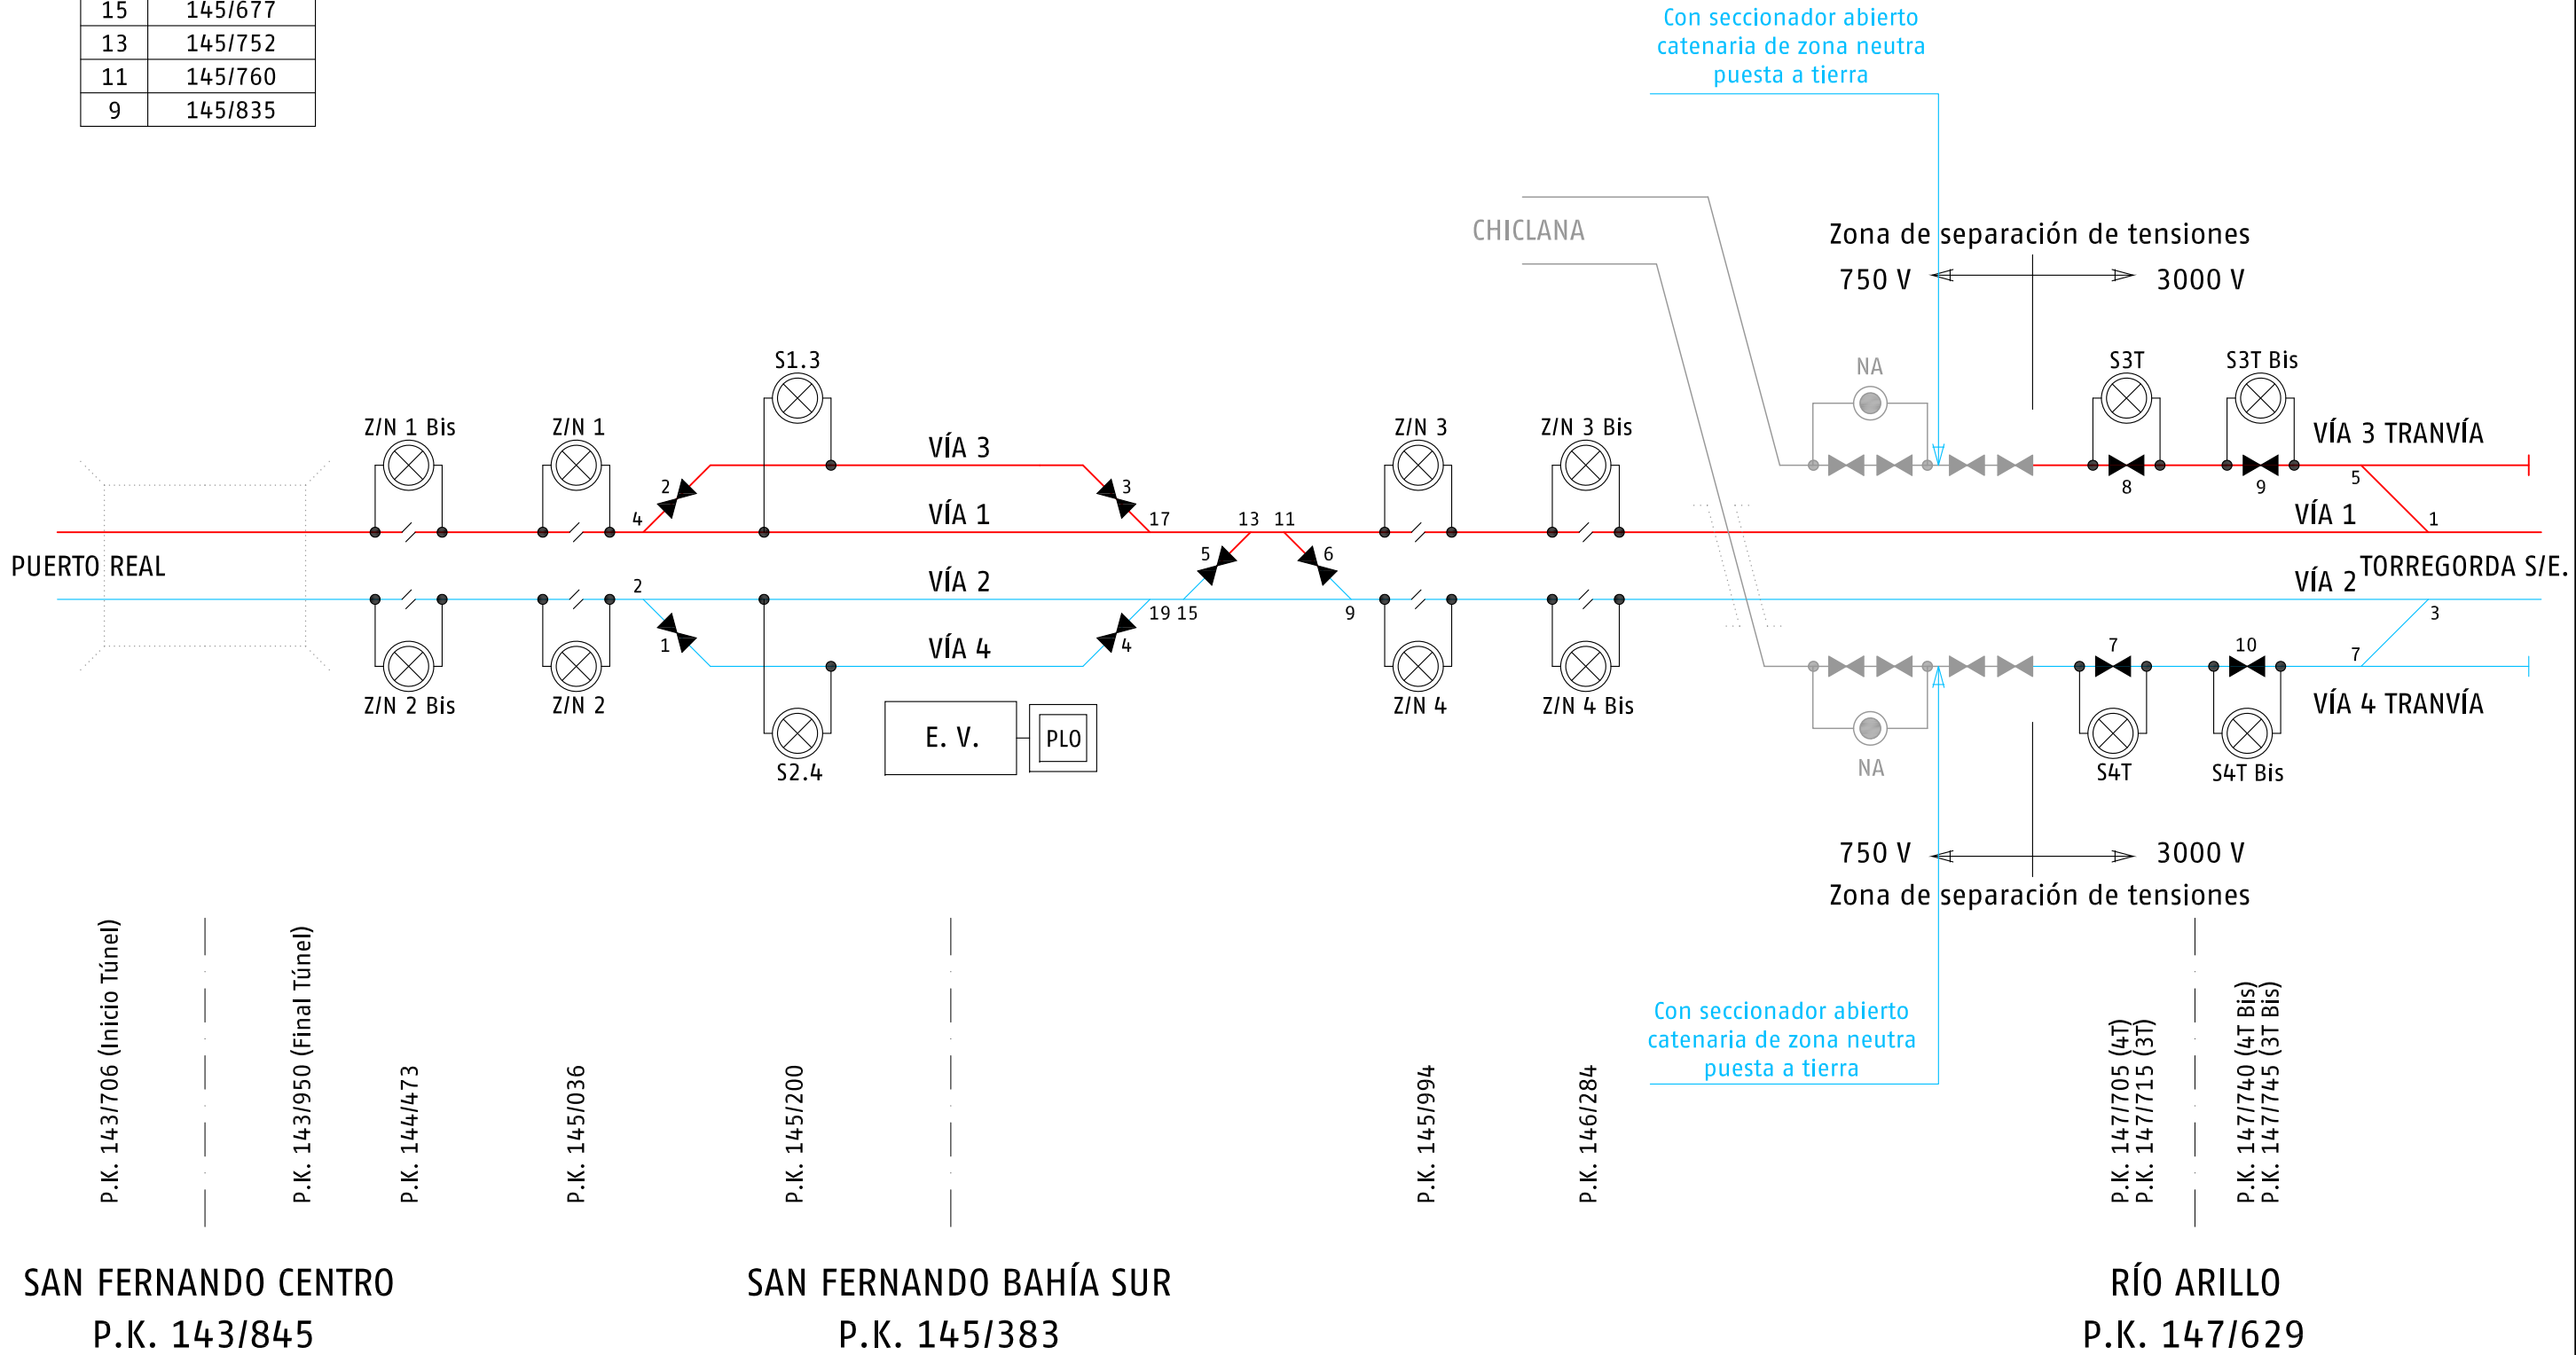

SAN FERNANDO CENTRO
P.K. 143/845

SAN FERNANDO BAHÍA SUR
P.K. 145/383

RÍO ARILLO
P.K. 147/629



SUBDIRECCIÓN DE OPERACIONES
RED CONVENCIONAL SUR
JEFATURA DE ÁREA DE
MANTENIMIENTO DE SEVILLA

Dibujado por: J.G.J.

Aprobado por: Jose Angel Gomez Flores

Firma

Fecha: 19 FEBRERO 2025

Formato digitalizado por Jose Angel Gomez Flores
Reservados todos los derechos. No se permite la explotación económica ni la transformación de esta obra. Queda permitida la impresión en su totalidad.

ESQUEMA ELÉCTRICO L.A.C.
P.E. 24 LÍNEA DE SEVILLA A CÁDIZ
SAN FERNANDO-BAHÍA SUR-RÍO ARILLO

Plano nº 1 de 1

Sustituye a: Hoja 18 de 21 de 26/04/21

Hoja nº 18 de 21