


AGUJAS	P.K.	AGUJAS	P.K.	AGUJAS	P.K.
2	562/024	16	562/199	28	562/422
4	562/095	18	562/240	T32	562/469
6	562/082	20	562/274	34	562/467
8	562/149	22	562/283	T38	562/515
10	562/155	24	562/354	44	562/559
14	562/196	26	562/393		

SEÑALES	P.K.	SEÑALES	P.K.
E2	561/777	E1	563/974
E4	561/777	E3	563/974
		E5	563/908
		E15	563/960

AGUJAS	P.K.	AGUJAS	P.K.
1	563/888	T15	563/588
3	563/722	T17	563/542
5	563/658	T19	563/524
7	563/658	T23	563/478
9	563/658	T27	564/852
11	563/594	T29	564/805
13	563/594		

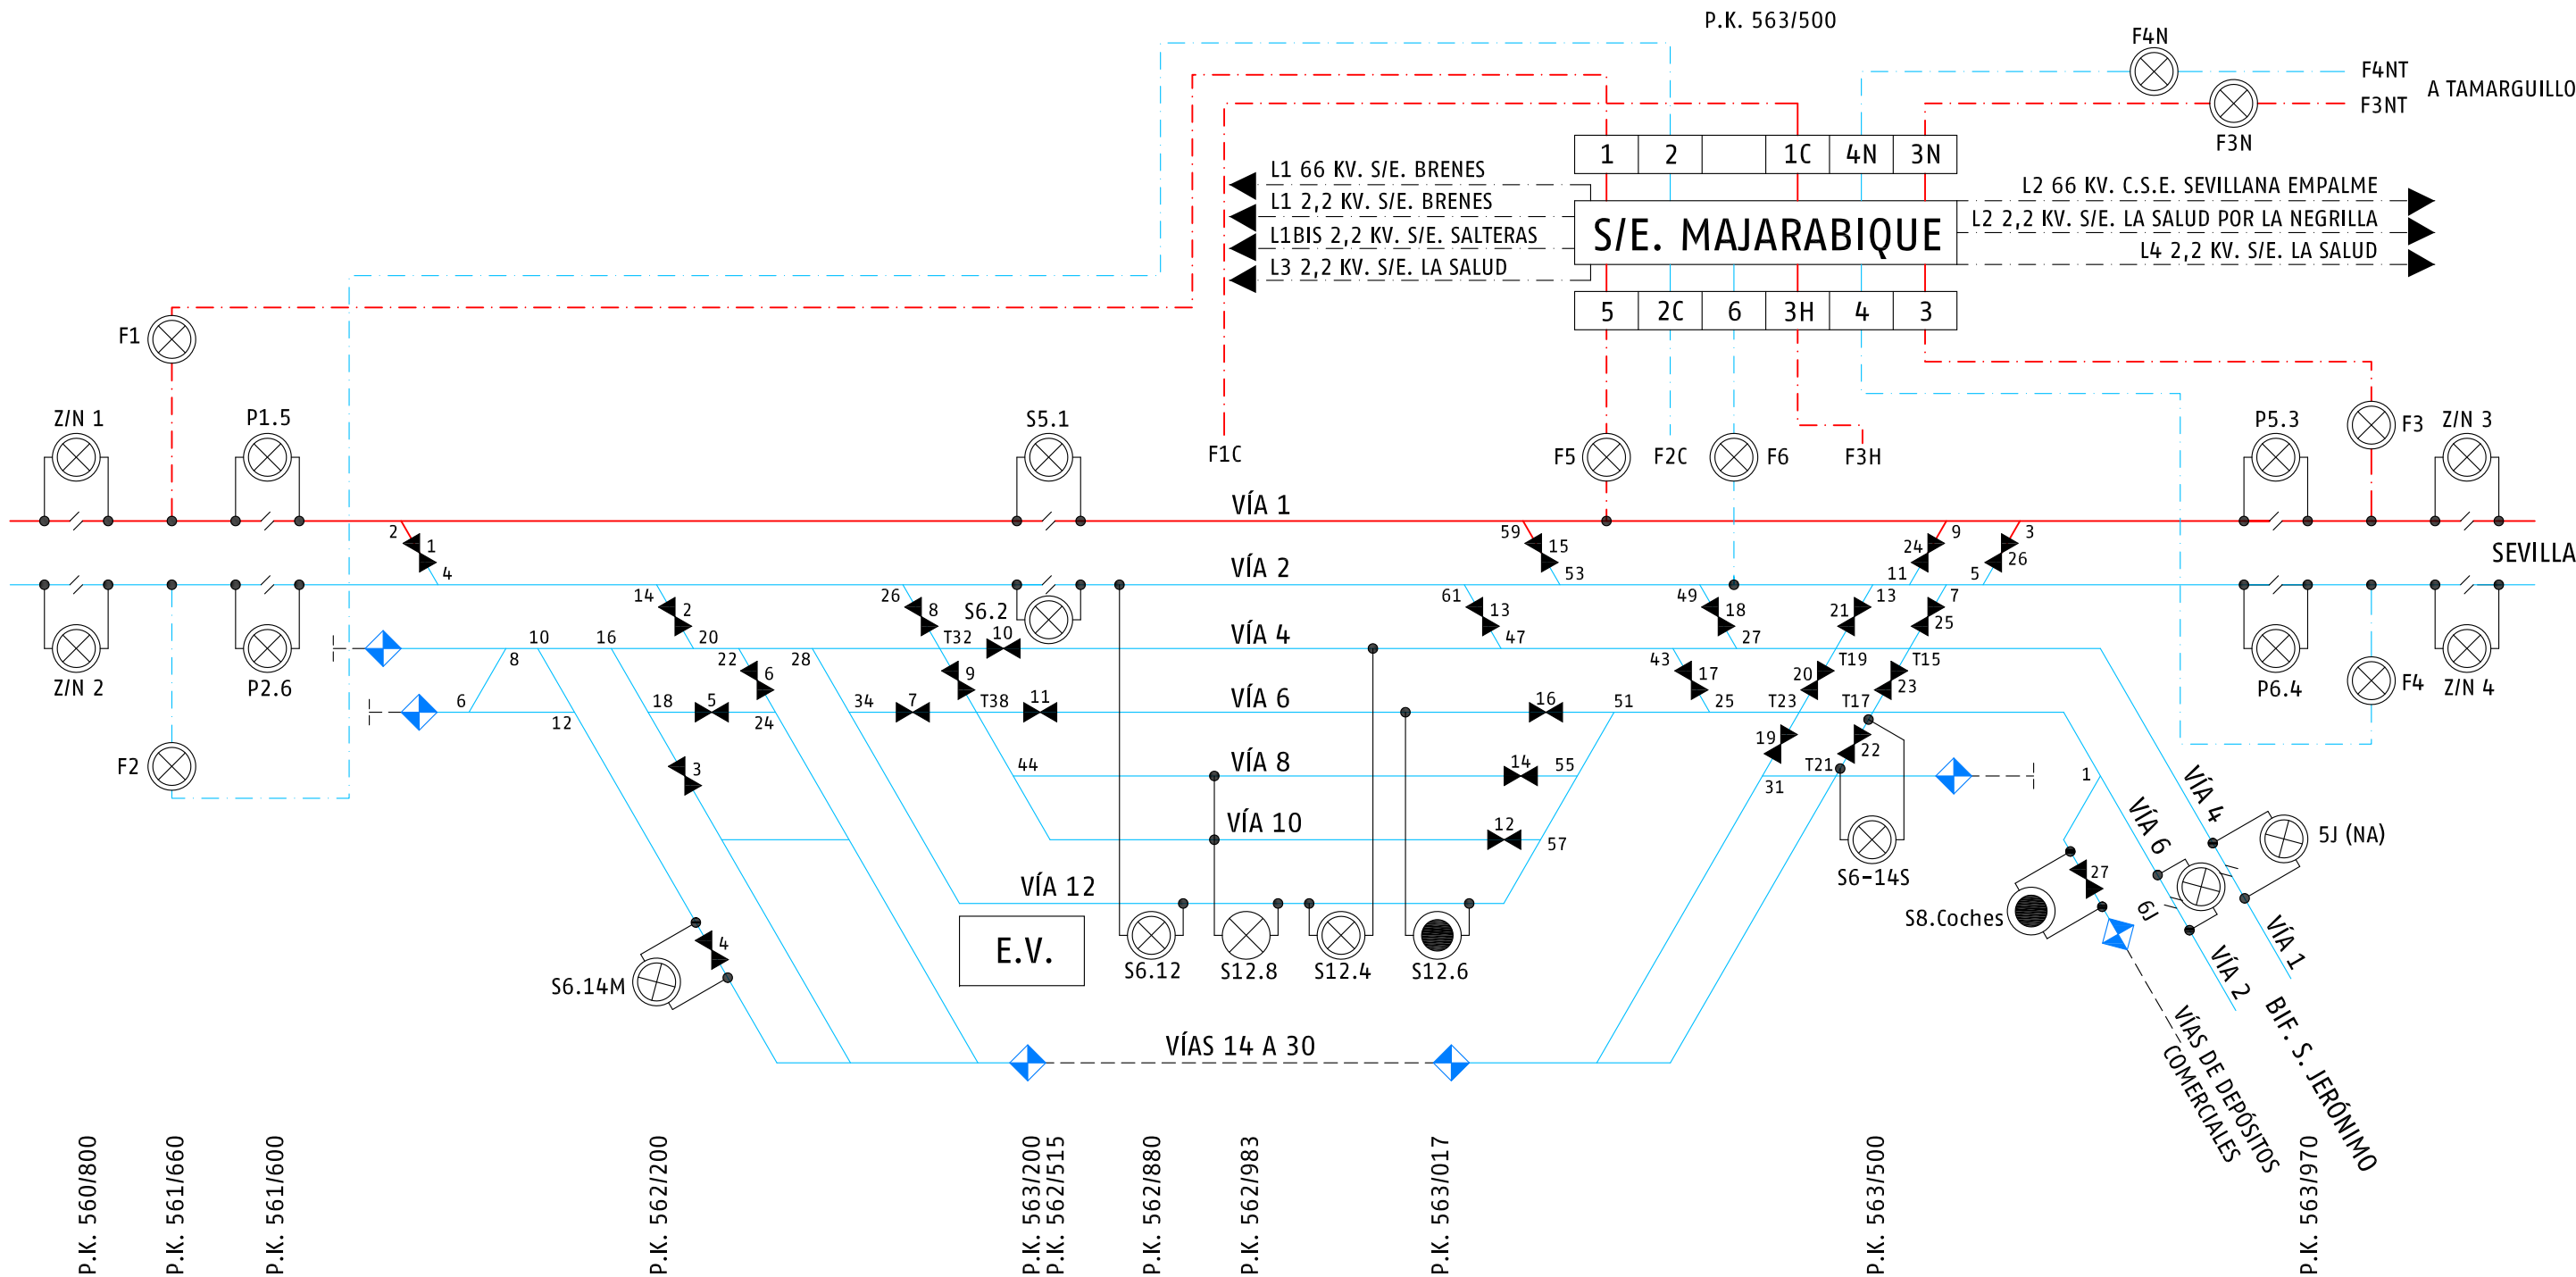

TODOS LOS PP.KK. DE ESTA HOJA PERTENECEN A LA LÍNEA 400 ALCÁZAR DE SAN JUAN-CÁDIZ, TRAMO MADRID-SEVILLA S.J.

NOTA: Esquema que no cumple con la NAE 112



SUBDIRECCIÓN DE OPERACIONES
RED CONVENCIONAL SUR
JEFATURA DE ÁREA DE
MANTENIMIENTO DE SEVILLA

Dibujado por: J.G.J.
Aprobado por: Jose Angel Gomez Flores
Firma: Firmado digitalmente por Jose Angel Gomez Flores
Fecha: 2024.07.19 11:19:16 +02'00'
Fecha: 19-JULIO-2024

ESQUEMA ELÉCTRICO L.A.C.
P.E. 26 LÍNEA DE BIF. LOS NARANJOS A HUELVA
MAJARABIQUE

Plano nº 1 de 2
Sustituye a: Hoja 1 de 17 de 13/05/2015
Hoja nº 01 de 17

