


AGUJAS	P.K.
123	1/276
121	1/367
2	4/128
4	4/686
6	4/725-2/470

SEÑALES LÍNEA	P.K.	SEÑALES RAMAL	P.K.
E3	2/763	E1	5/033
E2A	3/832	E5	5/033
		E6	4/322
		E8	4/294
		E2C	5/754
		E4	5/754

AGUJAS	P.K.
8	6/046
10	6/119
12	6/127
14	6/199
16	6/347
18	6/442

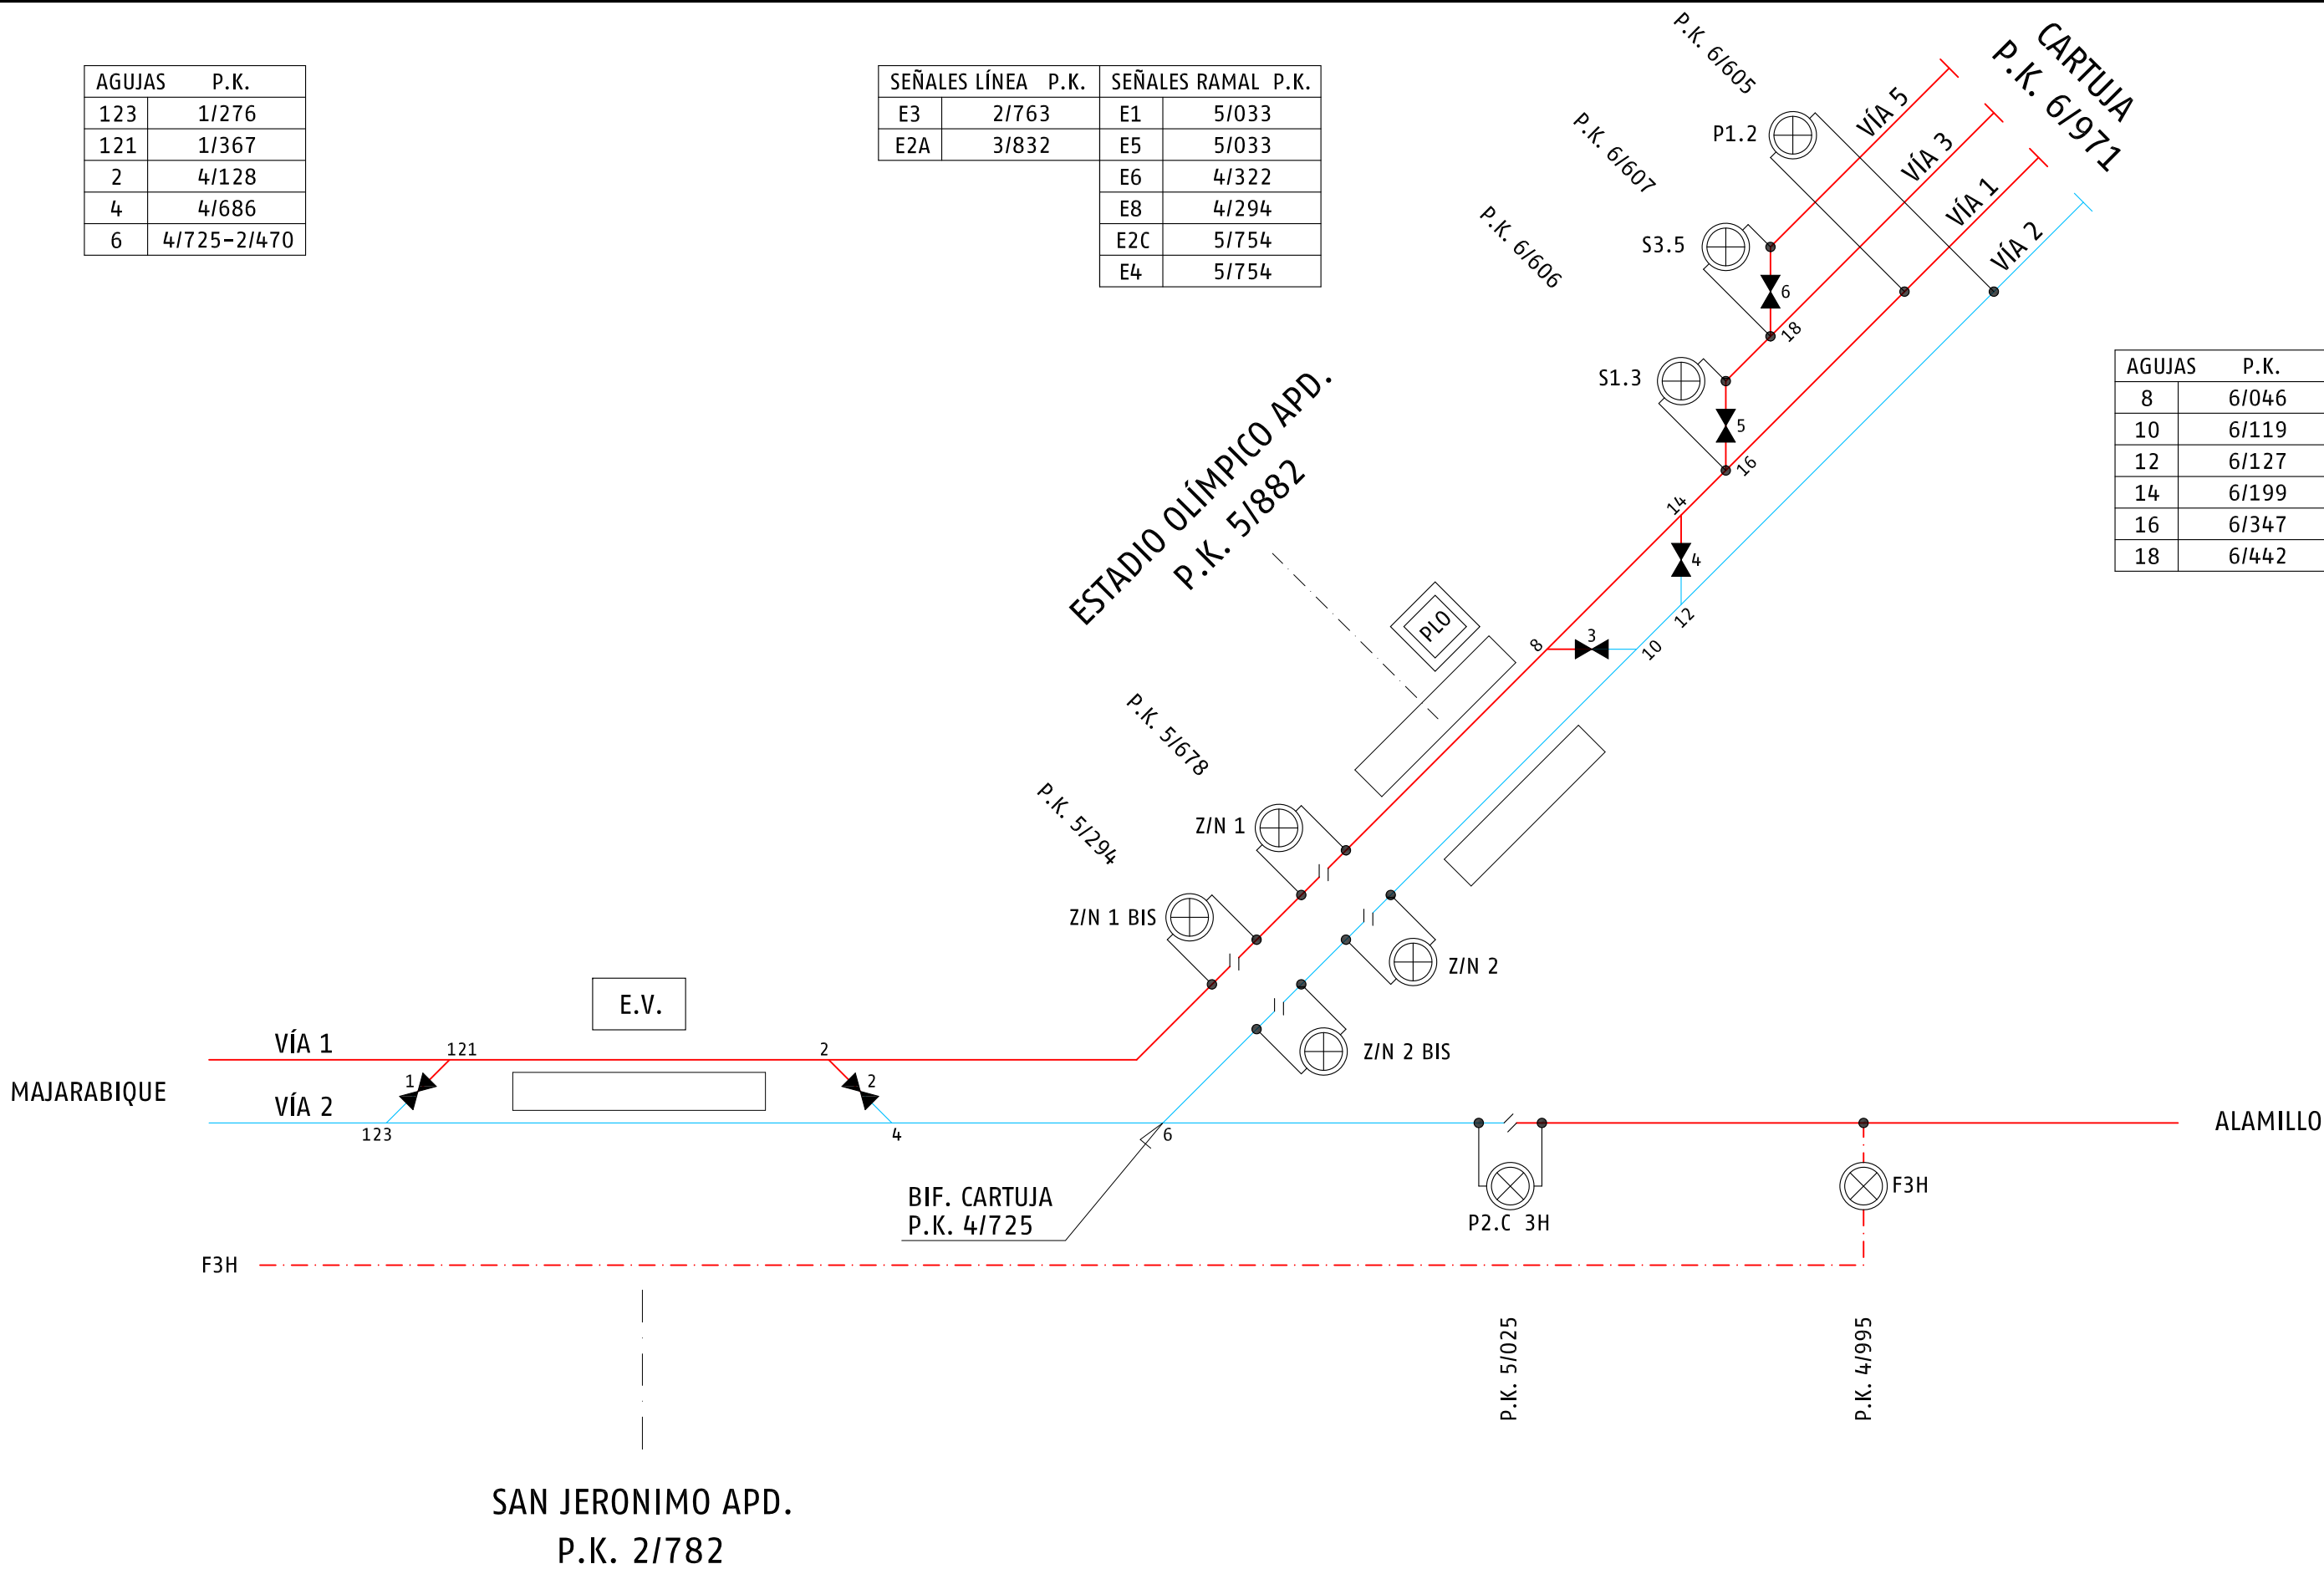

SUBDIRECCIÓN DE OPERACIONES
RED CONVENCIONAL SUR
JEFATURA DE ÁREA DE
MANTENIMIENTO DE SEVILLA

Dibujado por: J.G.J.
Aprobado por: Jose Angel Gomez Flores
Firma: Firmado digitalmente por Jose Angel Gomez Flores
Fecha: 2024.07.19 11:19:16 +02'00'
Fecha: 19-JULIO-2024

ESQUEMA ELÉCTRICO L.A.C.
P.E. 26 LÍNEA DE BIF. LOS NARANJOS A HUELVA
APD. S. JERÓNIMO-APD. ESTADIO-APD. CARTUJA

Plano nº 1 de 1
Sustituye a: Hoja 02 de 17 de 13/05/15
Hoja nº 02 de 17