


AGUJAS	P.K.
2	18/403

SEÑALES	P.K.
E1	21/220
E2	18/128

AGUJAS	P.K.
1	19/148
3	18/795

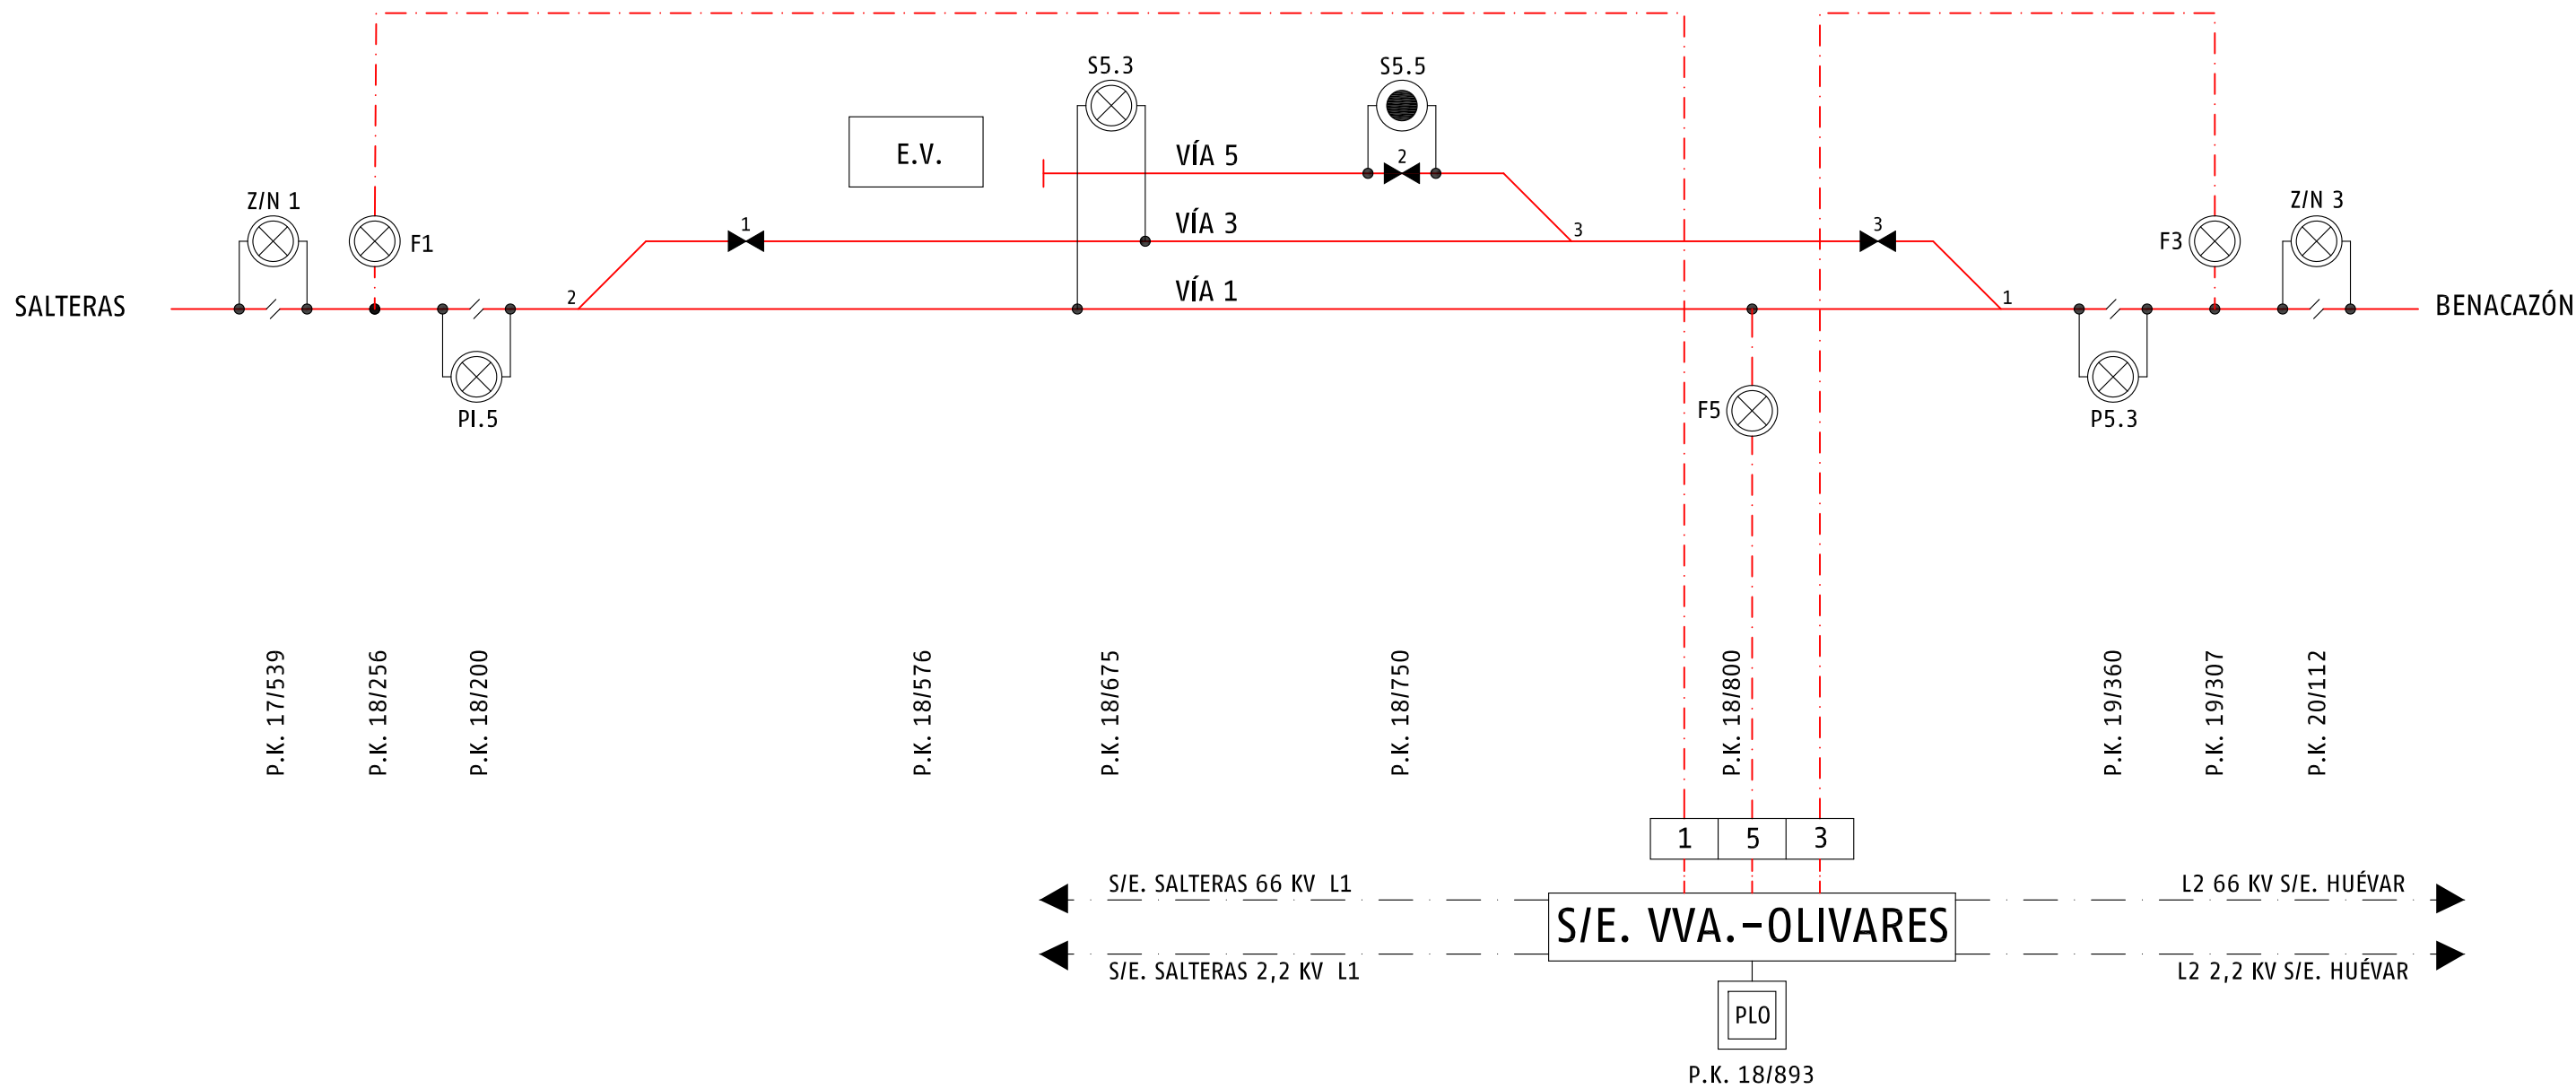

NOTA: Esquema que no cumple con la NAE 112



SUBDIRECCIÓN DE OPERACIONES
RED CONVENCIONAL SUR
JEFATURA DE ÁREA DE
MANTENIMIENTO DE SEVILLA

Dibujado por: J.G.J.

Aprobado por: Jose Angel Gomez Flores
Firma: Firmado digitalmente por Jose Angel Gomez Flores
Fecha: 2024.07.19 11:19:16 +02'00'

Fecha: 19-JULIO-2024

ESQUEMA ELÉCTRICO L.A.C.
P.E. 26 LÍNEA DE BIF. LOS NARANJOS A HUELVA
VILLANUEVA Y OLIVARES

Plano nº 1 de 1

Sustituye a: Hoja 6 de 17 de 13/05/15

Hoja nº 6 de 17