


AGUJAS	P.K.
2	26/763
4	26/993

SEÑALES	P.K.
E1	27/685
E2	26/373

AGUJAS	P.K.
1	27/410
3	27/337

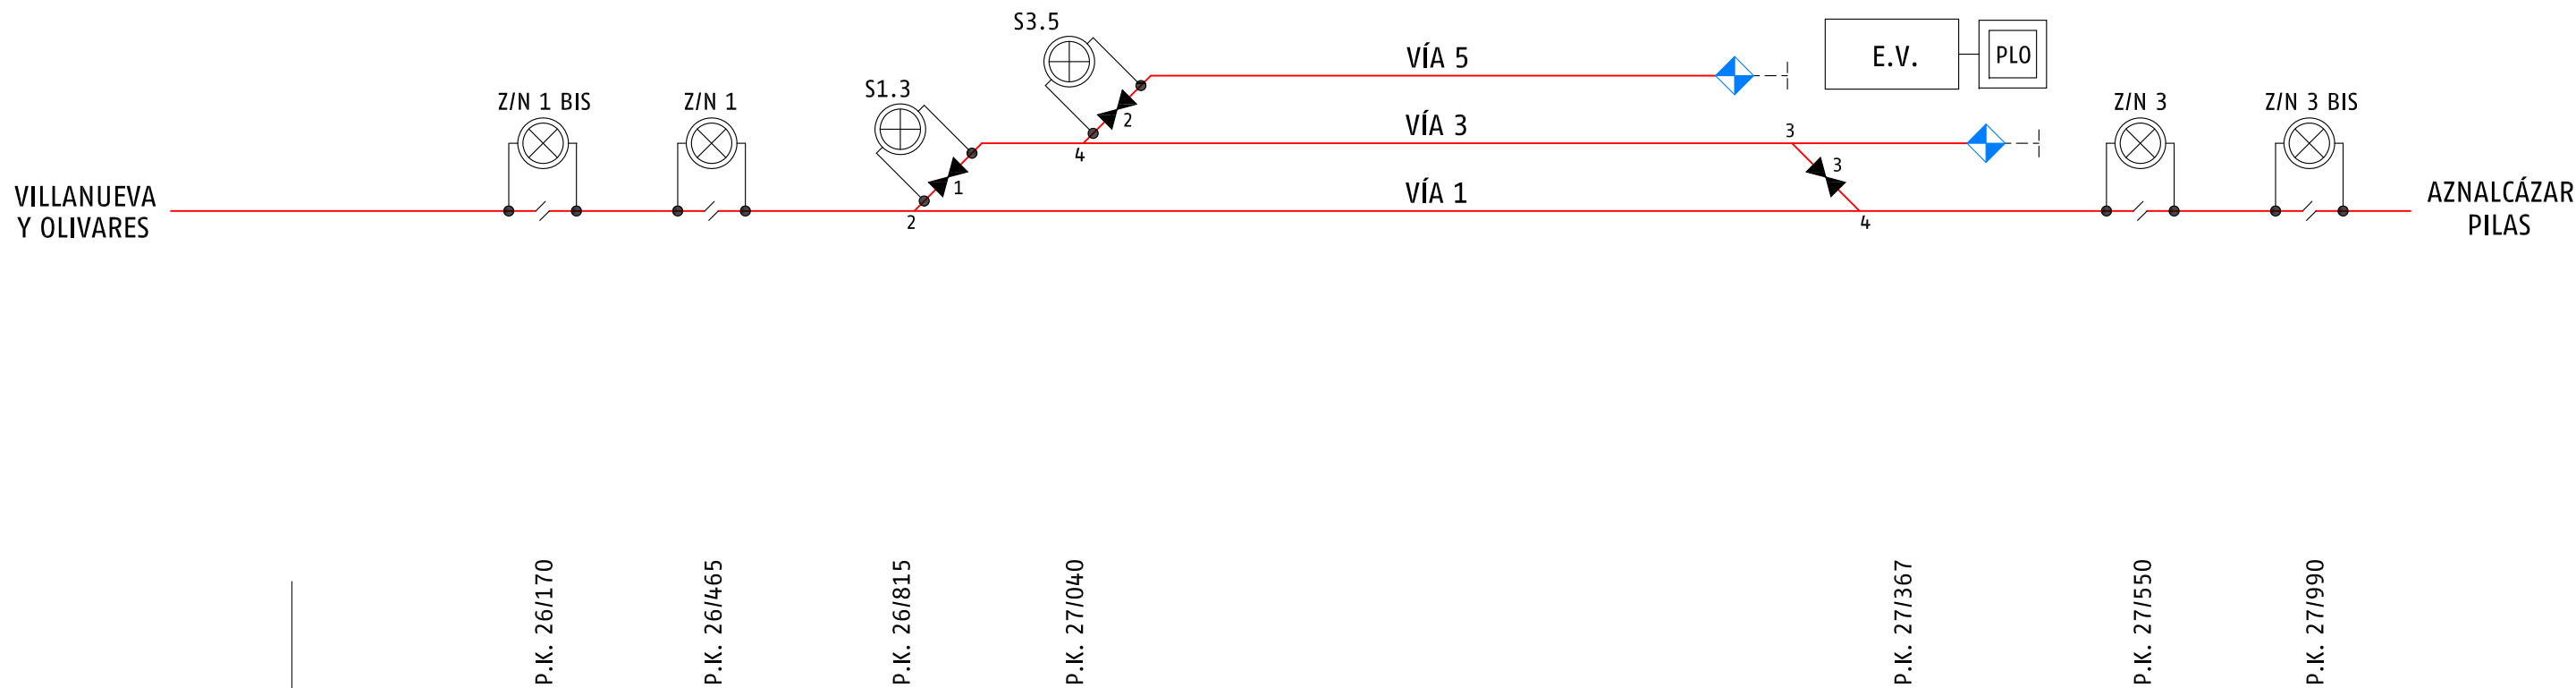

SANLÚCAR LA MAYOR
P.K. 24/112



SUBDIRECCIÓN DE OPERACIONES
RED CONVENCIONAL SUR
JEFATURA DE ÁREA DE
MANTENIMIENTO DE SEVILLA

Dibujado por:	J.G.J.
Aprobado por:	Jose Angel Gomez Flores
Firma	Firmado digitalmente por Jose Angel Gomez Flores Fecha: 2024.07.19 11:19:16 +02'00'
Fecha:	19-JULIO-2024

ESQUEMA ELÉCTRICO L.A.C.
P.E. 26 LÍNEA DE BIF. LOS NARANJOS A HUELVA
BENACAZÓN

Plano nº	1 de 1
Sustituye a:	Hoja 7 de 17 de 13/05/15
Hoja nº	7 de 17