


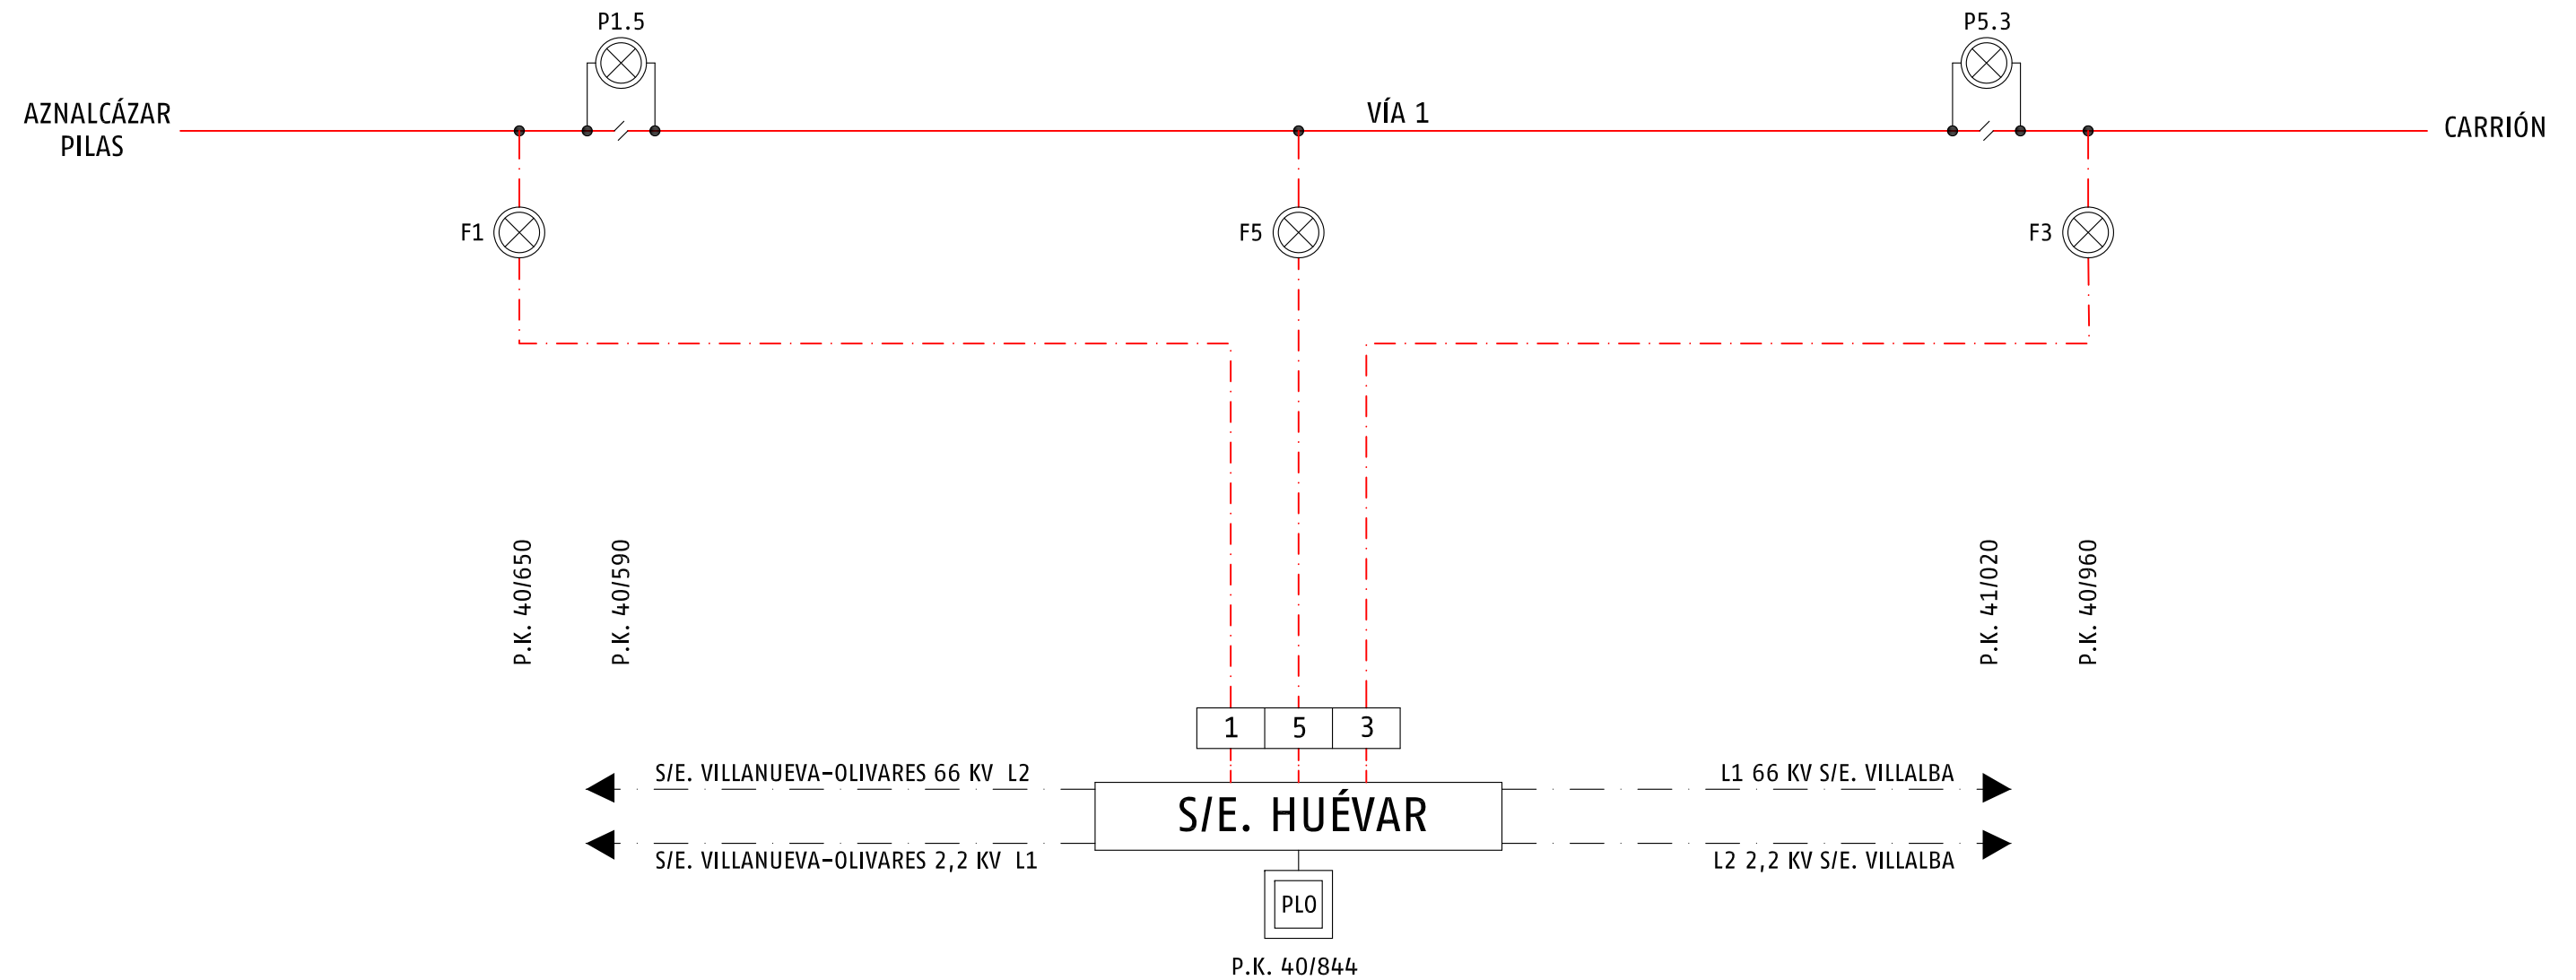

NOTA: Esquema que no cumple con la NAE 112



SUBDIRECCIÓN DE OPERACIONES
RED CONVENCIONAL SUR
JEFATURA DE ÁREA DE
MANTENIMIENTO DE SEVILLA

Dibujado por: J.G.J.
Aprobado por: Jose Angel Gomez Flores
Firma: Firmado digitalmente por Jose Angel Gomez Flores
Fecha: 2024.07.19 11:19:16 +02'00'
Fecha: 19-JULIO-2024

ESQUEMA ELÉCTRICO L.A.C.
P.E. 26 LÍNEA DE BIF. LOS NARANJOS A HUELVA
HUÉVAR

Plano nº 1 de 1
Sustituye a: Hoja 9 de 17 de 16/10/13
Hoja nº 9 de 17